



DOCK LEVELER TOP VIEW


BOM (For Single Dock Leveler)		
SL NO.	DESCRIPTION	QTY
1	Dock Leveler(1820m x 5000mm)	1No
2	Lip (1820 x250mm)	1No
3	Deck Cylinder	2Nos
4	Lip Cylinder	1No
5	Power Pack(1HP,3Phase)	1No
6	Control Panel	1No

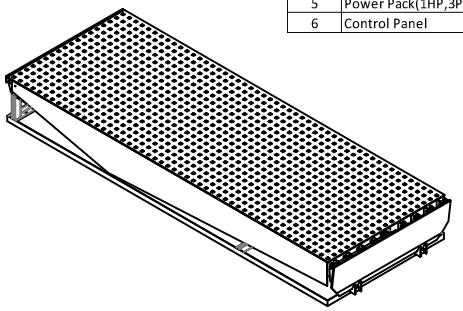


ISOMETRIC VIEW OF DOCK LEVELER

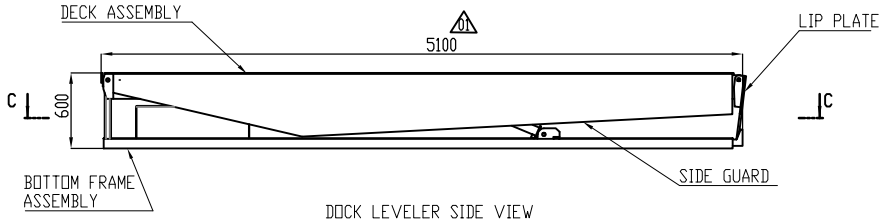

DOCK LEVELER SIDE VIEW

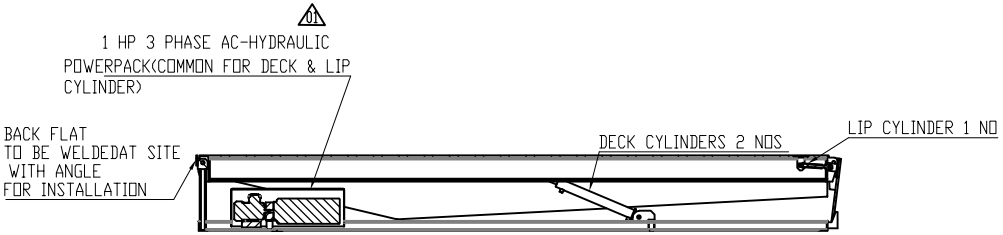

SECTION B-B
SCALE 1 : 15

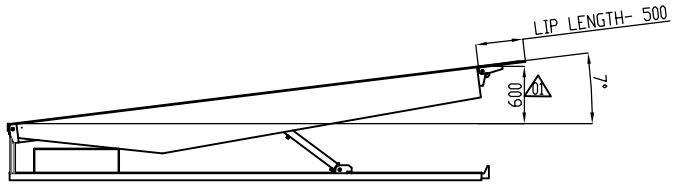

DECK UP HEIGHT - 600 MM




DECK DOWN HEIGHT - 300 MM

01

TECHNICAL SPECIFICATIONS OF PIT MOUNTED ELECRO-HYDRAULIC DOCK LEVELER -

1. SIZE OF DOCK LEVELER = 1820mm(W) X 5000mm(L)
2. OVERALL SIZE OF PRODUCT = 1820mm(W)X5100mm(L)X600mm(D)
3. CAPACITY = 6 TON POINT LOAD
4. LIP PLATE SIZE = 500mm(L)X1820mm(W)
5. DECK PLATE = CHEQUERED SHEET 1820mm(W)x5000mm(L)
6. DECK & LIP UP=DOWN OPERATION BY HYDRAULIC CYLINDER
7. DECK UP HEIGHT= (+)600 MM
8. DECK DOWN HEIGHT= (-)300MM
9. HEIGHT OF DOCK LEVELER FROM ROAD LEVEL= 900 mm,
10. OPERATION CONTROL BY PUSH BUTTONS ON CONTROL PANEL MOUNTED ON STAND NEAR DOCK LEVELER
11. ELECTRICAL SUPPLY OF EQUIPMENT= 415 VOLT 3 PHASE AC , 50HZ
12. PAINT = FIROZI BLUE
13. MATERIAL OF CONSTRUCTION = MILD STEEL AS PER IS STANDARD
14. MANUFACTURING STANDARD OF DOCK LEVELER =EN1398
15. ELECRICAL MOTOR COMPLIANCE ZONE 1-IIC-T3 HAZARDOUS AREA
16. PIT SIZE = 1870 mm(W)X5100mm(L)x600 mm(D)
17. DOCK LEVELER FIXING IN PIT BY ANCHOR BOLT .
18. REQUIRED PIT & ALL CIVIL WORK FOR MOUNTING OD DOCK LEVELER IS IN LTHE SCOPE .
    REFER PIT DRAWING FOR CONSTRUCTION OF PIT B016-RUF-LT-504-MP-DW-NTPL(1)-13005
19. HYDRAULIC CYLINDERS & POWERPACK IS DESIGNED FOR LIFTING BARE DOCK ONLY.
20. MOTOR RATING=1HP 3 PHASE AC-HYDRAULIC
21. All ELECTRICAL EQUIPMENTS SHALL HAVE PAINT SHADE RAL 7031
22. FLAME PROOF CONTROL PANEL 350X350X145MM

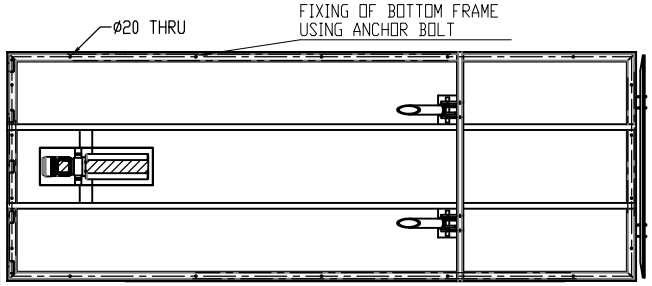

SECTION C-C
SCALE 1 : 15

504-LZ-930A/B — CIVIL DRAWING OF DOCK LEVELER — 01
DRAWING NO. — DRAWING TITLE — REV
REFERENCE DOCUMENTS / DRAWINGS

REV	DESCRIPTION	DRN	CHECKED	APPROVED	REVIEWED	APPROVED	DATE
01	ISSUED FOR APPROVAL	SNS	VJ	AK			

OWNER: HINDUSTAN PETROLEUM CORPORATION LIMITED
VISAKH REFINERY MODERNISATION PROJECT
EPCC-03 PACKAGE FOR RESIDUE UP-GRADATION FACILITY (RUF)
PMC: Engineers India Limited
LSTK CONTRACTOR: L&T Hydrocarbon Engineering
DETAILED ENGINEERING CENTER: L&T - CHIYODA LIMITED
VENDOR: M/s VIMVA TECHNOLOGIES PVT LTD
VENDOR PO NO: REFINARY/75000-82256/VMM
VENDOR DWG. NO: NBMVA_20-21_0157
DATE: 31/05/21 SCALE: 1:4
TITLE: 504-LZ-930A/B GAD FOR DOCK LEVELER
DEPT: DESIGN
DRN BY: SNS
CHK BY: VJ
APP BY: AK
PROJECT: L&T-RUF
PRO NO.:
ORG. NO.: B016-RUF-LT-504-MP-DW-NTPL(1)-13005
SH.9 OF 9
REV. 01
CAD FILE:

L&T - CHIYODA LIMITED
GENERATED BY | REVIEWED BY | APPROVED BY | DATE