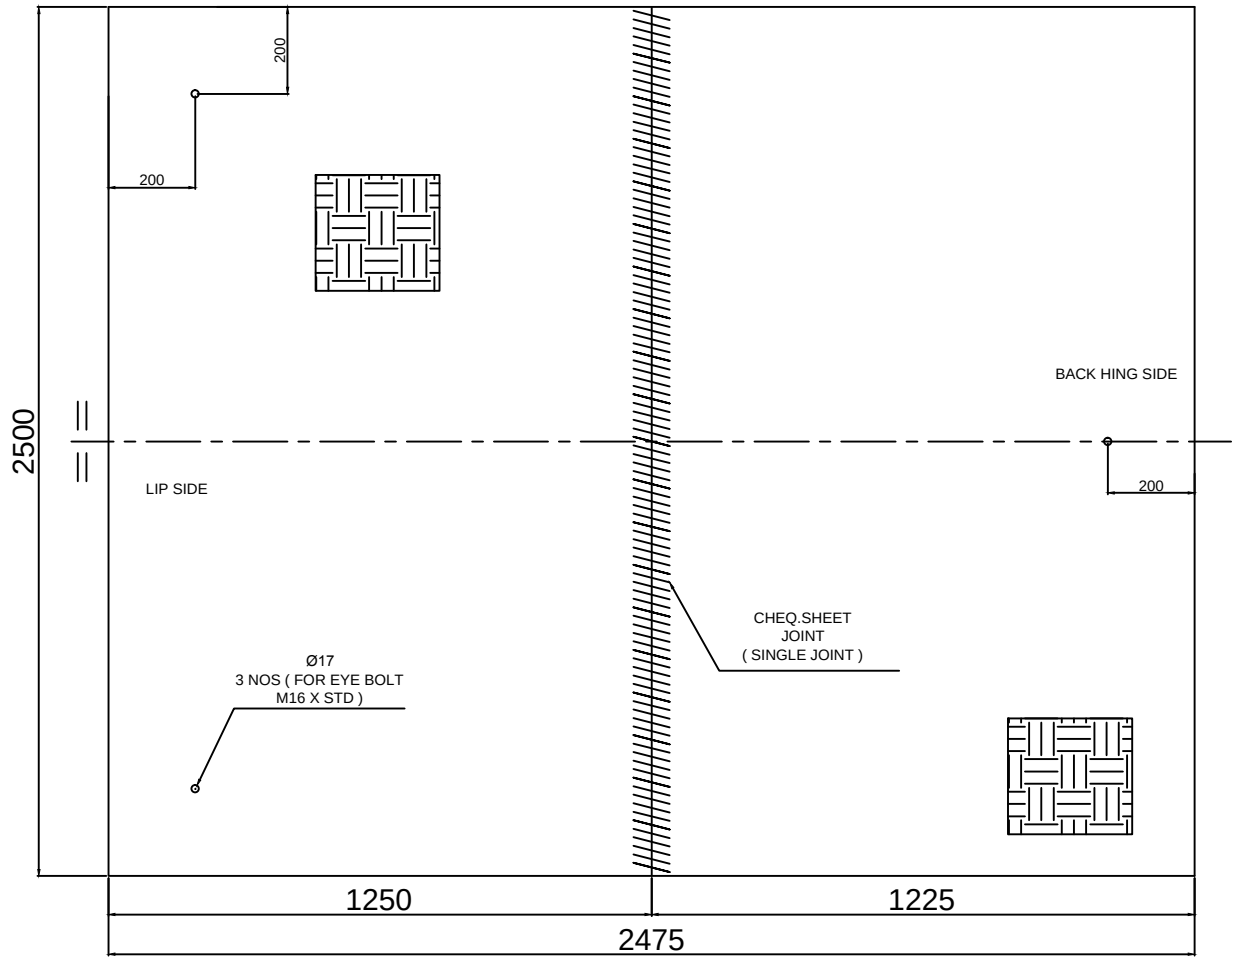


This drawing & design is the property of NIHVA TECHNOLOGIES. Not to be sold or copied to any other concern.

TITLE

DECK CHEQ.SHEET

NIHVA TECHNOLOGIES PVT. LTD.

NIHVA TECHNOLOGIES PVT. LTD. PUNE
Tel : 020 66304033
Email:- info@nihva.com
Website:- www.nihva.com

	NAME	SIGN	DATE
DRAWN	PRADEEP		23.04.2018
CHECK	PRADEEP		23.04.2018
APPRD.	PRADEEP		23.04.2018

If any queries contact : design@nihva.com

ALL DIMENSION ARE IN mm

CLIENT -

PROJECT - DLMP1004

SITE LOCATION -

DWG. NO. : NIHVA/18-19/DLMP1004_006_002

SCALE: NTS | WT: | REV- 00