



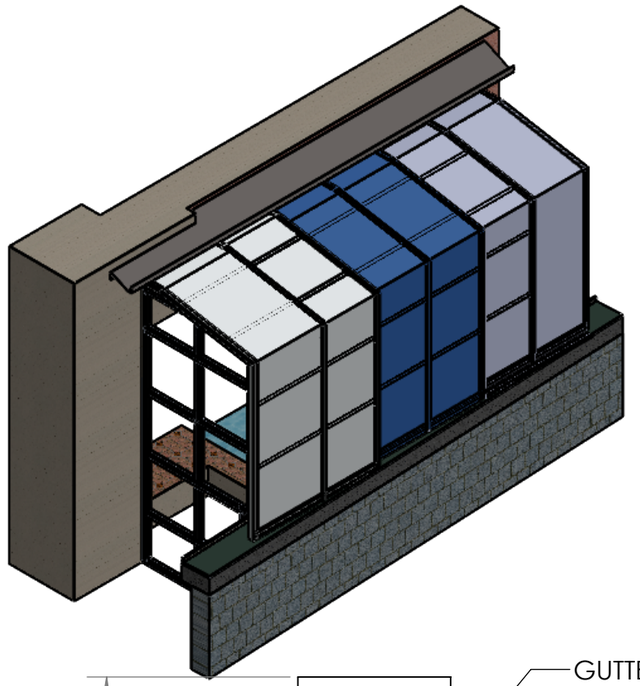


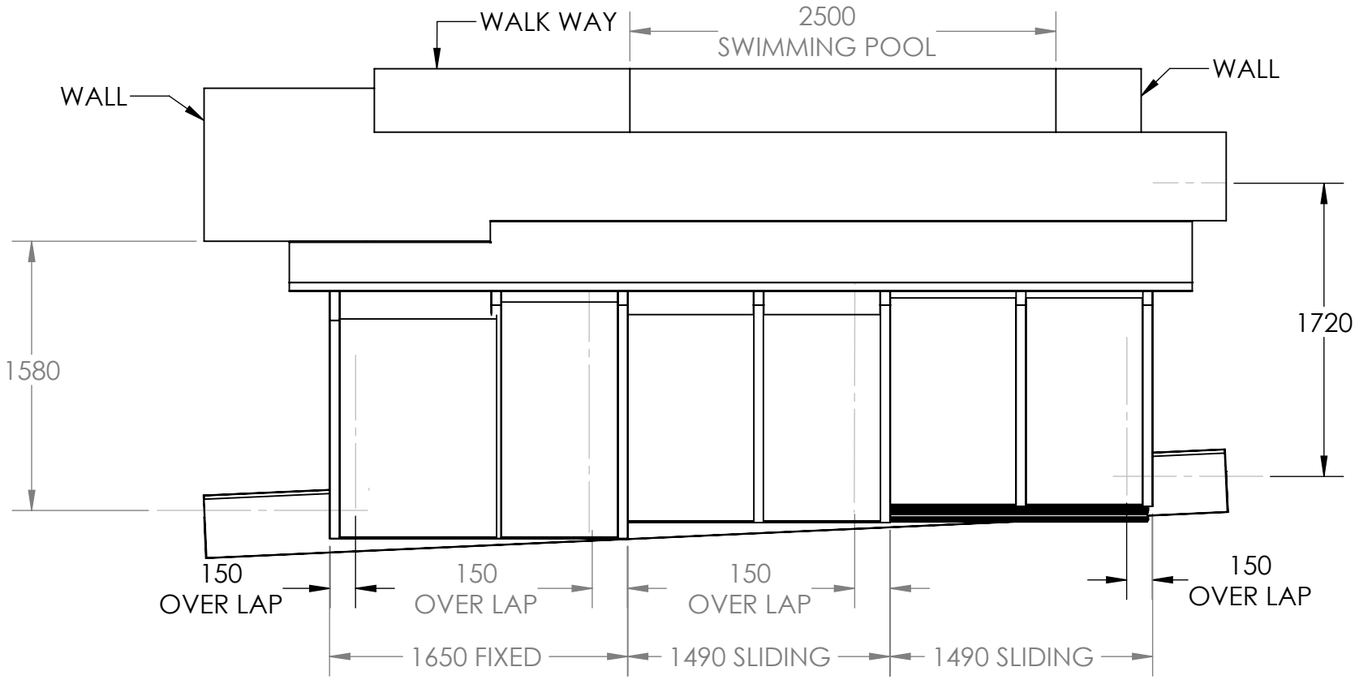

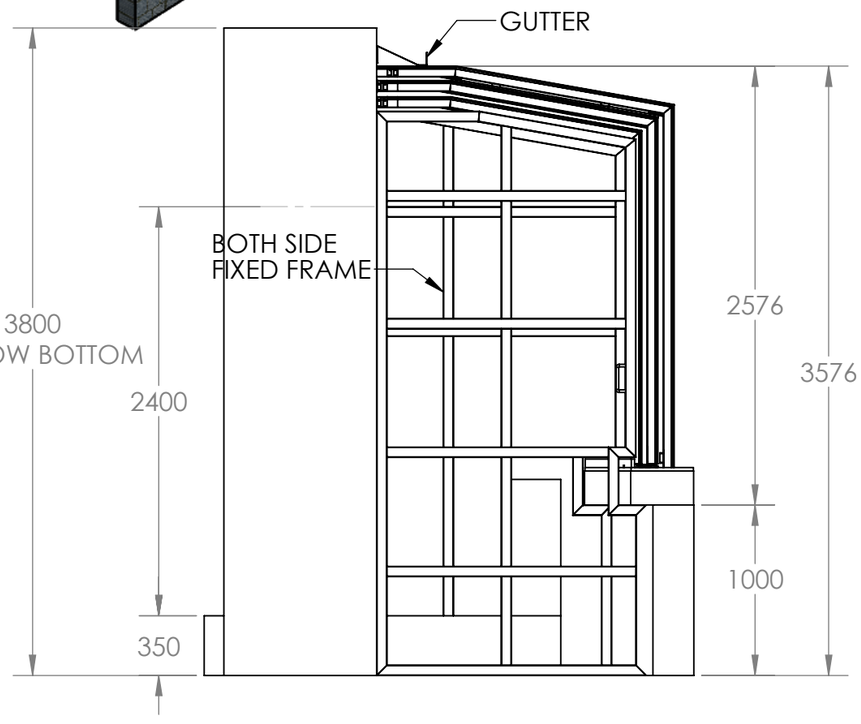


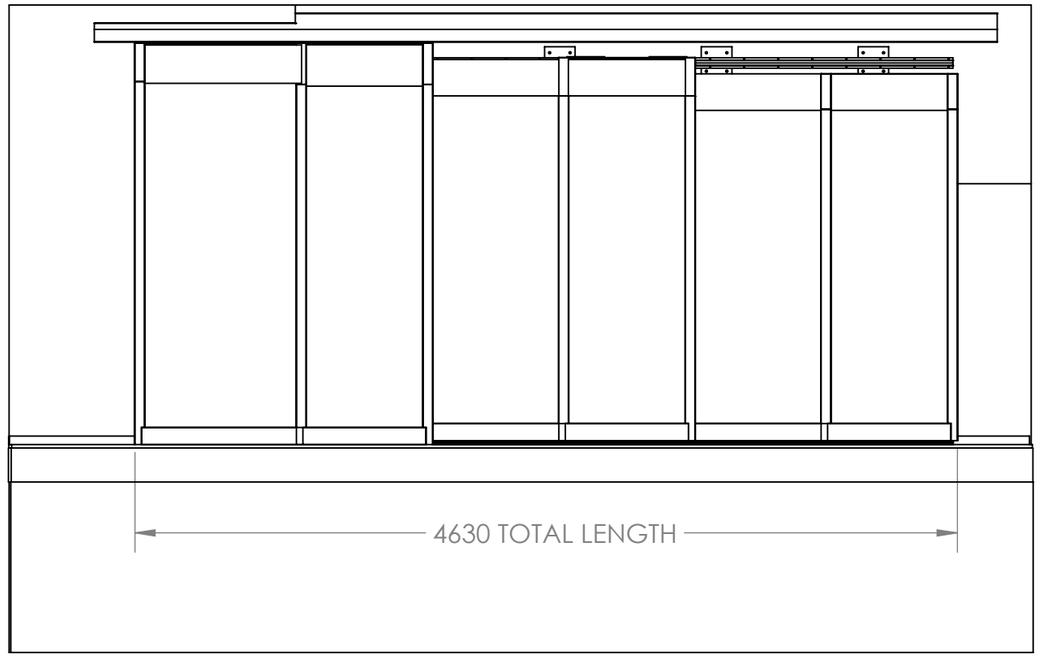



-				NIHVA TECHNOLOGIES PVT.LTD.PUNE Website - www.nihva.com
DWG NO - NTPL-234			QTY - 1	
	NAME	SIGNATURE	DATE	PROJECT NO - NTPL-234
DRAWN	B.B.		28.06.2024	PRODUCT - MANUALLY BALCONY ENCLOSURE
CHK'D	B.B.		28.06.2024	SITE LOCATION -
APPV'D	V.T.		28.06.2024	
if any queries contact - supportautomation@nihva.com				REVISION - 02
ALL DIMENSION ARE IN mm			A3	SCALE - SHEET 1 OF 3

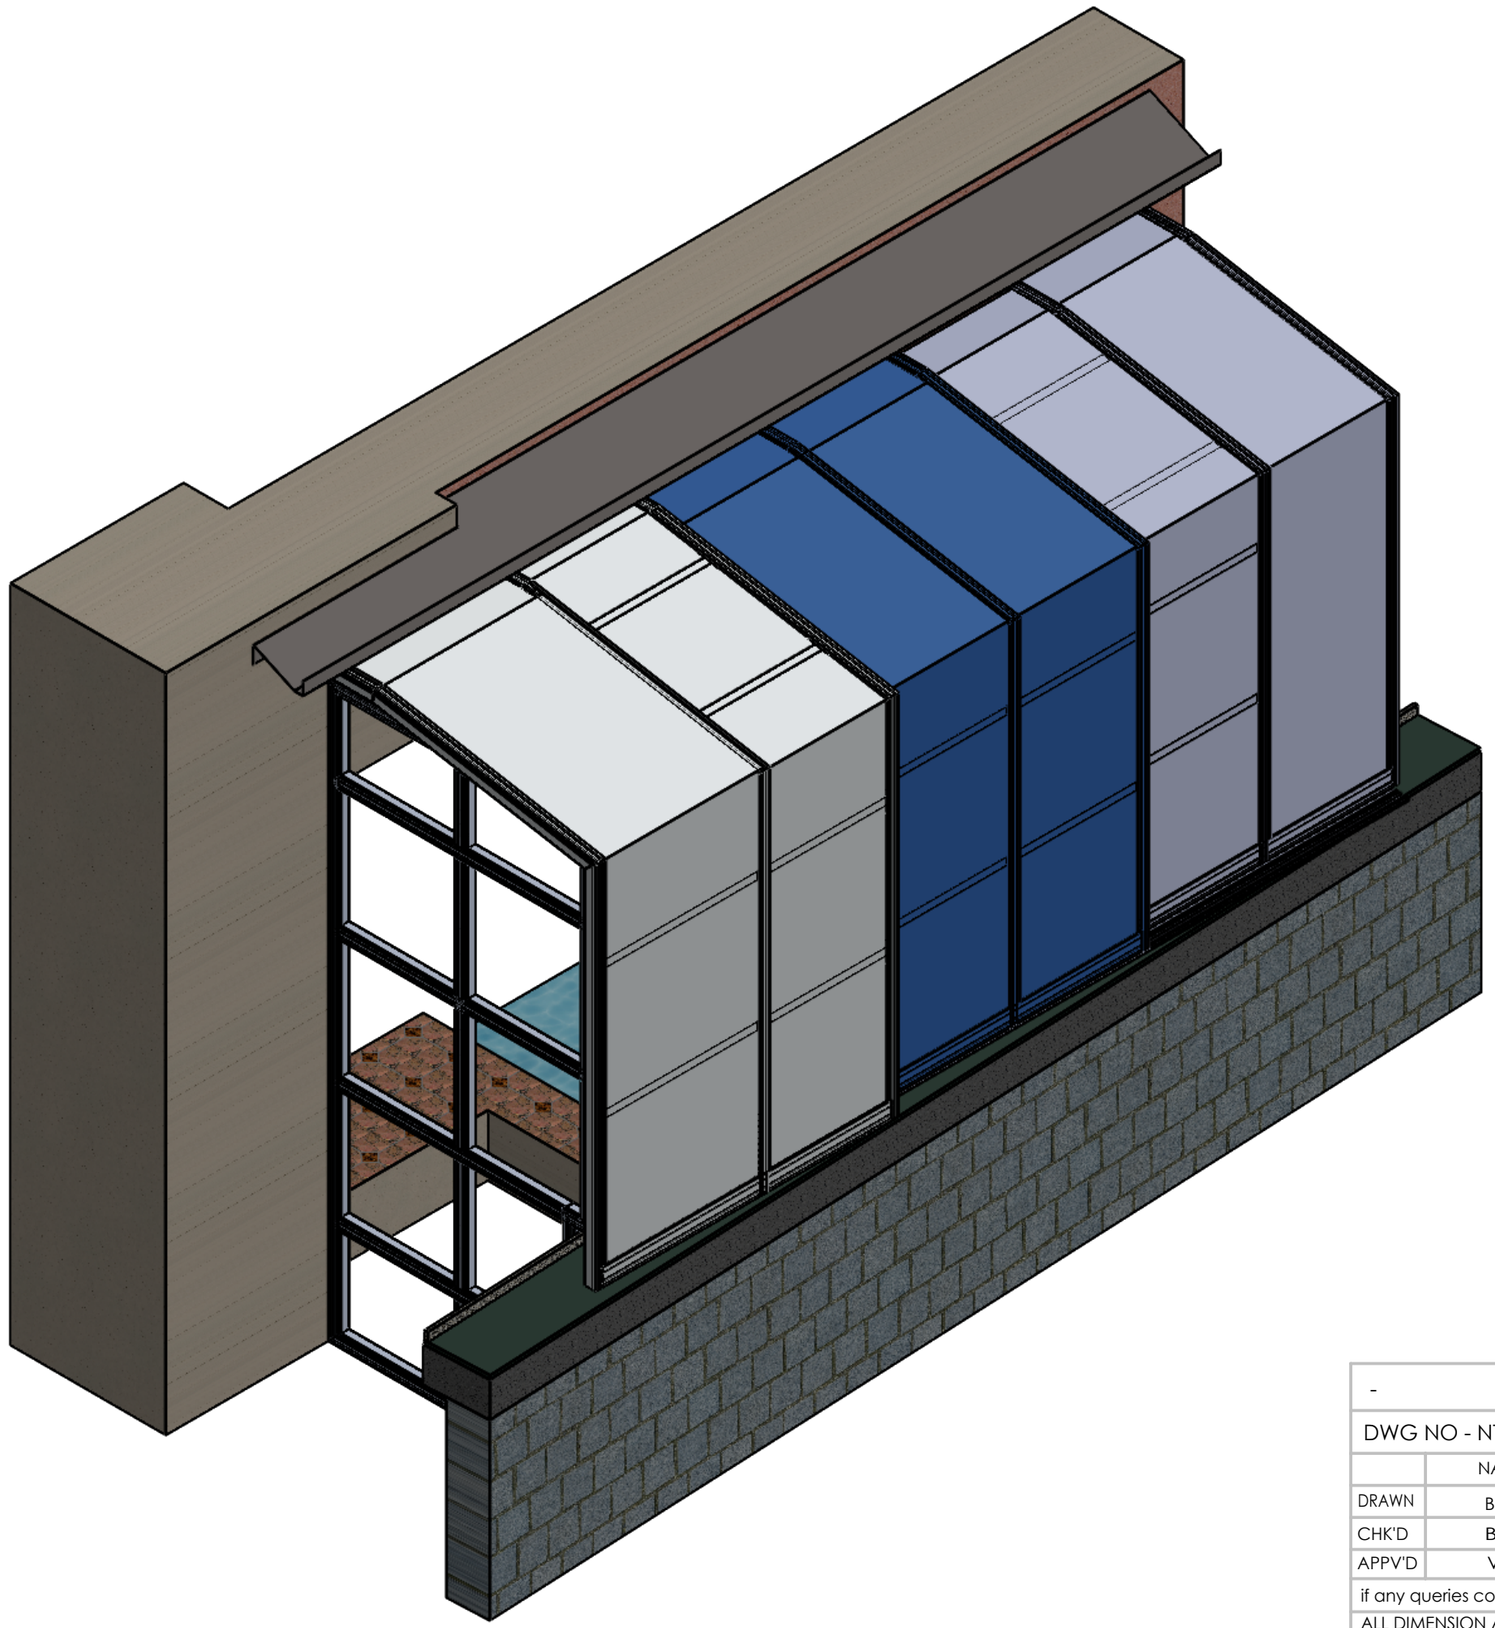



-				NIHVA TECHNOLOGIES PVT.LTD.PUNE Website - www.nihva.com
DWG NO - NTPL-234			QTY - 1	
	NAME	SIGNATURE	DATE	PROJECT NO - NTPL-234
DRAWN	B.B.		28.06.2024	PRODUCT - MANUALLY BALCONY ENCLOSURE
CHK'D	B.B.		28.06.2024	SITE LOCATION -
APPV'D	V.T.		28.06.2024	
if any queries contact - supportautomation@nihva.com				REVISION - 02
ALL DIMENSION ARE IN mm			A3	SCALE - SHEET 2 OF 3

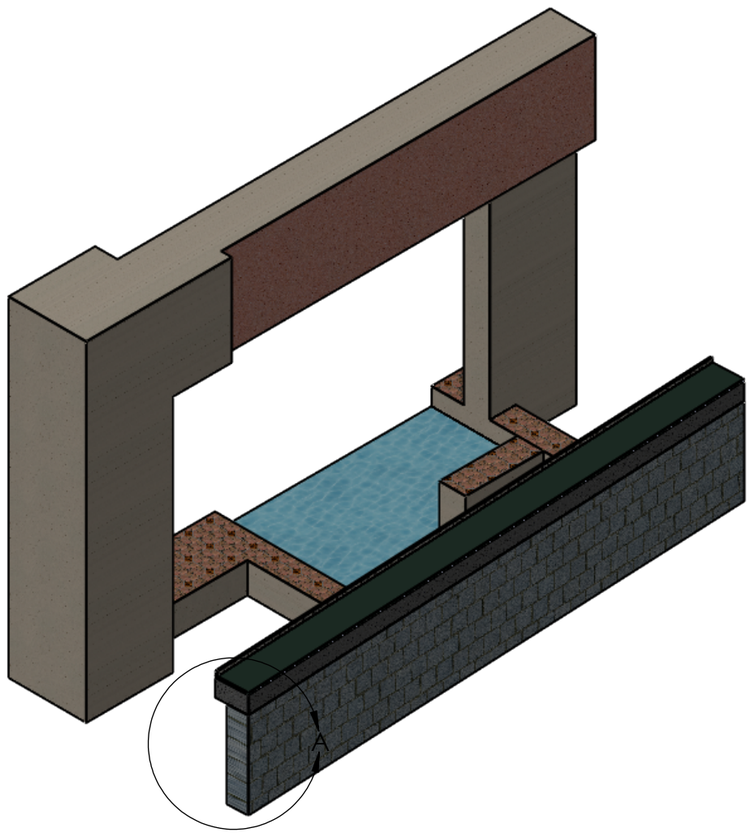

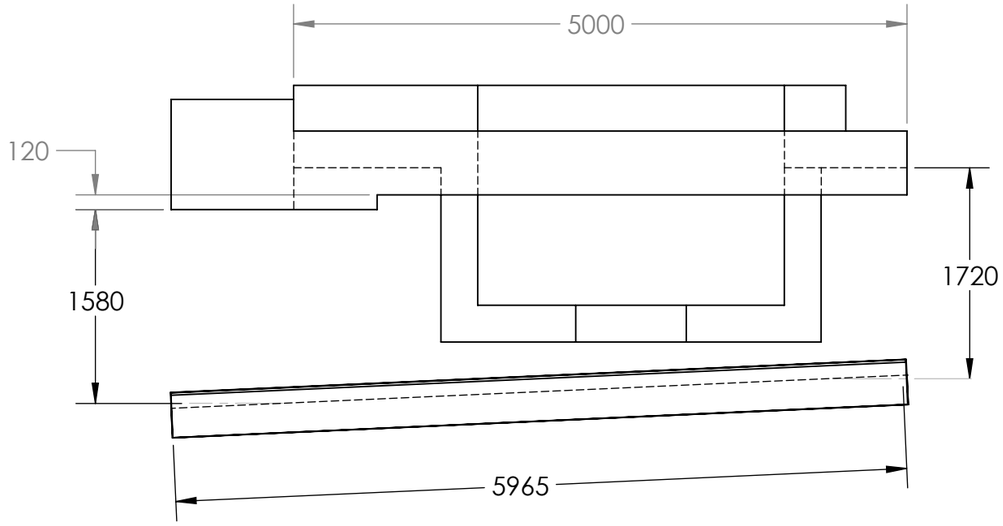

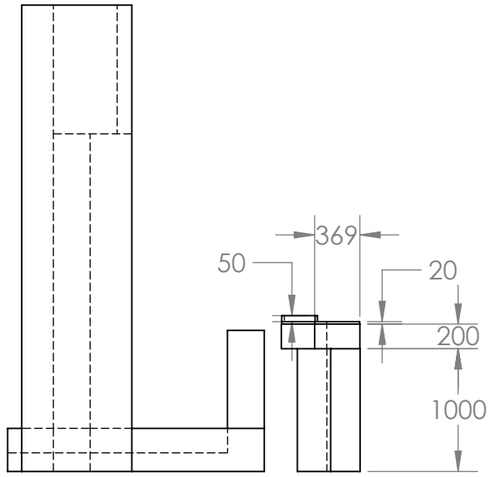

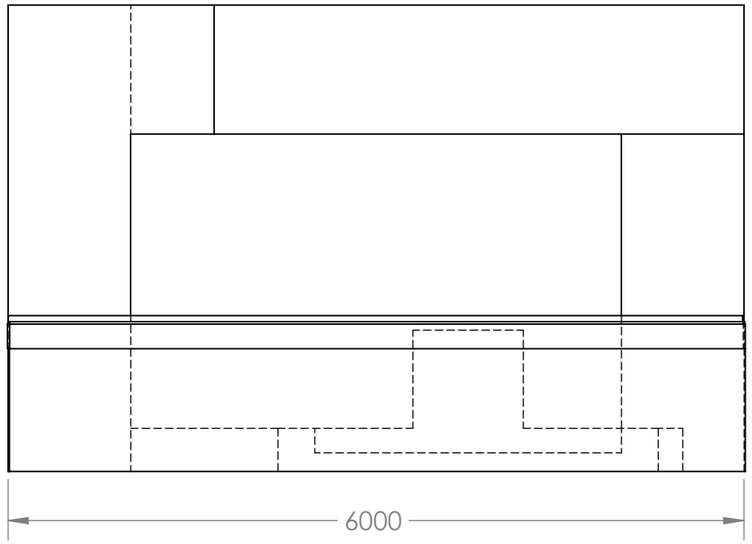

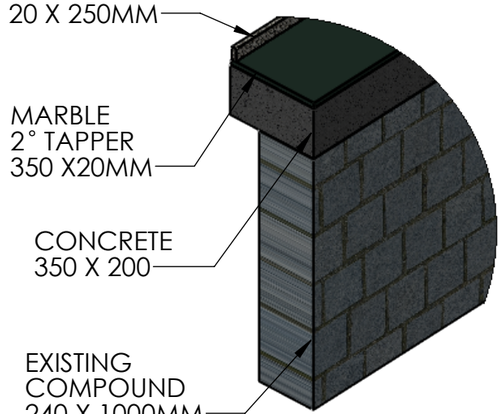

DETAIL A
SCALE 1 : 20

-				NIHVA TECHNOLOGIES PVT.LTD.PUNE Website - www.nihva.com
DWG NO - NTPL-234			QTY - 1	
	NAME	SIGNATURE	DATE	PROJECT NO - NTPL-234
DRAWN	B.B.		28.06.2024	PRODUCT - BALCONY ENCLOSURE CIVIL DRAWING
CHK'D	B.B.		28.06.2024	SITE LOCATION -
APPV'D	V.T.		28.06.2024	
if any queries contact - supportautomation@nihva.com				REVISION - 02
ALL DIMENSION ARE IN mm			A3	SCALE - SHEET 3 OF 3