



DOCK LEVELER TOP VIEW

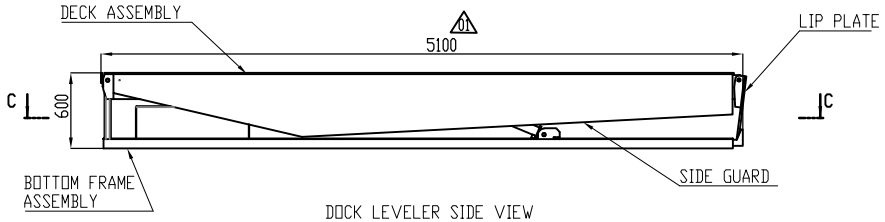


DOCK LEVELER SIDE VIEW

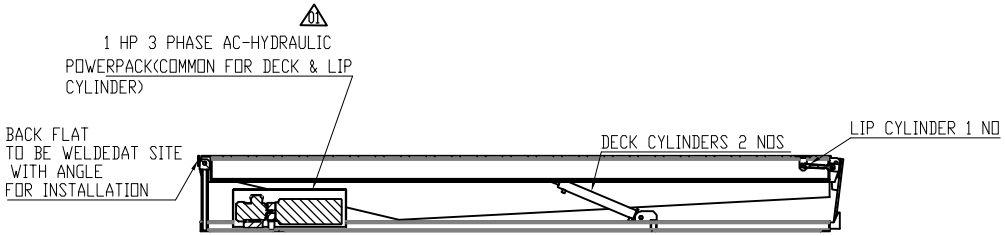


SECTION B-B
SCALE 1 : 15


BOM (For Single Dock Leveler)		
SL NO.	DESCRIPTION	QTY
1	Dock Leveler(1820m x 5000mm)	1No
2	Lip (1820 x500mm)	1No
3	Deck Cylinder	2Nos
4	Lip Cylinder	1No
5	Power Pack(1HP,3Phase)	1No
6	Control Panel	1No

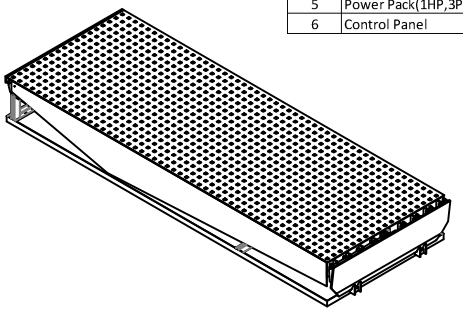

ISOMETRIC VIEW OF DOCK LEVELER

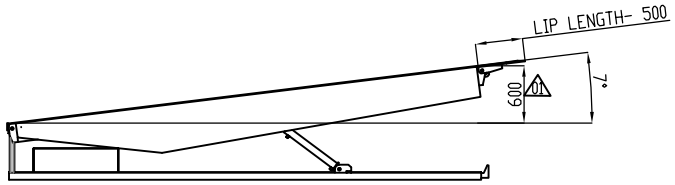


DECK UP HEIGHT - 600 MM

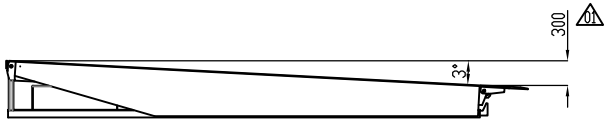

DECK DOWN HEIGHT - 300 MM


40MM CUTOUT AT THE CENTRE OF THE TUBE FOR WATER DRAINNG

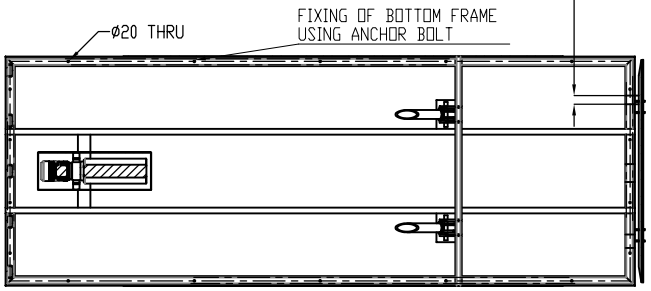

SECTION C-C
SCALE 1 : 15

TECHNICAL SPECIFICATIONS OF PIT MOUNTED ELECRO-HYDRAULIC DOCK LEVELER -

1. SIZE OF DOCK LEVELER = 1820mm(W) X 5000mm(L)
2. OVERALL SIZE OF PRODUCT = 1820mm(W)X5100mm(L)X600mm(D)
3. CAPACITY = 6 TON POINT LOAD
4. LIP PLATE SIZE = 500mm(L)X1820mm(W)
5. DECK PLATE = CHEQUERED SHEET 1820mm(W)x5000mm(L)
6. DECK & LIP UP=DOWN OPERATION BY HYDRAULIC CYLINDER
7. DECK UP HEIGHT= (+)600 MM
8. DECK DOWN HEIGHT= (-)300MM 02
9. HEIGHT OF DOCK LEVELER FROM ROAD LEVEL= 900 mm,
10. OPERATION CONTROL BY PUSH BUTTONS ON CONTROL PANEL MOUNTED ON STAND NEAR DOCK LEVELER
11. ELECTRICAL SUPPLY OF EQUIPMENT= 415 VOLT 3 PHASE AC , 50HZ
12. PAINT = FIROZI BLUE
13. MATERIAL OF CONSTRUCTION = MILD STEEL AS PER IS STANDARD
14. MANUFACTURING STANDARD OF DOCK LEVELER =EN1398
15. ELECRICAL MOTOR COMPLIANCE ZONE 1-IIC-T3 HAZARDOUS AREA
16. PIT SIZE = 1870 mm(W)X5100mm(L)x600 mm(D)
17. DOCK LEVELER FIXING IN PIT BY ANCHOR BOLT .
18. REQUIRED PIT & ALL CIVIL WORK FOR MOUNTING OD DOCK LEVELER IS IN LTHE SCOPE .
    REFER PIT DRAWING FOR CONSTRUCTION OF PIT B016-RUF-LT-504-MP-DW-NTPL(1)-13005
19. HYDRAULIC CYLINDERS & POWERPACK IS DESIGNED FOR LIFTING BARE DOCK ONLY.
20. MOTOR RATING=1HP 3 PHASE AC-HYDRAULIC
21. All ELECTRICAL EQUIPMENTS SHALL HAVE PAINT SHADE RAL 7031 02
22. ALL FLAME PROOF CONTROL PANEL 360X360X210MM 02
23. WEIGHT= APPROX 2500KG EMPTTY & 8500KG OPERATING 02
24. WE WILL PROVIDE FRP CANOPY FOR LOCAL CONTROL PANEL. 02

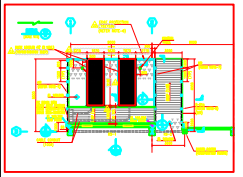

504-LZ-930A/B	CIVIL DRAWING OF DOCK LEVELER				01
DRAWING NO.	DRAWING TITLE				REV
REFERENCE DOCUMENTS / DRAWINGS					
REV	DESCRIPTION	DRN	CHECKED	APPROVED	REVIEWED	APPROVED	DATE
01	ISSUED FOR APPROVAL	SMS	VJ	AK			
00	ISSUED FOR CONSTRUCTION	SMS	VJ	AK			

OWNER: HINDUSTAN PETROLEUM CORPORATION LIMITED
VISAKH REFINERY MODERNIZATION PROJECT
EPCC-03 PACKAGE FOR RESIDUE UP-GRADATION FACILITY (RUF)

PMC: EIL ENGINEERS INDIA LIMITED

LSTK CONTRACTOR: L&T Hydrocarbon Engineering

DETAILED ENGINEERING CENTER: L&T - CHIYODA LIMITED

VENDOR: NIRVA TECHNOLOGIES PVT LTD	VENDOR PO NO: REFINARY/75000-82256/VNM
	VENDOR DWG. NO: NBHVA_20-21_0157
DATE: 31.05.21	SCALE: 1:4
DEPT: DESIGN	TITLE: GAD FOR DOCK LEVELER (504-LZ-930A/B)
DRN BY: SMS	PROJECT: L&T-RUF
CHK BY: VJ	DWG. NO.: B016-RUF-LT-504-MP-DW-NTPL(1)-13005
APP BY: AK	PRO NO.:
	SH.1 OF 4
	REV. 02
	CAD FILE:

L&T - CHIYODA LIMITED