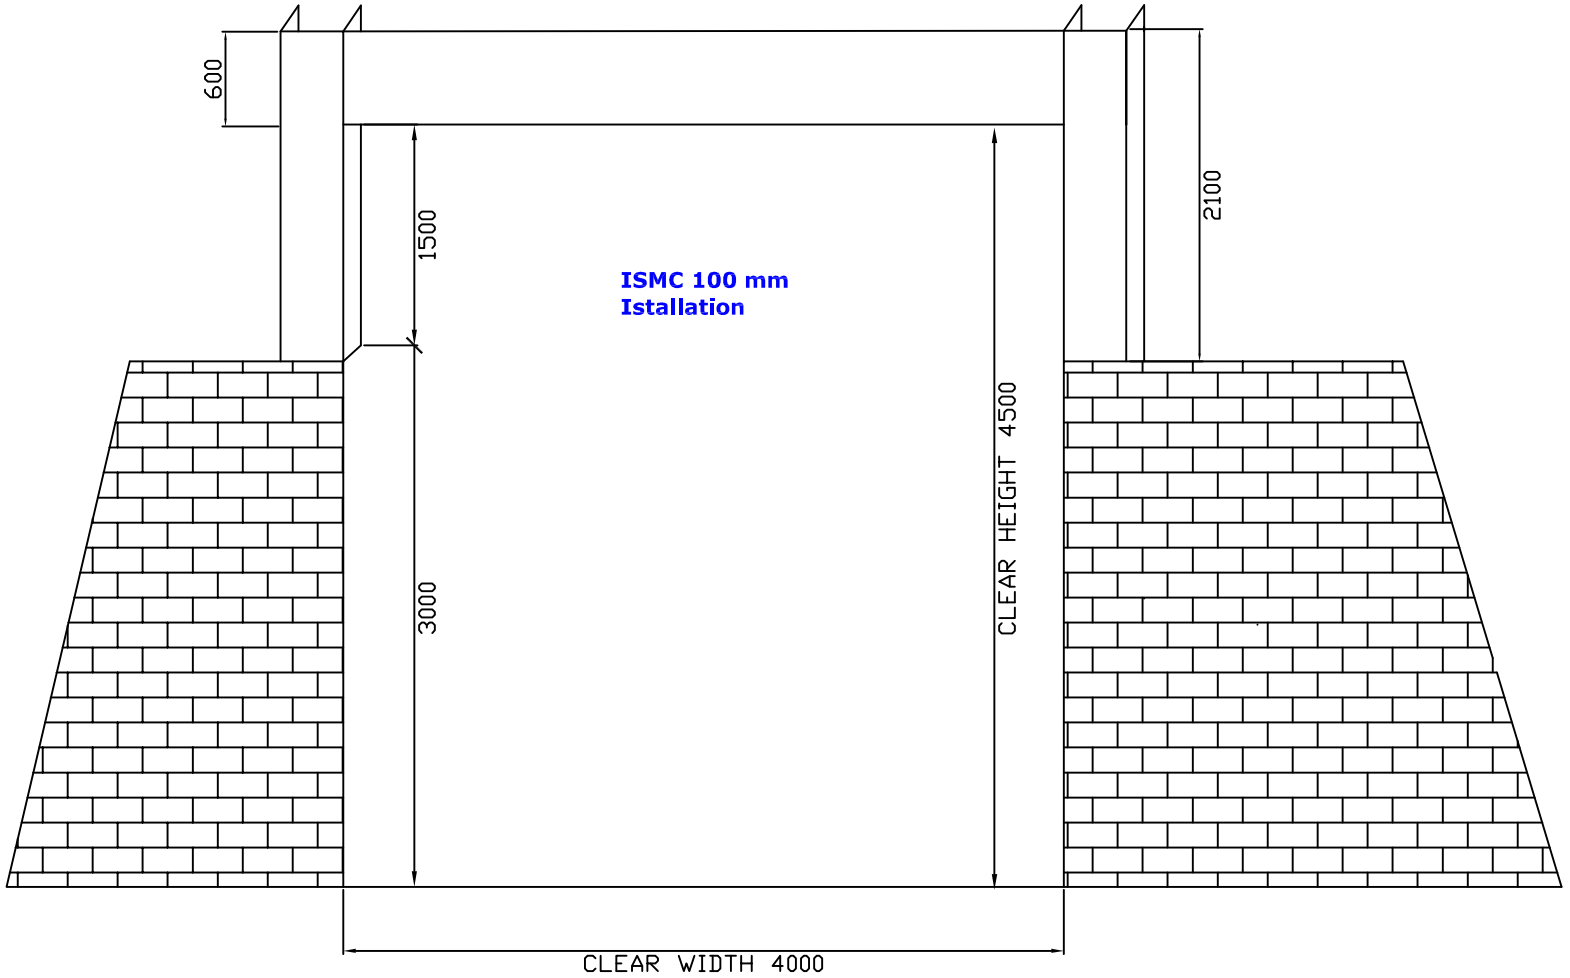


**FRONT VIEW FROM INSIDE BUILDING**

SIZE :- (W)4.0M X (H)4.5M

| | | | |
|---|---|---|---|
| TITLE: MOUNTING STRUCTURE OF FIRE RATED ROLLING SHUTTER | DO NOT SCALE DRAWING | | |
| | | SIGN | DATE |
| CLIENTS APPROVEL:– | DRAWN | ANIL | |
| | CHECK | | |
| | ENG | | |
| | APPRD. | | |
| ALL DIMENSION ARE IN M.M. | PROD | | |
| | MFG | | |
| | Ref. No. | | |

CLIENT:
PROJECT / SITE:
PRODUCT NAME: FIRE RATED ROLLING SHUTTER
DWG. NO.:–
SCALE: NTS
SHEET: 1 OF 1