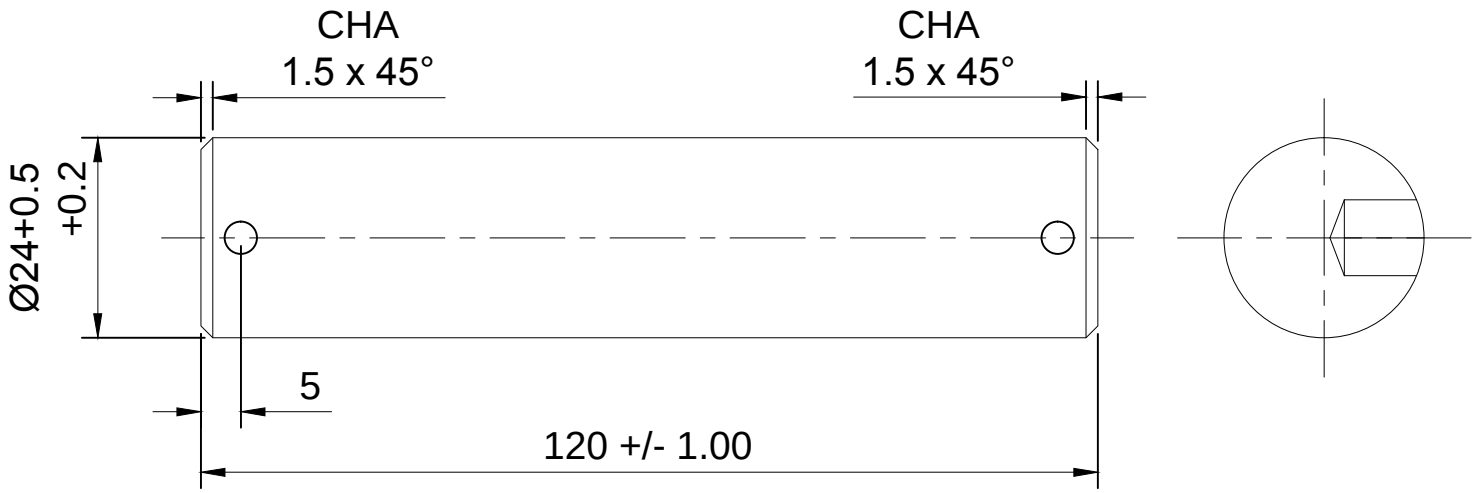


NOTE:~ MTL : EN8

Ø24 X 128L = 3 NOS (HARDENING & GRINDING)

This drawing & design is the property of NIHVA TECHNOLOGIES. Not to be sold or copied to any other concern.

TITLE

DECK CYL TOP & LIP CYL PIN

NIHVA TECHNOLOGIES PVT. LTD.
NIHVA TECHNOLOGIES PVT. PUNE
Tel : 020 66304033
Email:- info@nihva.com
Website:- www.nihva.com

	NAME	SIGN	DATE
DRAWN	PRADEEP		05.09.2018
CHECK	PRADEEP		05.09.2018
APPRD.	PRADEEP		05.09.2018

CLIENT -

PROJECT - DLSD1010

SITE LOCATION -

If any queries contact : design@nihva.com

DWG. NO. : NIHVA/18-19/MFG/DLSD1010/013

ALL DIMENSION ARE IN mm

SCALE: NTS | WT: | REV- 0