

TOP VIEW


INSIDE

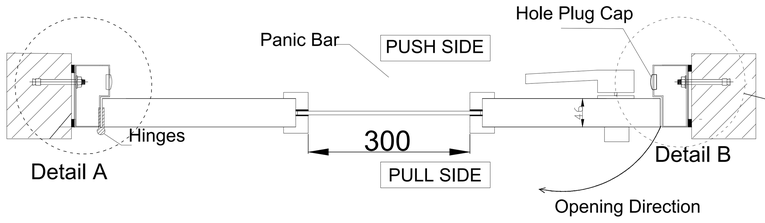

OUT SIDE

SECTION 'X'-'X'

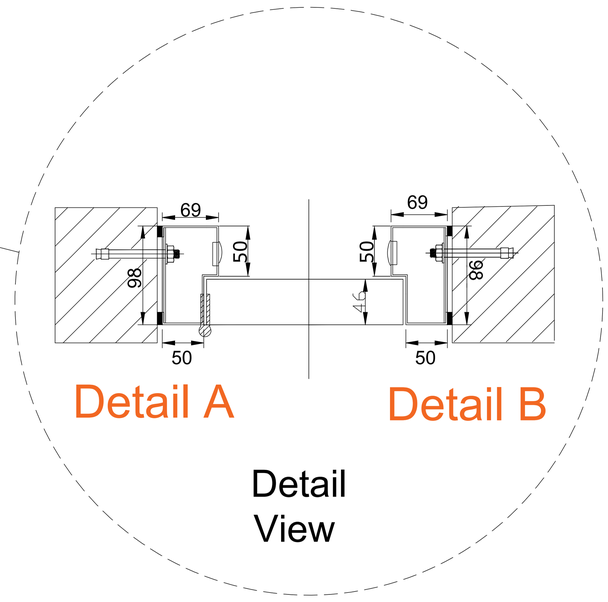

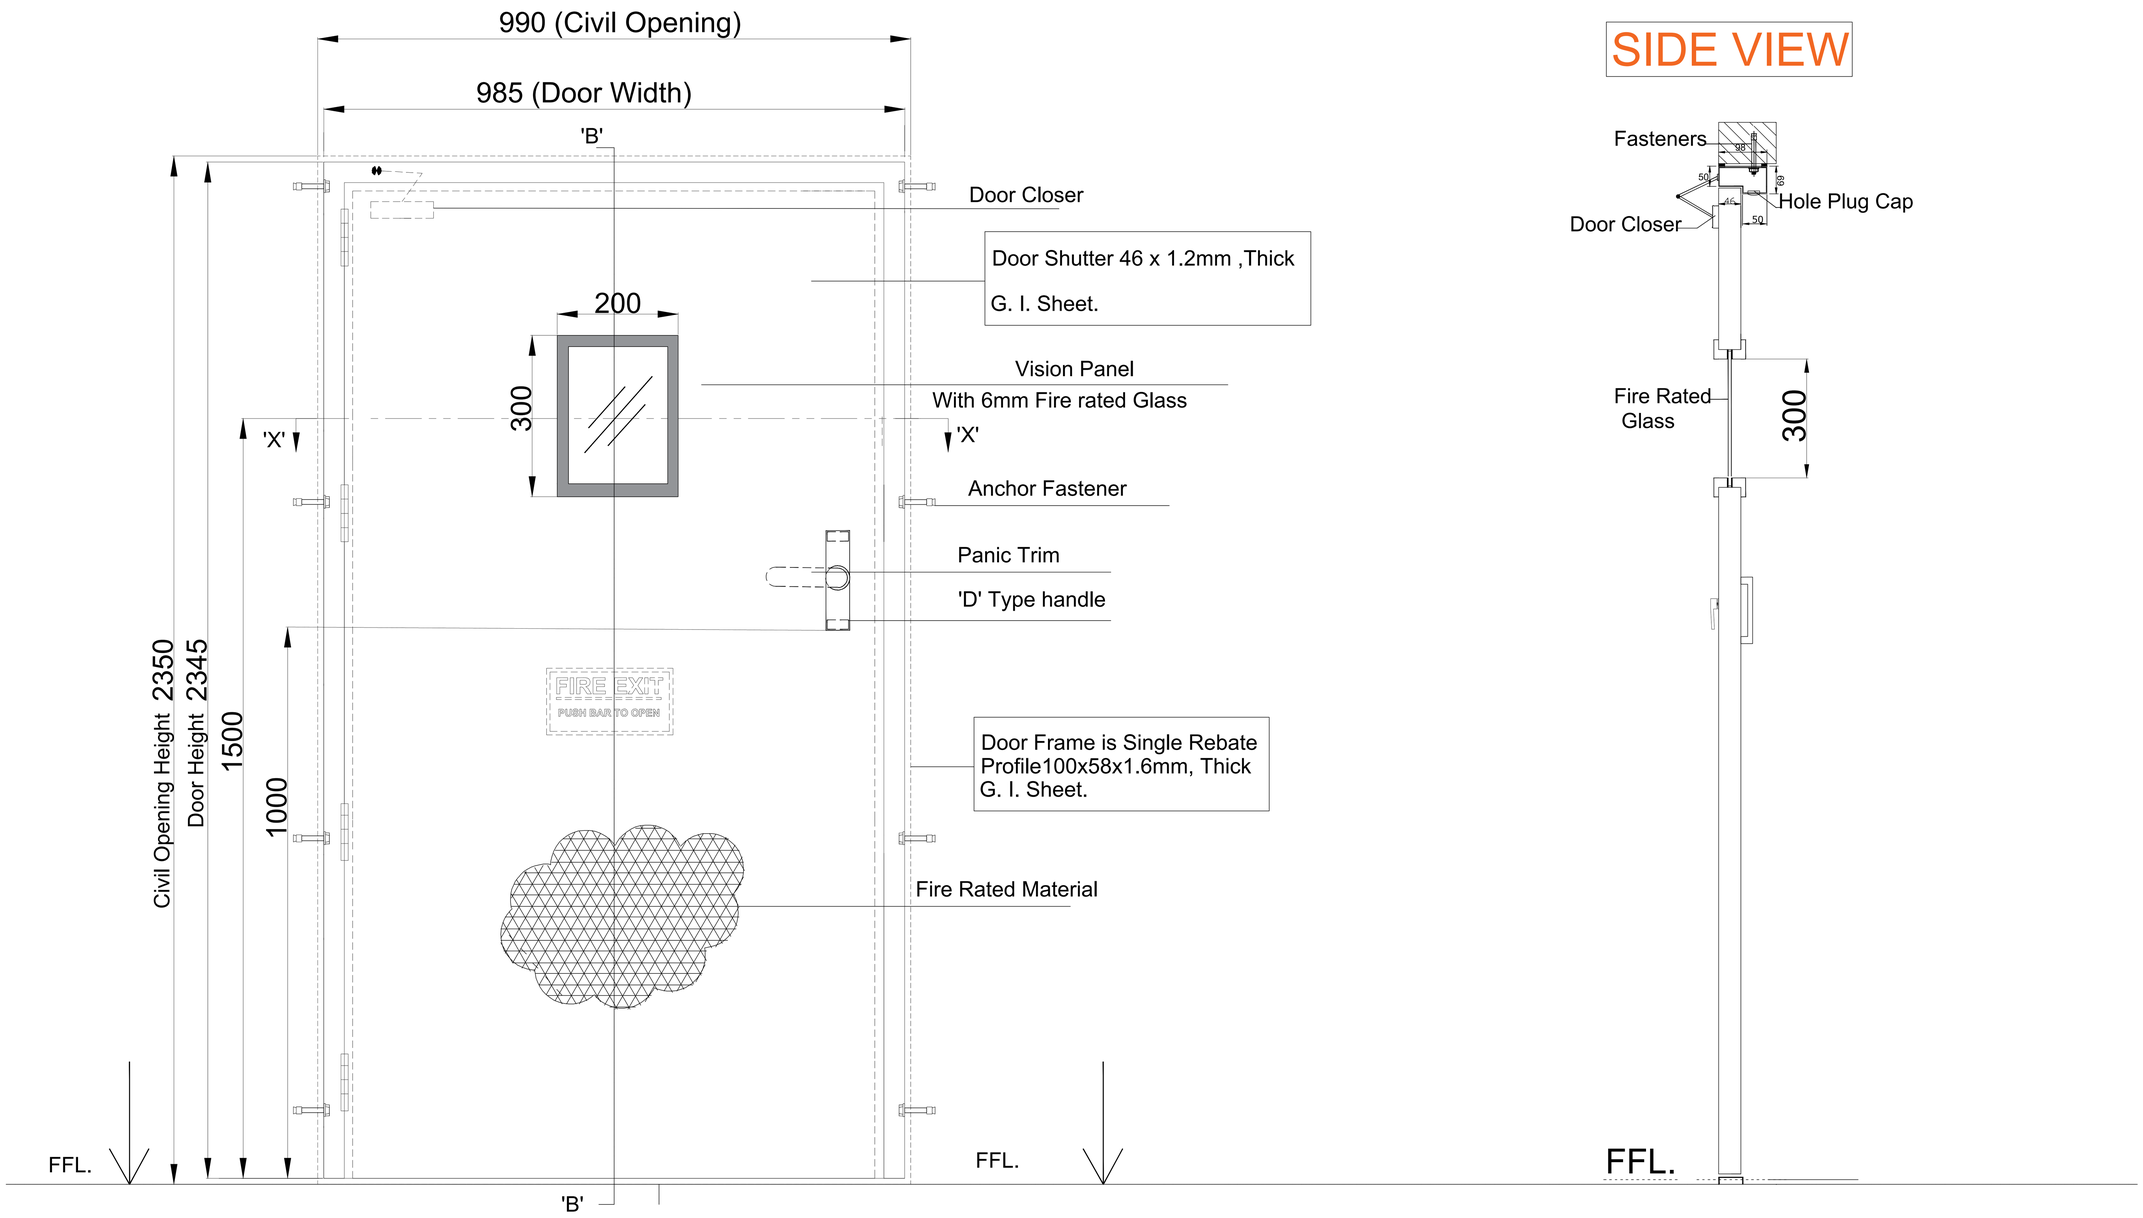

ELEVATION

SIDE VIEW

SECTION B-B

FRONT VIEW

TECHNICAL SPECIFICATION :

Sr.	DESCRIPTION & DETAILS
01	Door frame - 98 X 69 mm x1.6mm thick G.I. Sheet
02	Door Shutter - 46 mm x1.2mm thick G.I. Sheet
03	SS Ball Bearing Hinges 4"x3"x3mm
04	'D' Type handle
05	External Panic Trim
06	Anchor Fasteners (M10x100mm Dia)
07	Heavy Duty Door Closer (TS 1000)
08	Vision Window With 6mm Fire Rated Glass
09	Fire Rating - 120 Minutes
10	RAL Code - 7044

SIZE:

Sr.	Clear Width	Clear Height	Qty
01	990	2350	01

This Drawing & Design is the property of NIHVA TECHNOLOGIES. Not to be sold or copied to any other concern.

TITLE :- FIRE DOOR

NIHVA TECHNOLOGIES PVT. LTD. PUNE
Tel : 020 66304033
Email : info@nihva.com
Website : www.nihva.com

NAME	DATE	SIGN
S.J	20/09/2024	
B.B	21/09/2024	
V.T	21/09/2024	

CLIENT -

LOCATION -

PRODUCT - FIRE DOOR | QTY-01 Nos

If any queries contact : design2@nihva.com

DWG NO - NIHVA/24-25/HVT/2409001 | REV- 0

All dimensions are in MM

SCALE : NTS | SHEET : 01 OF 01