
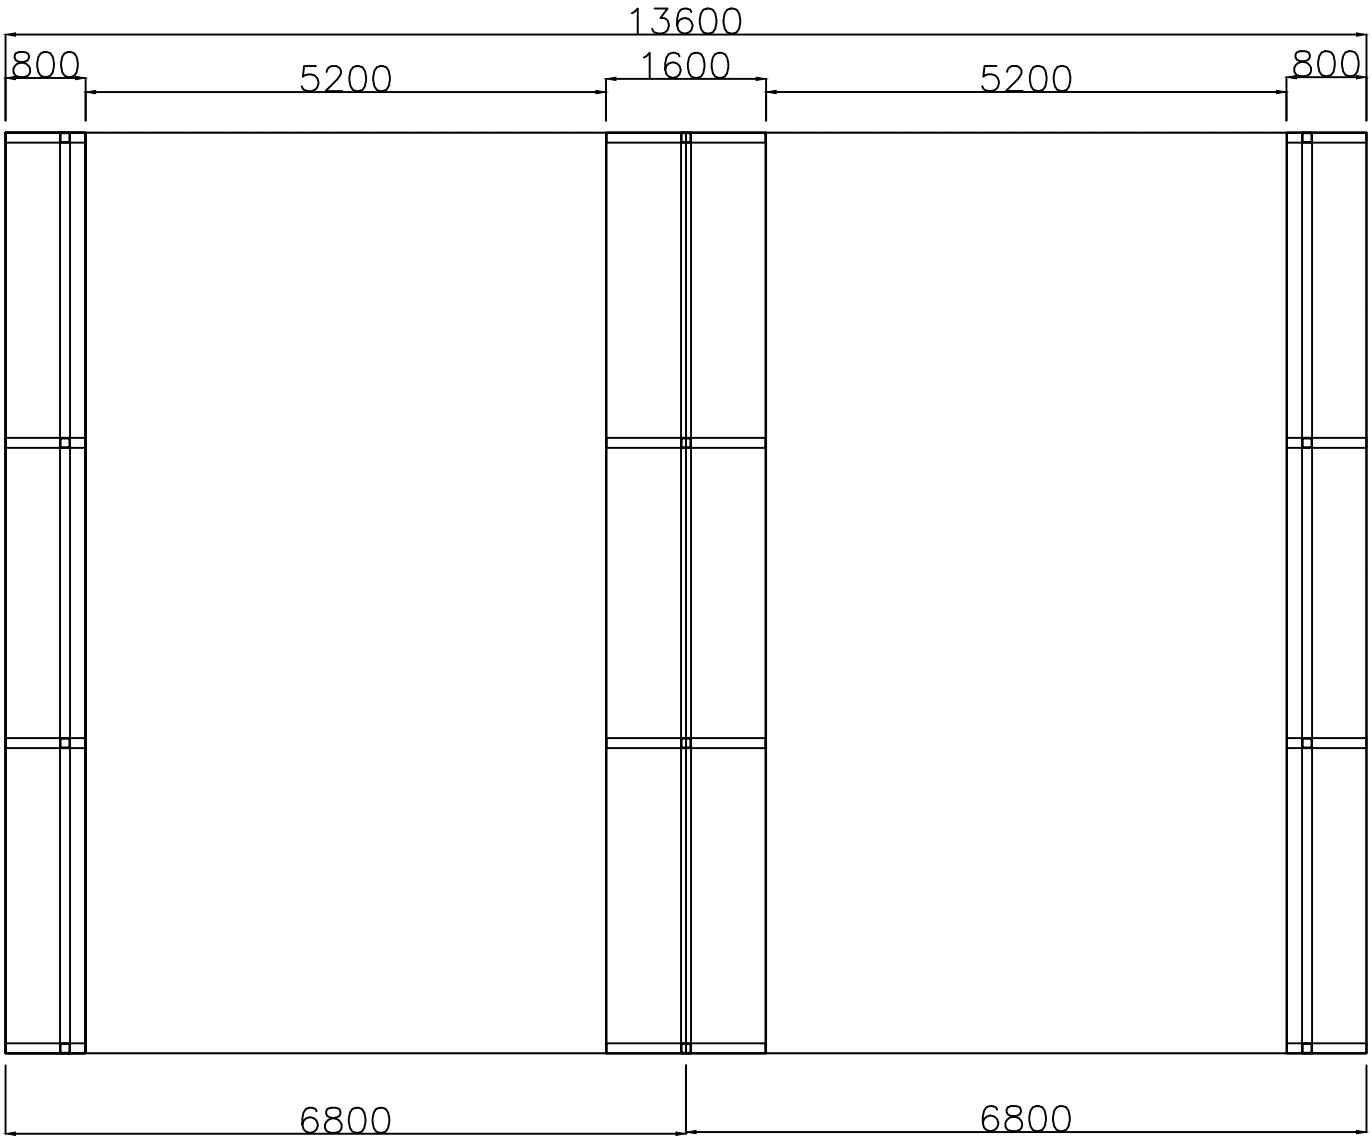


STRUCTURAL PLAN

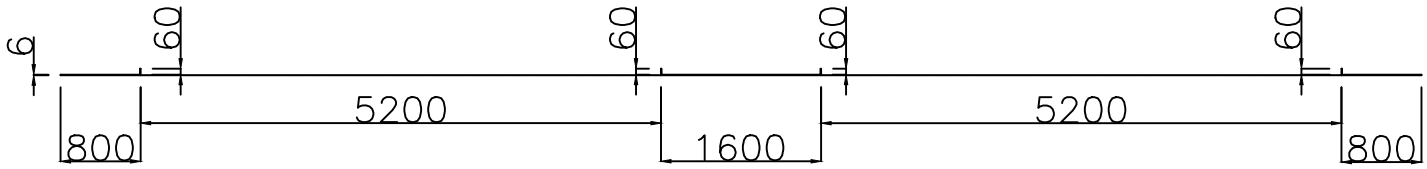

SECTION VIEW

1. THE DRAWING IS ONLY FOR REFERENCE, THE FINAL DRAWING WILL BE SHARED AFTER ORDER CONFIRMATION.
2. ALL STRUCTURAL WORK IS IN CLIENT SCOPE.
3. GRADIENT OF 50MM NEED TO BE PROVIDED ALONG THE OUTER LENGTH TO AVOID WATER STAGNANCY IN GUIDE RAIL.
4. AL PROFILE - POWDER COATED 60X63 MM
5. GASKET - EPDM
6. MOTOR - ITALIAN/GERMAN MAKE
7. ELECTRICAL REQUIREMENT - 220V 5AMP SINGLE PHASE CONNECTION.
8. ALL DIMENSION IN MM.