


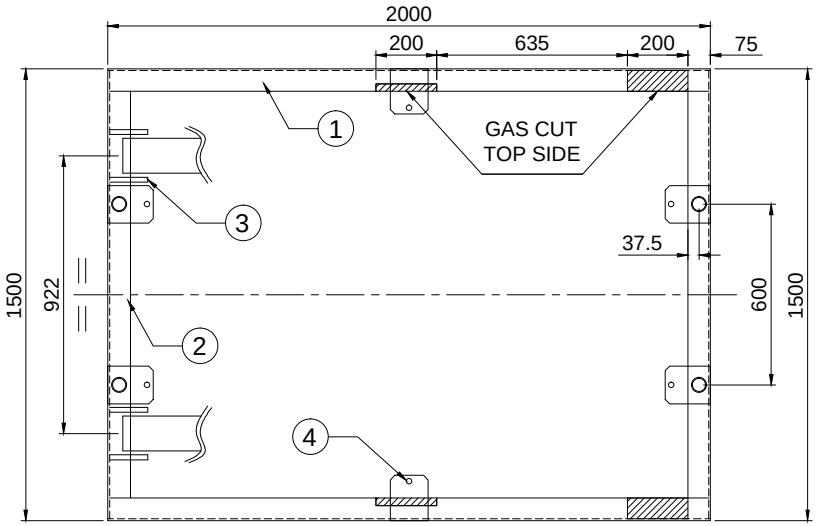


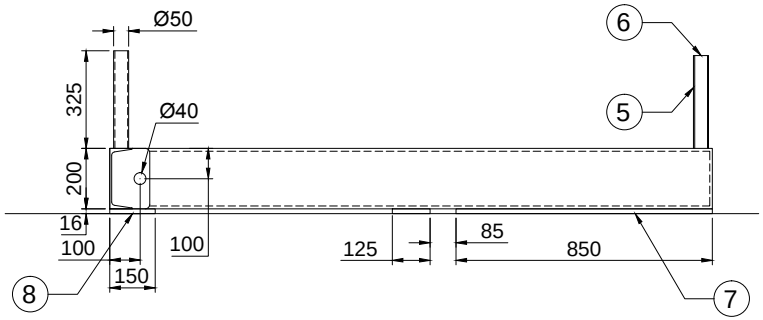

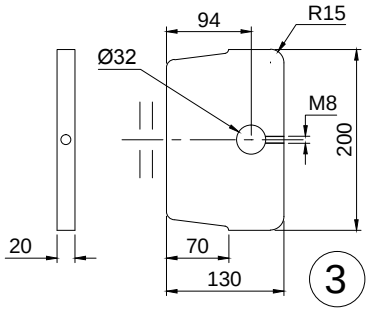

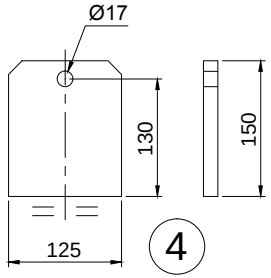

SR NO	PART NAME	SPECIFICATION	QTY
1	ISMC	200 X 75 X 2000L	2 NOS
2	ISMC	200 X 75 X 1488L	2 NOS
3	LASER PRO.	200 X 20 THK X 130L	4 NOS
4	FLAT	125 X 16 X 150L	6 NOS
5	ERW PIPE	OD48 X 3.25 THK X 325L	4 NOS
6	NYLON ROD	Ø50 X 10THK	4 NOS
7	FLAT	75 X 16 X 850L	2 NOS
8	FLAT	75 X 16 X 150L	2 NOS

This drawing & design is the property of NIHVA TECHNOLOGIES. Not to be sold or copied to any other concern.

TITLE : - BASE FRAME

	SIGN	DATE
DRAWN	P.A	10.01.19
CHECK	R.D	10.01.19
REV.		
APPROVAL		

If any queries contact : projects@nihva.com

ALL DIMENSION ARE IN mm

NIHVA TECHNOLOGIES PVT. LTD. PUNE
Tel : 020 66304033
Email:- info@nihva.com
Website:- www.nihva.com

CLIENT -

PROJECT -

SITE -

DWG. NO. : NIHVA/18-19//MFG/NSCL327/01

SCALE: NTS | WT: | SHEET: 01 OF 01