
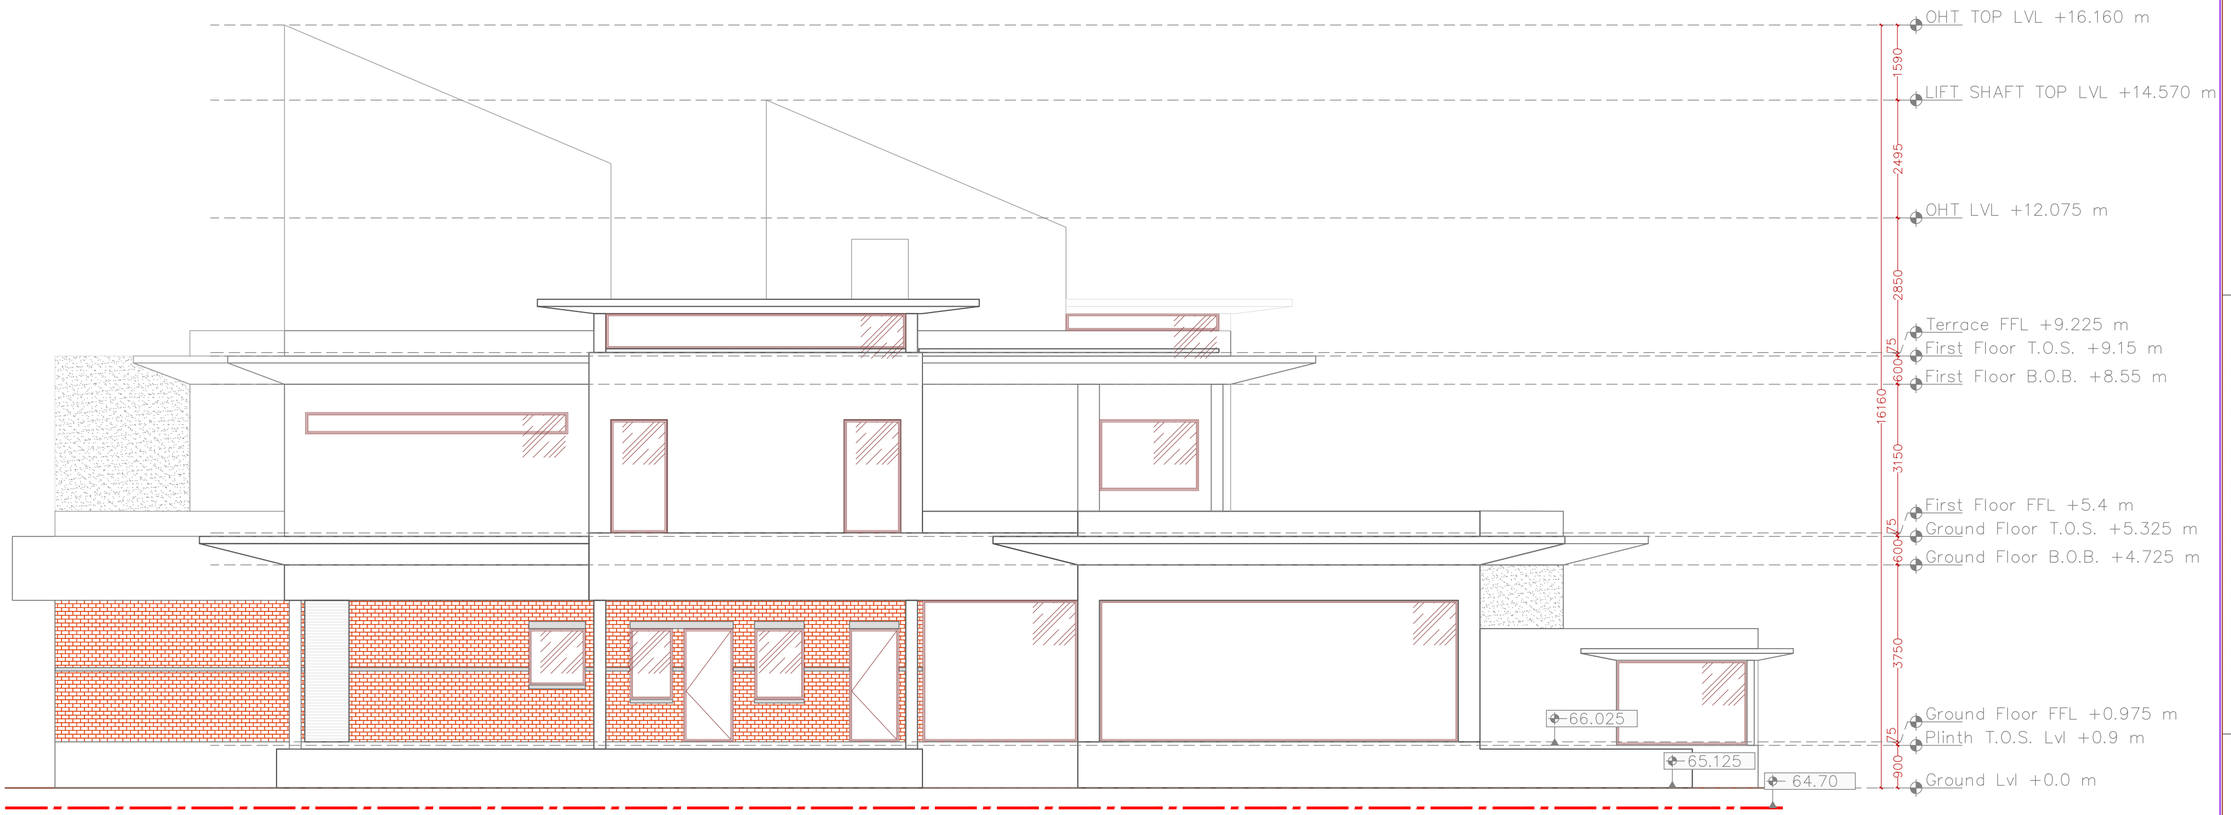


ELEVATION A

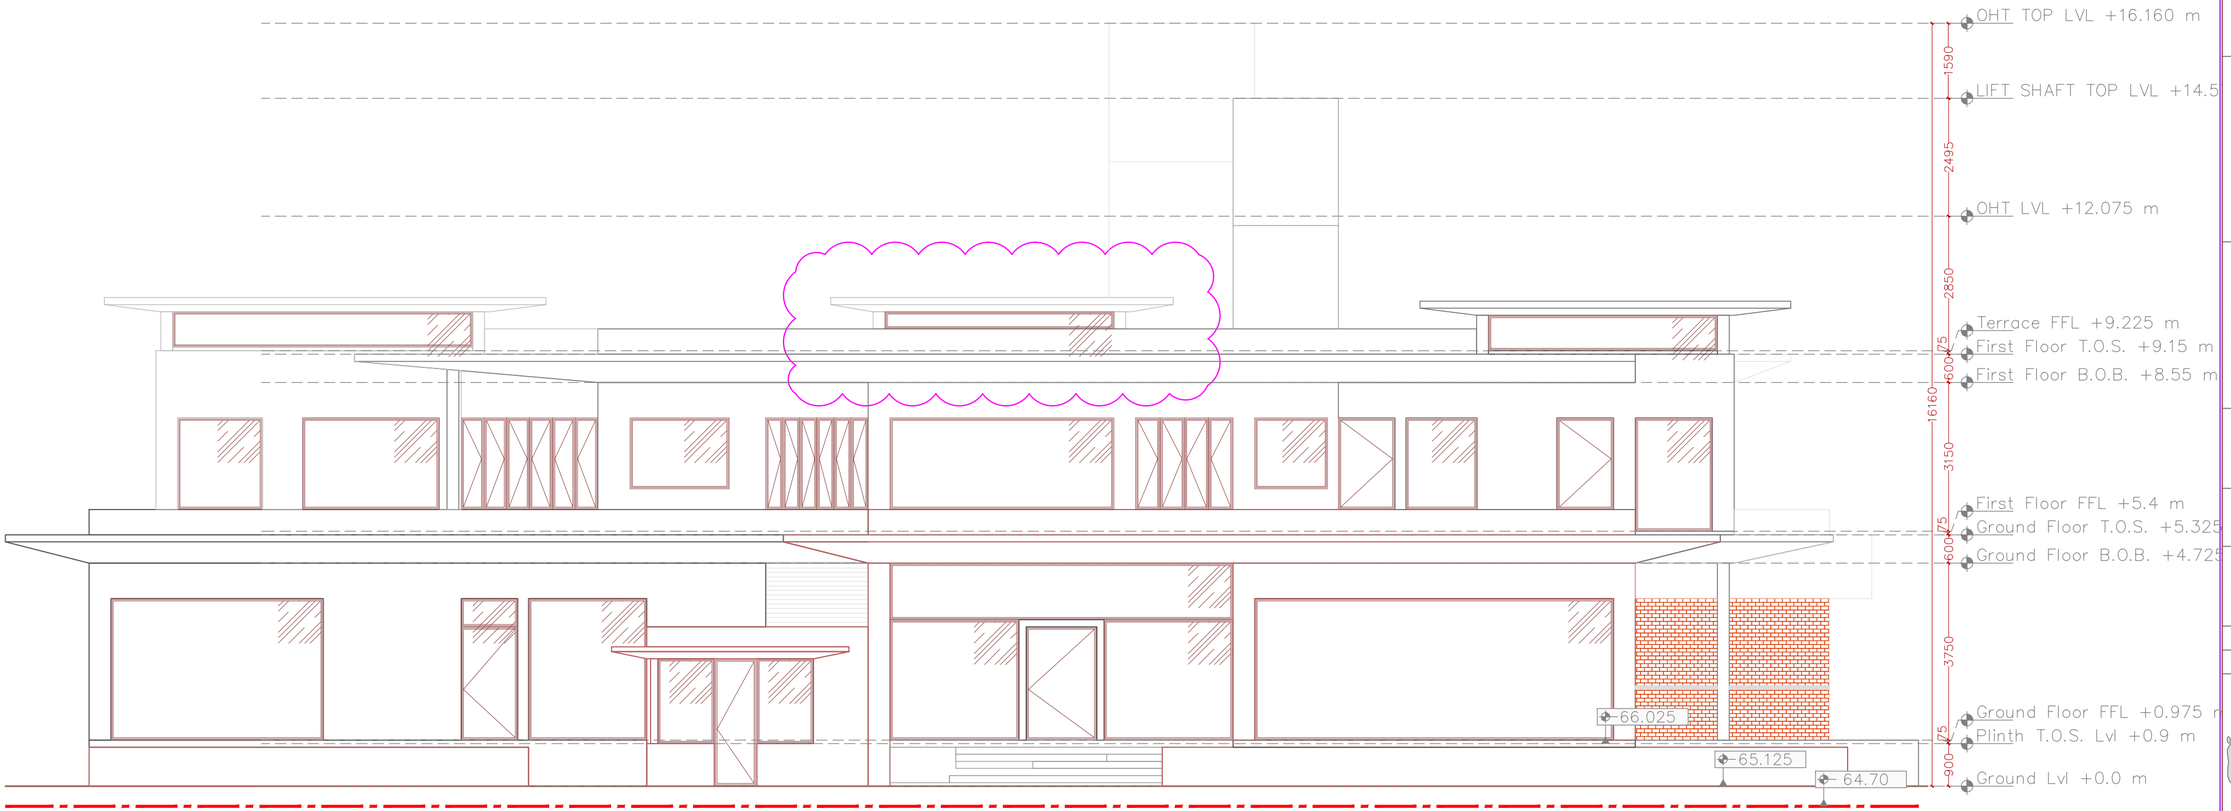

ELEVATION B

KEY PLAN

NOTES

All dimensions are in millimeters. All dimensions refer to unfinished surfaces unless specified otherwise. All dimensions should be read and not measured.

Refer structural drawings for all concrete work and details below plinth.

Refer detail drawings wherever relevant.

Drawings are cross referenced and are to be read in conjunction with other drawings as indicated.

0000 level for each building is set with reference to benchmark established on site. All other levels are with reference to the 0000 level. All levels are indicated in millimeters.

In case of any discrepancy between architectural drawings and other drawings, architectural drawings to be followed.The discrepancy to be brought to the notice of the architect before commencement of the work.

SIGN & STAMP

LEGEND AND ABBREVIATIONS

CONSULTANTS

STRUCTURAL CONSLT.– SETU INFRASTRUCTURE
ELECTRICAL CONSLT.– AMBA CONSTRUCTION
PLUMBING CONSLT.– UTILITY DESIGN STUDIO
HVAC– J.J. KARIA HVAC CONSLT.
LANDSCAPE–
PMC– SANJAY SONEKAR

PROJECT

NEW APTA SANKUL RESIDENCE
ADALAJ

CLIENT

SHREE SIMANDAR SWAMI ARADHANA TRUS

DRAWING

Elevations
Vatsalya– Working Drawing

DATE: 03–10–202 DRG. NO.: V–AR–E–006–0–R4

DRAWN BY– Krupen

ARCHITECTS

Yatin Pandya
FOOTPRINTS E.A.R.T.H.
Environment Architecture Research Technology Housing
Milan bungalow, sargam flat lane,
Ishwar Bhuvan to Staduim road, Navarngpura.
Ahmedabad: 380014
Phone no: +91 9825005049
E-mail: footprintsearthoffice@gmail.com

This drawing and the design it covers is the property of FOOTPRINTS E.A.R.T.H., Ahmedabad, India. It is merely loaned on the borrower's express agreement that it will not be reproduced, copied, loaned, exhibited nor used except in a limited way and private use as permitted by any written consent given by the lender to th