



PLAN

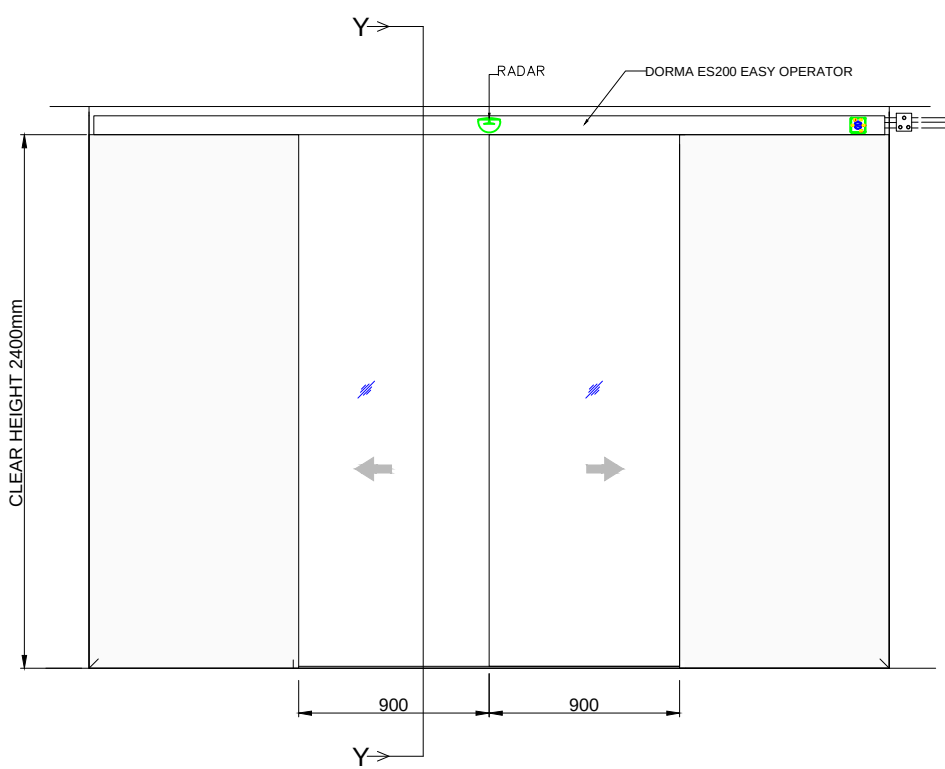

ELEVATION@INSIDE

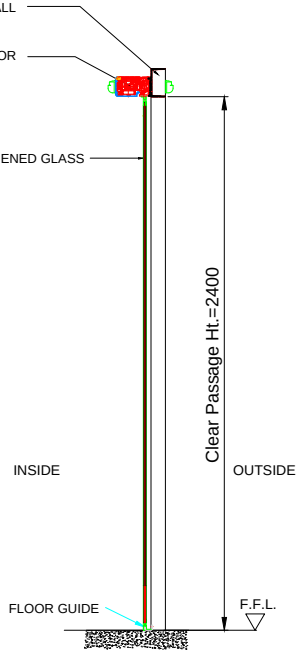

SECTION Y-Y

DIMENSION		
CLEAR WIDTH	CLEAR HEIGHT	QUANTITY
1800 mm	2400 mm	1 NOS.

MATERIAL :

THICKNESS :

CLIENT'S COMMENTS :

NIHVA TECHNOLOGIES PVT. LTD.
NIHVA TECHNOLOGY PVT. LTD. PUNE
Email:- info@nihva.com
Website:- www.nihva.com

TITLE:

AUTOMATIC SLIDING GLASS DOOR

CLIENT'S APPROVAL :

CLIENT - SVN ASSOCIATES

PROJECT - VIJAY LOGISTICS

SITE LOCATION - CHAKAN

DWG. NO. : NIHVA/16-17/0039

SCALE: NTS	WT:	SHEET:1 OF 1
DRAWN BY: OMKAR		DATE: 26-09-2016
CHECK : ANIL		DATE: 26-09-2016

If any queries contact : projects@nihva.com

NOTE: ALL DIMENSION ARE IN mm

THIS DRAWING & DESIGNING IS THE PROPERTY OF NIHVA TECHNOLOGIES. NOT BE SOLD OR COPY TO ANY OTHER CONCERN.