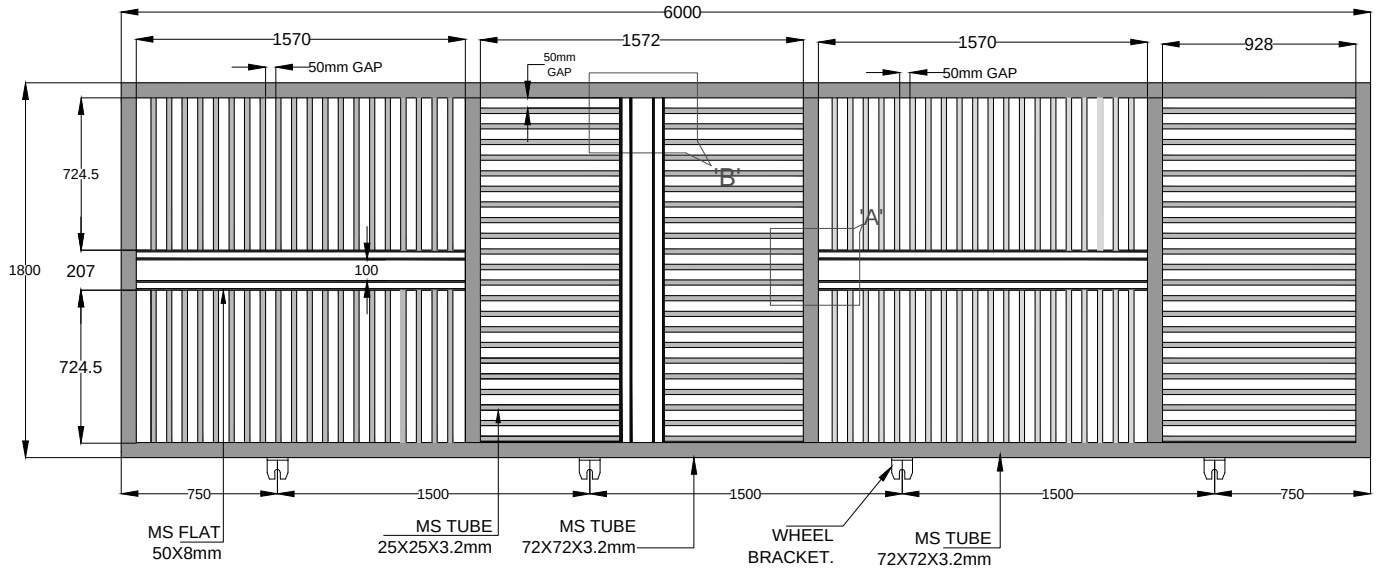

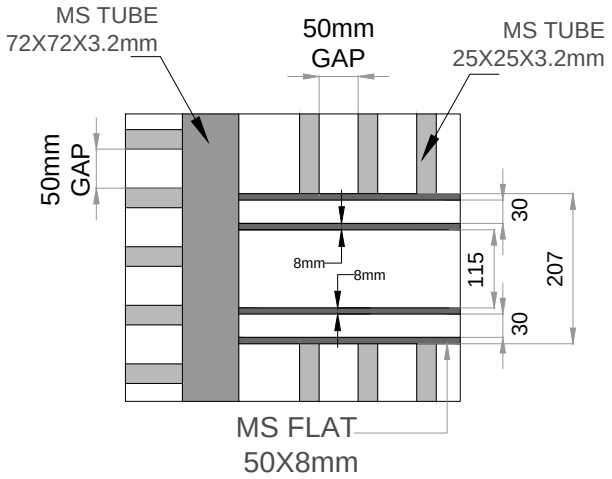

DETAIL VIEW OF 'A'.

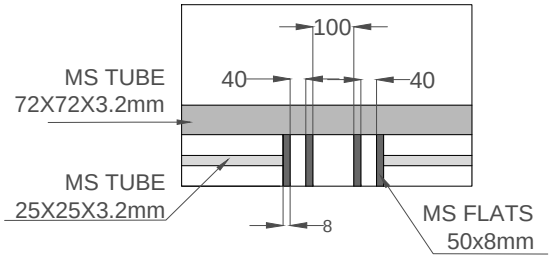

DETAIL VIEW 'B'

NOTE:-WHEEL BRACKET PROFILE ONLY LASER CUTTING.

REV04(18-04-2018):-A).LENGTH OF PATTERN IS REVISED.
REV03(13-04-2018):-A).GATE HEIGHT CHANGED.
REV02:-A).GATE HEIGHT CHANGED.
B).PATTEREN SIZE CHANGED.
REV01:-A).IN INTERMEDIATE PORTIONS FLATS REPLACED WITH TUBE.

SR NO	CLEAR WIDTH	CLEAR HEIGHT	QTY.
1	6000mm	1800mm	01 NOS

This drawing & design is the property of NIHVA TECHNOLOGIES. Not to be sold or copied to any other concern.

TITLE: SLIDING GATE LEAF 02

NIHVA TECHNOLOGIES PVT. LTD.

NIHVA TECHNOLOGIES PVT. LTD. PUNE
Tel : 020 66304033
Email:- info@nihva.com
Website:- www.nihva.com

	NAME	SIGN	DATE
DRAWN	SURAJ		03-04-2018
CHECK	OMKAR		03-04-2018
APPRD.	SHEKHAR		03-04-2018

CLIENT -
PROJECT -
SITE LOCATION -
If any queries contact : design@nihva.com
DWG. NO. : NIHVA/17-18/VDR/0269/R04.
REV- 04.
ALL DIMENSION ARE IN mm
SCALE: NTS
WT:
SHEET: 01 OF 01