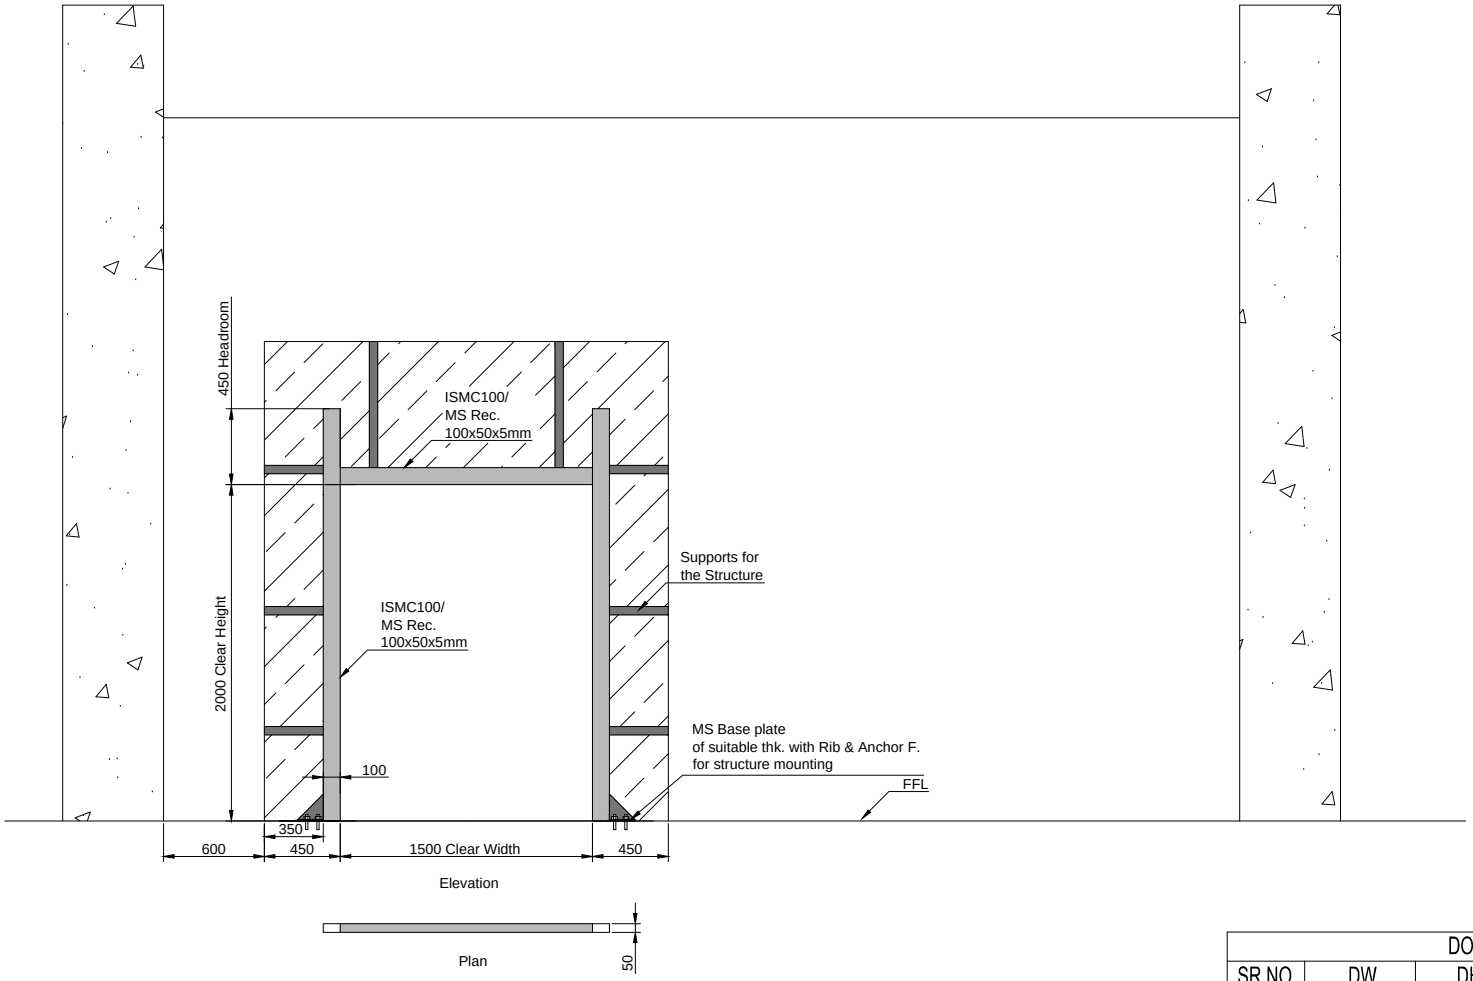

DOOR DIMENSION				
SR NO	DW	DH	MOTOR LOCATION	QUANTITY
1	1500	2000	RIGHT HAND SIDE	2

This drawing & designing is the property of NIHVA TECHNOLOGIES. Not to be sold or copied to any other concern.

TITLE: STRUCTURE FOR HSD HS9020G

NIHVA TECHNOLOGIES PVT. LTD.
NIHVA TECHNOLOGIES PVT. LTD. PUNE
Tel : 020 66304033
Email:- info@nihva.com
Website:- www.nihva.com

	NAME	SIGN	DATE
DRAWN	OMKAR		11/05/18
CHECK	PRADEEP		11/05/18
APPROVAL	PRADEEP		11/05/18

If any queries contact : design@nihva.com

ALL DIMENSION ARE IN mm

CLIENT - Fibro,India

PROJECT -

SITE - Chakan

DWG. NO. : NIHVA/17-18/0037 | REV- 0

SCALE: NTS | WT: | SHEET: 01 OF 01

Note-
1. All Civil work will be in clients scope.