

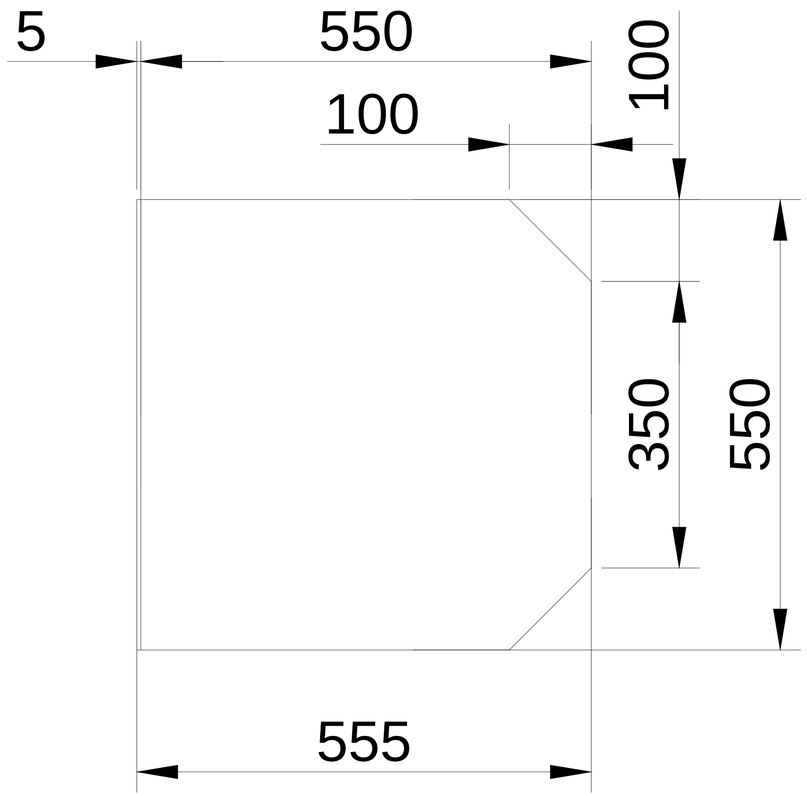


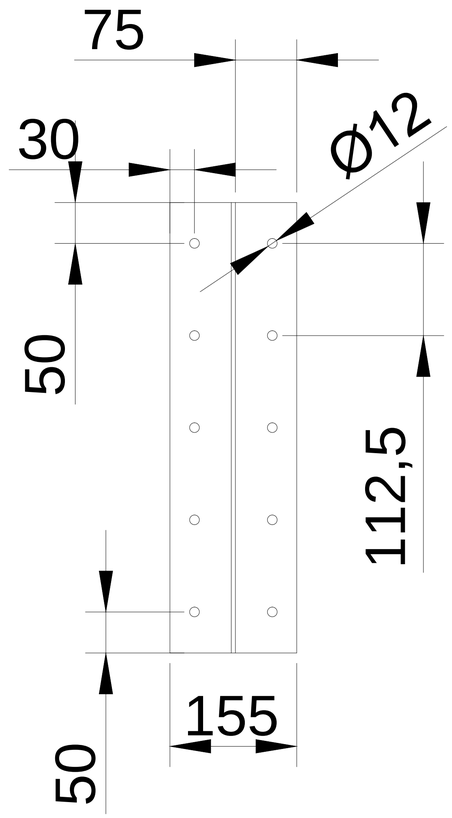

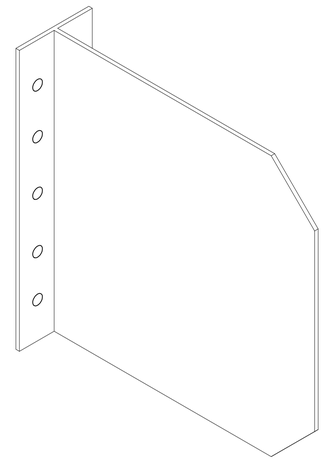

MATERIAL- MS
THICKNESS- 5mm
QUANTITY- 16 NOS

This drawing & design is the property of NIHVA TECHNOLOGIES. Not to be sold or copied to any other concern.

TITLE	MS BRACKET		NIHVA TECHNOLOGIES PVT. LTD. PUNE Tel : 020 66304033 Email:- info@nihva.com Website:- www.nihva.com
	SIGN	DATE	
DRAWN	GIP	14/12/21	CLIENT -
CHECK	AK	14/12/21	PROJECT -
REV.			SITE -
APPROVAL			DWG. NO. : NIHVA/21-22/MFG/010
If any queries contact : projects@nihva.com			SCALE: NTS | WT: | SHEET: 01 OF 01
ALL DIMENSION ARE IN mm			