
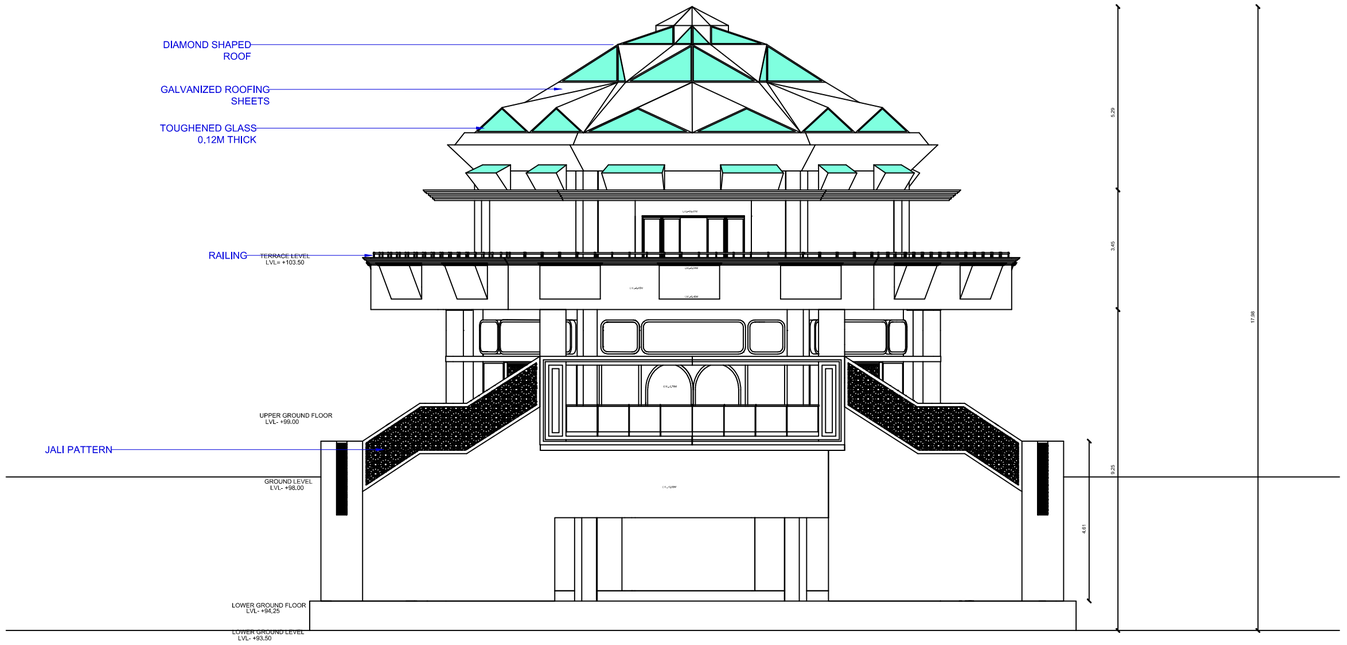


BACK ELEVATION

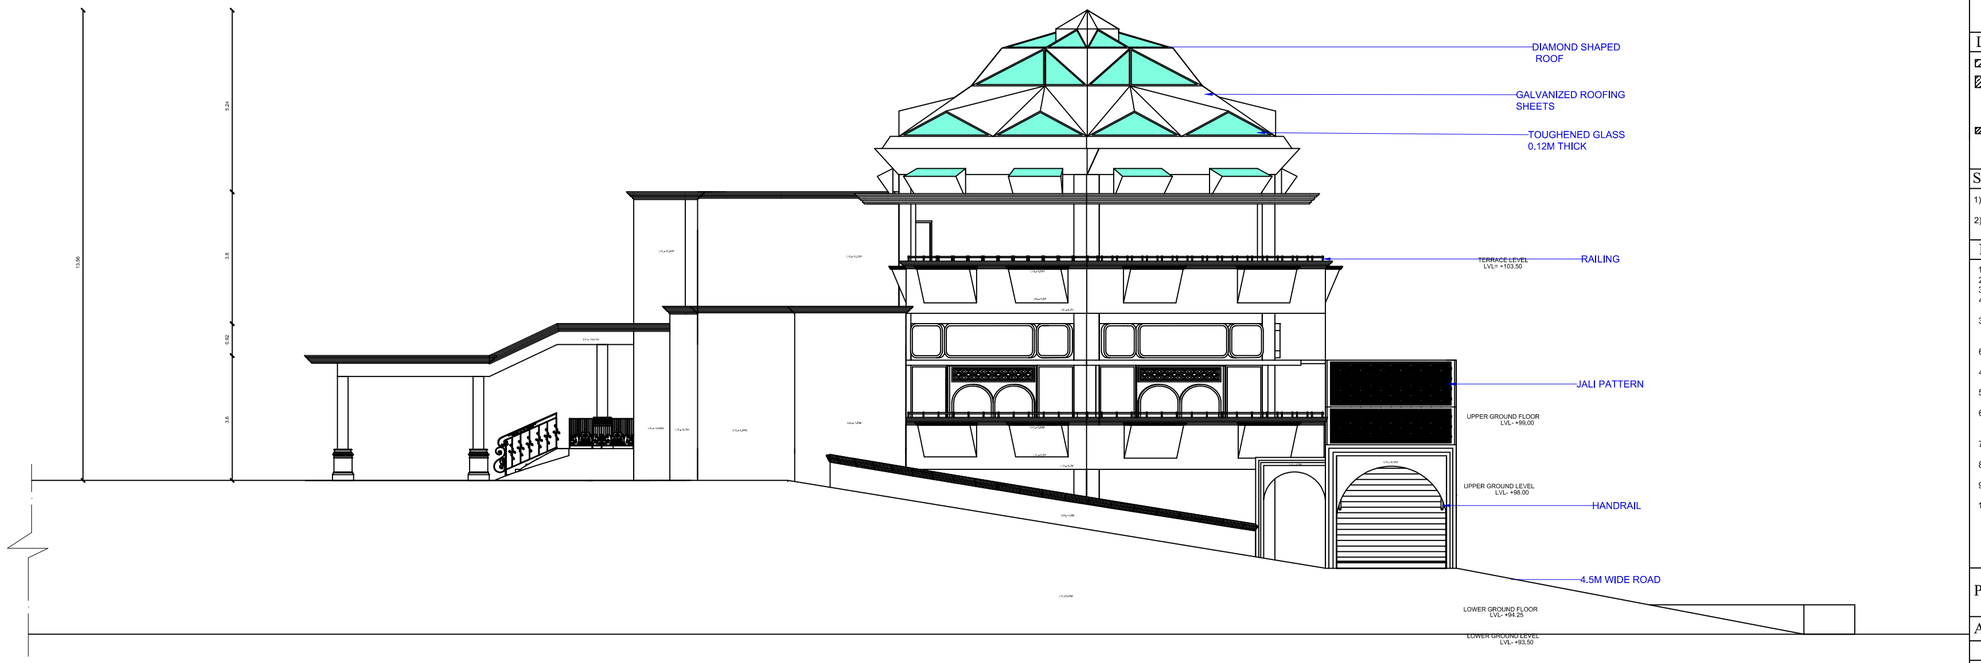

RIGHT ELEVATION

ADVANCE COPY | W / DRG. NO. 01

DRAWING-

ELEVATIONS

LEGENDS

- 150MM THK. BRICK WALL
- 230MM THK. BRICK WALL
- 100MM THK. BRICK WALL WITH 1050MM HT. IN UTILITY AREA
- 125MM THK. BRICK WALL

SPECIFICATIONS

1) REFER DETAIL DRAWING FOR TOILET AND SCHEDULE OF OPENING DOORS, WINDOWS
2) ALL EXTERNAL & INTERNAL WALL THICKNESS :150MM

NOTES

1) DO NOT SCALE THE DRAWING.
2) ONLY WRITTEN DIMENSIONS TO BE FOLLOWED.
3) ALL DIMENSIONS ARE IN METER.
4) DRAWING SHALL BE READ IN CONJUNCTION WITH STRUCTURAL DRAWING & MUNICIPAL DWG.
3) ALL STRUCTURAL SIZES & STRUCTURAL DETAIL TO BE REFERED FROM DRAWINGS OF STRUCTURAL CONSULTANTS.
6) REFER STRUCTURAL DRAWING FOR RCC/ STEEL TRUSS OR RESPONSIBILITY GOES TO OWNER ONLY.
4) DO NOT ASSUME IN CASE OF DISCRIPANCY REFER ARCHITECT.
5) DRAWING NOT TO BE SCALED, ONLY WRITTEN DIMENSIONS TO BE FOLLOWED.
6) ANY DISCREPANCIES IN THIS DRAWING SHALL BE BROUGHT TO THE NOTICE OF THE ARCHITECT BEFORE EXECUTION.
7) ALL CENTER LINE DIMENSIONS WITH REFERENCE TO (O,0)
8) CONTRACTOR TO STUDY DRAWING AND REVERT BACK IN CASE OF ANY DISCREPANCIES.
9) FIGURE SHOWS FIXED FACE OF COLUMN

10) COPY RIGHT AND PROPERTY OF THIS DRAWING BELONGS TO THE ARCHITECT, IT MUST NOT BE COPIED NOR MADE KNOWN TO THIRD PARTY WITHOUT THEIR WRITTEN CONSENT.

PROJECT : KHORI PARK

ARCHITECT : SHASHANK JOSHI

PROJECT CONSULTANT

DESIGNERS GROUP
ARCHITECTS & INTERIOR.
LANDSCAPE DESIGNERS
FLAT NO 07,PUSHPA APARTMENT, NEAR UNION BANK, VANAZ CORNER, POUD ROAD, KOTHRUD, PUNE-38

REV.DATE	REV.NO.	REASON	REV.BY	NORTH	REV.NO.	DEALT BY	
	R0	PRELIMINARY WORKING DRG	YASH	N	R0	DATE	
						JOB NO.	
						SCALE	

DRAWING NO.
WD/07/KHORI PARK
ELEVATIONS

THIS DRAWING IS THE SOLE PROPERTY OF DESIGNERS GROUP, IT'S USE FOR ANY PURPOSE OTHER THAN THAT MENTIONED IS TO BE DONE ONLY AFTER PRIOR APPROVAL.