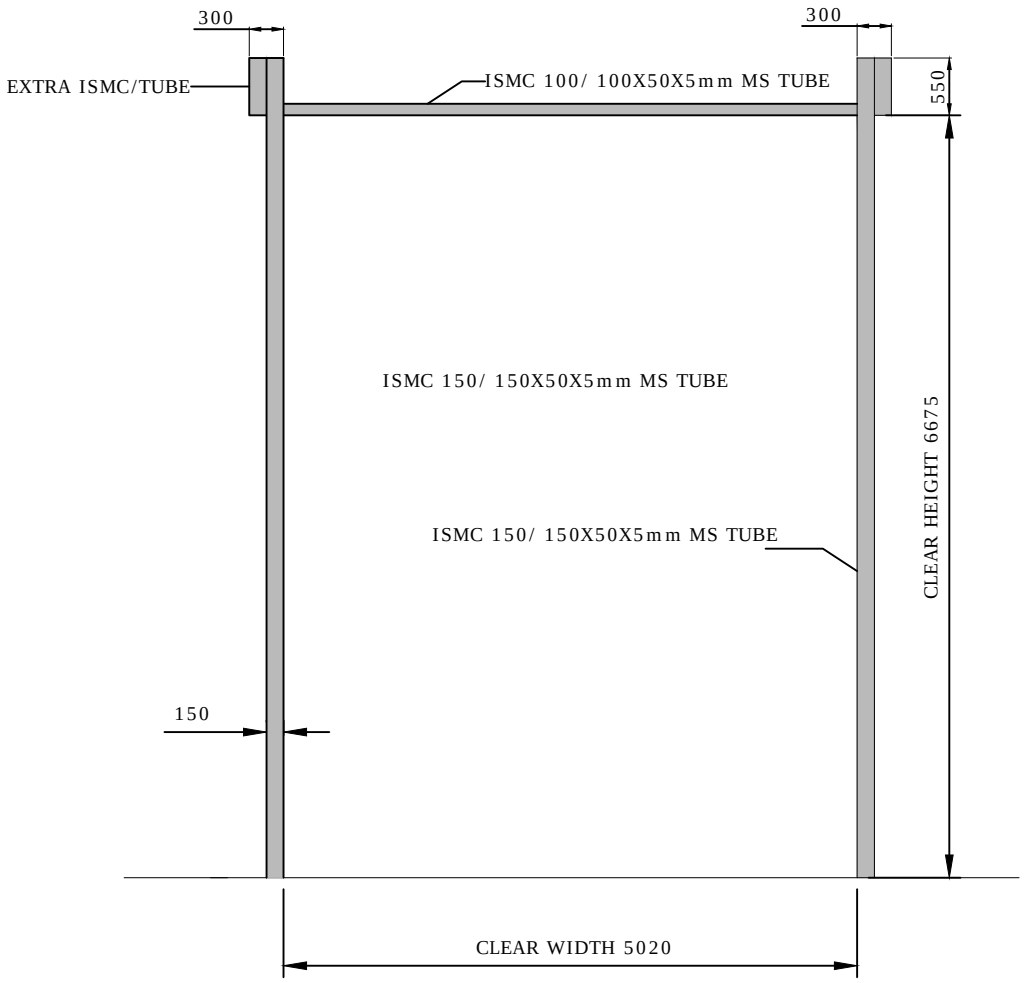

CLEAR WIDTH	CLEAR HEIGHT	QUANTITY
5020	6675	02

NOTE-
1. IF RCC LINTEL FOR MS BRACKET & WALL FOR MS GUIDE IS AVAILABLE AT SITE THEN NO NEED OF MS STRUCTURE.
2. REQUIRED STRUCTURE FOR ROLLING SHUTTER WILL BE CLIENT'S SCOPE.

This drawing & designing is the property of NIHVA TECHNOLOGIES. Not to be sold or copied to any other concern.

TITLE	STRUCTURE FOR ROLLING SHUTTER		NIHVA TECHNOLOGIES PVT. LTD. PUNE Tel : 020 66304033 Email:- info@nihva.com Website:- www.nihva.com
	SIGN	DATE	
DRAWN	SURAJ	24/08/17	CLIENT - SHILCHAR TECHNOLOGIES LTD.
CHECK	SHEKHAR	24/08/17	PROJECT -
REV.	00		SITE - VADODARA
APPROVAL			DWG. NO. : NIHVA/17-18/0179
If any queries contact : projects@nihva.com			SCALE: NTS / WT: / SHEET: 01 OF 01
ALL DIMENSION ARE IN mm			