



ELEVATION

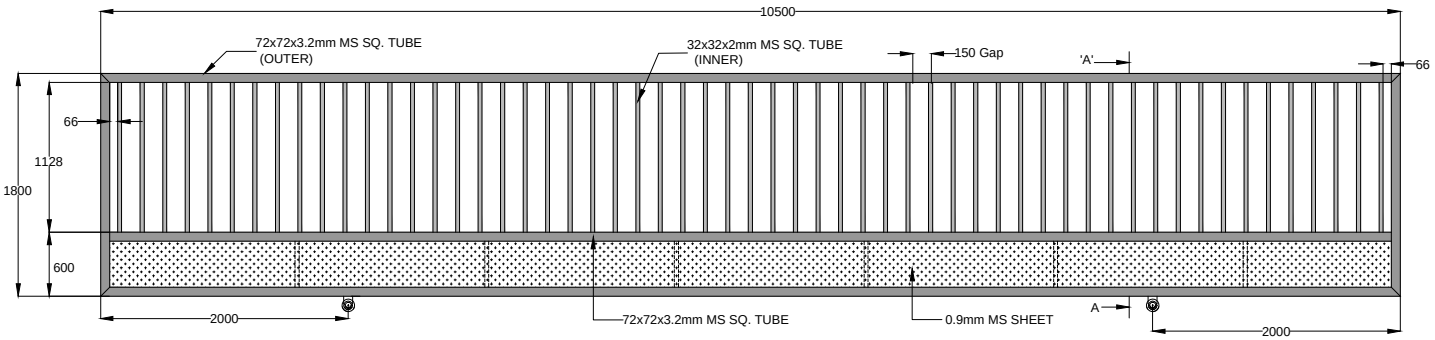

SIDE VIEW

DETAIL A-'A'

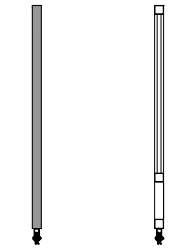

PLAN

SR NO	TUBE SPECIFICATION		MATERIAL	SIZE
1	72X72X3.2mm MS TUBE	OUTER FRAME	MILD STEEL	10.5 MTR- 03 NOS 1.8 MTR - 02 NOS
2	32X32X2mm MS TUBE	INNER PATTERN	MILD STEEL	1.128MTR- 57 NOS 0.456MTR- 18 NOS
3	150mm	GAP BETWEEN TUBES	-	-
4	0.9mm THK	MS SHEET	MILD STEEL	1150X456X0.9- 8 NOS 1156X456X0.9- 1 NOS

TOLERANCE:- ± 10mm

CLEAR WIDTH (CW)	CLEAR HEIGHT (CH)	QUANTITY
10500mm	1800mm	1 NOS

DIMENSION :

CLEAR WIDTH	CLEAR HEIGHT	QUANTITY
10500mm	1800mm	1 NOS

MATERIAL: MS

THICKNESS :

NOTE-
1. ALL REQUIRED CIVIL WORK WILL BE IN CLIENTS SCOPE.
2.ONE COAT OF RED OXIDE & TWO COAT OF APPROVED RAL SHADE WILL BE GIVEN TO THE GATE.
3.GATE WILL CUT IN 2 PART FOR TRANSPORT.

NIHVA
NIHVA TECHNOLOGIES PVT. LTD.
NIHVA TECHNOLOGIES PVT. LTD. PUNE
Email:- info@nihva.com
TEL :020 66304033
Website:- www.nihva.com

TITLE:

SLIDING GATE LEAF

CLIENT'S APPROVAL :

CLIENT -

PROJECT -

SITE LOCATION -KANJIKODE,KERALA.

DWG. NO. : NIHVA/18-19/VDR/250

SCALE: NTS	WT:	SHEET:1 OF 1

	NAME	SIGN	DATE
DRAWN	SURAJ		05-12-2018
CHECK	PRADEEP		05-12-2018
APPROVED	R.D		05-12-2018

IF ANY QUERIES CONTACT:- design@nihva.com

NOTE: ALL DIMENSIONS ARE IN mm

THIS DRAWING & DESIGN IS THE PROPERTY OF NIHVA TECHNOLOGIES. NOT TO BE SOLD OR COPIED TO ANY OTHER CONCERN.