Revision		Date	By
A	Corrected mullion hoist positions, floor pits altered	2022-09-02	EB

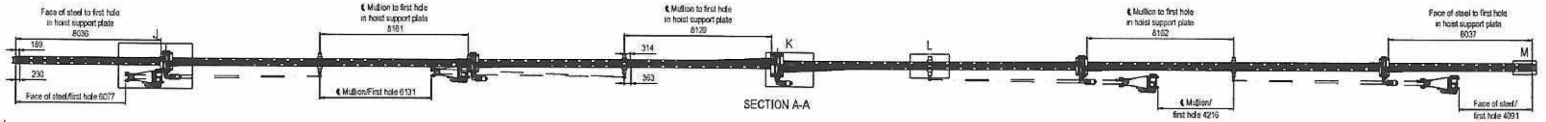

SECTION A-A

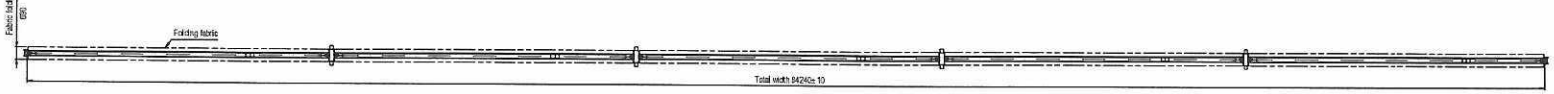

SECTION B-B

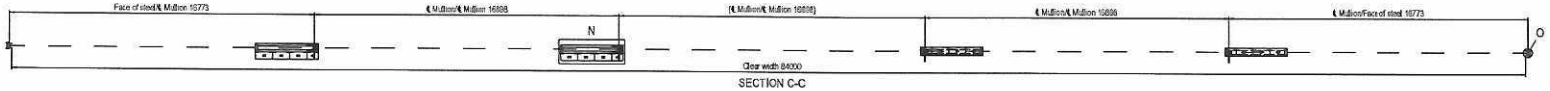
Face of steel/℄ Mullion 16773
℄ Mullion/℄ Mullion 16898
N
(℄ Mullion/℄ Mullion 16898)
℄ Mullion/℄ Mullion 16898
℄ Mullion/Face of steel 16773
O
Clear width 84000

SECTION C-C

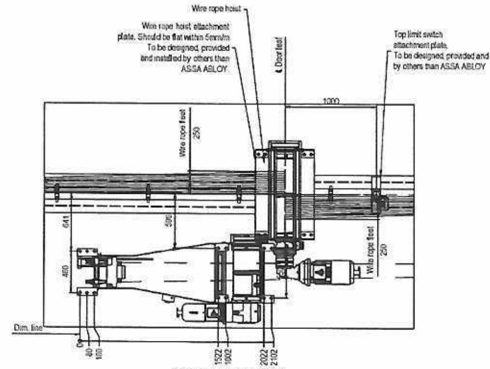
Wire rope hoist
Wire rope hoist attachment plate. Should be flat within 5mm/m
To be designed, provided and installed by others than ASSA ABLOY
℄ Door leaf
Top limit switch attachment plate,
To be designed, provided and installed by others than ASSA ABLOY
1000
Wire rope fleet 250
Wire rope fleet 250
641
596
460
Dim. line
0
40
100
1522
1602
2022
2102

DETAIL J, SCALE (1:20)

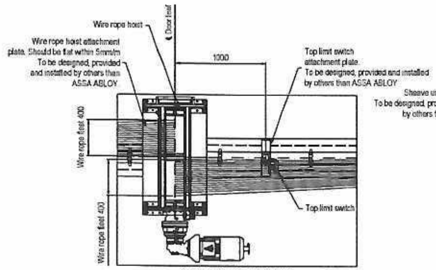
Wire rope hoist
Wire rope hoist attachment plate. Should be flat within 5mm/m
To be designed, provided and installed by others than ASSA ABLOY
℄ Door leaf
1000
Top limit switch attachment plate.
To be designed, provided and installed by others than ASSA ABLOY
Wire rope fleet 400
Wire rope fleet 400
Top limit switch

DETAIL K, SCALE (1:20)

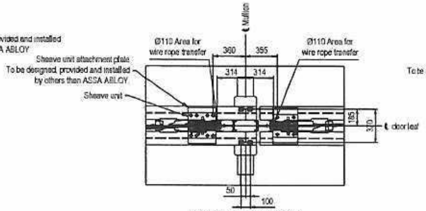
℄ Mullion
Ø110 Area for wire rope transfer
Ø110 Area for wire rope transfer
360
355
314
314
Sheave unit attachment plate
To be designed, provided and installed by others than ASSA ABLOY
Sheave unit
185
370
℄ door leaf
50
100

DETAIL L, SCALE (1:20)

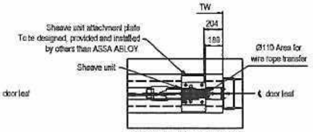
TW
204
188
Sheave unit attachment plate
To be designed, provided and installed by others than ASSA ABLOY
Sheave unit
Ø110 Area for wire rope transfer
℄ door leaf

DETAIL M, SCALE (1:20)

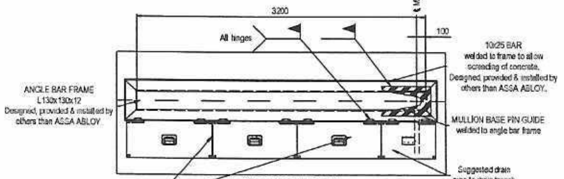
3200
℄ Mullion
All hinges
100
10x25 BAR welded to frame to allow screeding of concrete. Designed, provided & installed by others than ASSA ABLOY.
ANGLE BAR FRAME L130x130x12 Designed, provided & installed by others than ASSA ABLOY
MULLION BASE PIN GUIDE welded to angle bar frame
Suggested drain pipe to drain trench
Hinged lid

DETAIL N, SCALE (1:20)

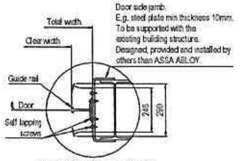
Total width
Clear width
Door side jamb.
E.g. steel plate min thickness 10mm.
To be supported with the existing building structure.
Designed, provided and installed by others than ASSA ABLOY.
Guide rail
℄ Door
Self tapping screws
245
290

DETAIL O, SCALE (1:10)

DOOR IDENTITY NUMBER: 8480O001

LOAD DIAGRAM & NOTES, ref. to drwng. no. 77446

INTERFACE, SECTIONS ref. to drwng. no. 77445

INTERFACE, ELEVATION ref. to drwng. no. 77443

EB
A1F
1:100
84500
2022-08-23

GMR Aero Technic Hangar1
India
Megadoor 84000x23000/14000
Interface, Plan views

77444
A

NIHVA TECHNOLOGIES PVT. LTD. * PUNE *