

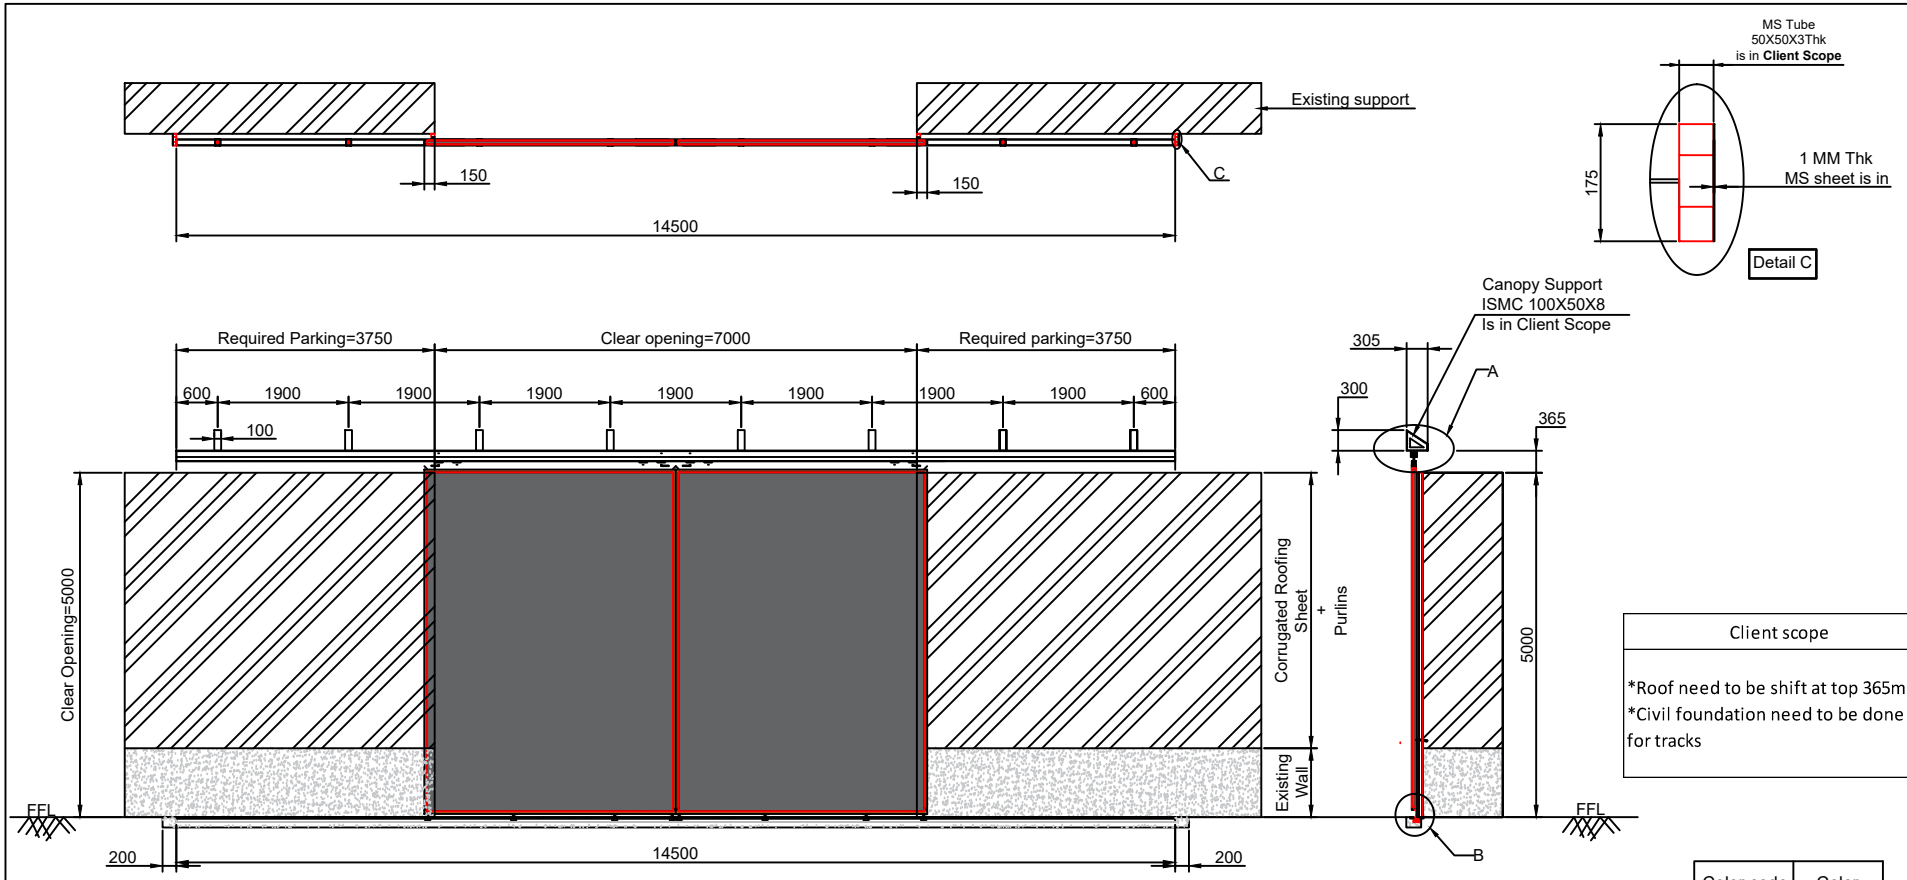


Client scope
*Roof need to be shift at top 365mm. *Civil foundation need to be done for tracks

Color code	Color
5018	Turquoise blue

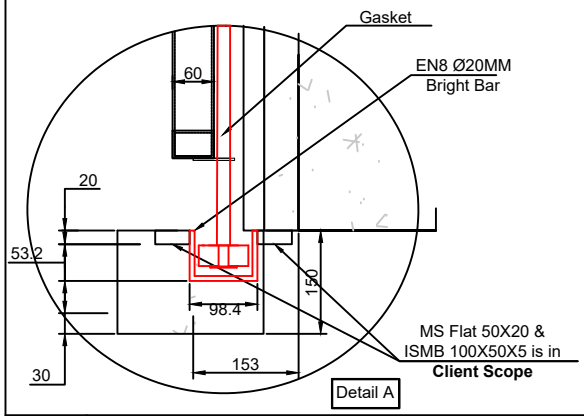

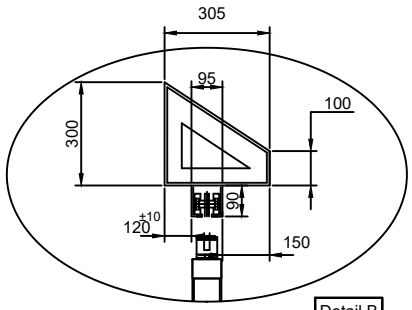

Note:--

1.All dimension are in MM

2.All Civil work will be in client scope

3.Manufacturing,civil and installation tolerance will be ±10mm

4.Top and Bottom track should be in parallal within ±3mm

5.Nihva Supervisor on site for Monitoring/Checking of civil work

This drawing & design is the property of NIHVA TECHNOLOGIES. Not to be sold or copied to any other concern.

	Revision	Date	Revised By

TITLE:-2LEAF-BOTH SIDE CRM DOOR-14

NIHVA TECHNOLOGIES PVT. LTD.

NIHVA TECHNOLOGIES PVT. LTD. PUNE
Tel : 020 66304033
Email:- info@nihva.com
Website:- www.nihva.com

	NAME	DATE	SIGN
DRAWN	M.SUTAR	20/05/2022	
CHECK	M.SUTAR	20/05/2022	
APPRD.	V.TARAK	20/05/2022	

If any queries contact : design@nihva.com

ALL DIMENSION ARE IN mm

CLIENT - LESTECH

LOCATION - POSCO MANGAON

PRODUCT - SLIDING DOOR - OVERHEAD

DWG NO:-NIHVA/22-23/CLT/0045 REV- 0

SCALE: NTS SCALE:-- 1:1 SHEET: 01 OF 01