


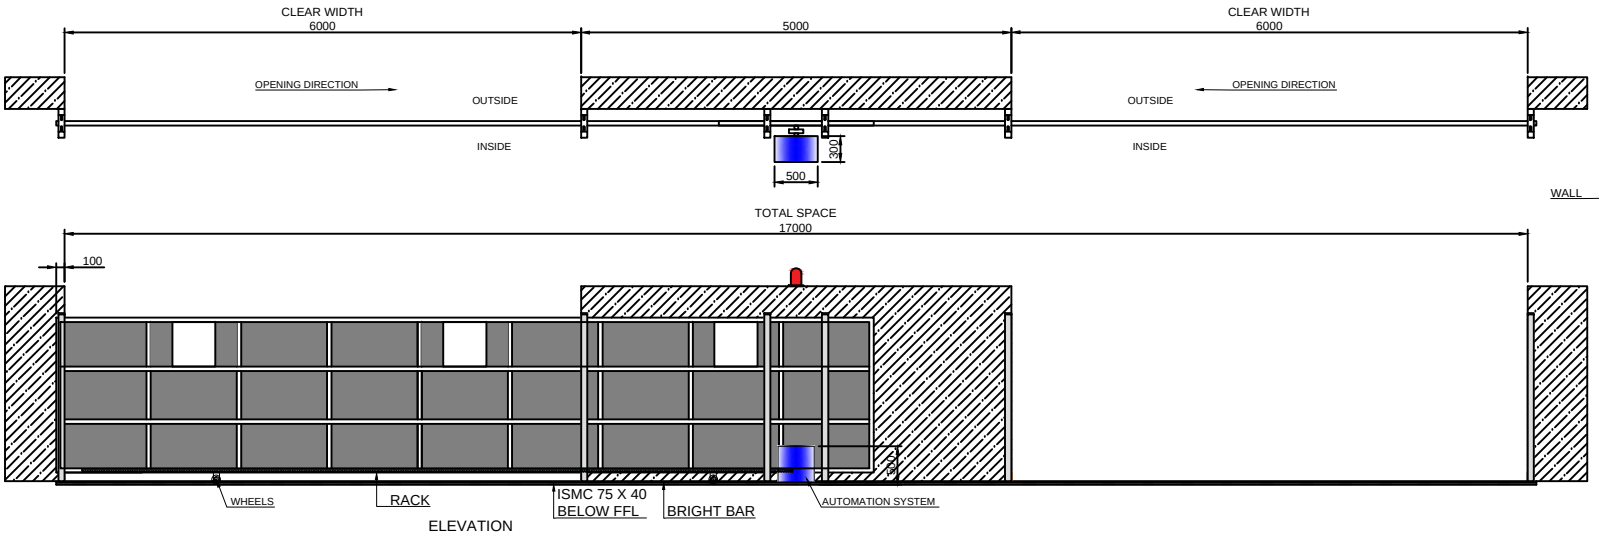


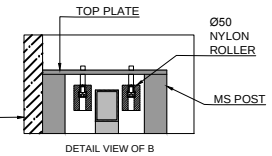

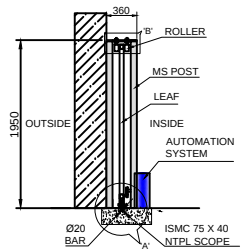

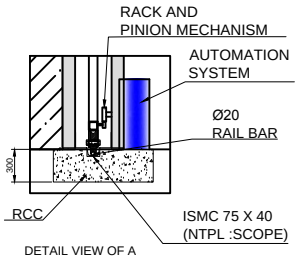

NOTE-
1. ALL REQUIRED CIVIL WORK WILL BE IN CLIENTS SCOPE.
2. TWO COATS OF PRIMER AND TWO COATS OF SYNTHETIC ENAMEL PAINT OF APPROVE SHADE.
3. SAFETY ACCESSORIES : FLASHING LIGHT, SAFETY PHOTOCELL, BUZZER, E.OFF PUSH BUTTON.
4. GATE LEAF WILL BE IN TWO PARTS FOR TRANSPORTATION & WILL BE WELD TOGETHER ON SITE.

TOLERANCE- ±10mm

REV NO	DATE	DRAWN	REMARK
R01	20.08.20	DRAWN	1. MOTOR DIMENSIONS ADD

This drawing & design is the property of NIHVA TECHNOLOGIES. Not to be sold or copied to any other concern.

TITLE			
AUTOMATIC SLIDING GATE			
	NAME	SIGN	DATE
DRAWN	P.A		06.04.2020
CHECK	G.J		06.04.2020
APPRD.			

NIHVA TECHNOLOGIES PVT. LTD.
NIHVA TECHNOLOGIES PVT. LTD, PUNE
Tel : 020 66304033
Email:- info@nihva.com
Website:- www.nihva.com

CLIENT - CLOOS INDIA WELDING TECHNOLOGY PVT LTD
PROJECT -
SITE LOCATION - BHOSARI, PUNE
If any queries contact : design@nihva.com
DWG. NO. : NIHVA/20-21/0001/R01
REV- R01
ALL DIMENSION ARE IN mm
SCALE: NTS
WT:
SHEET: