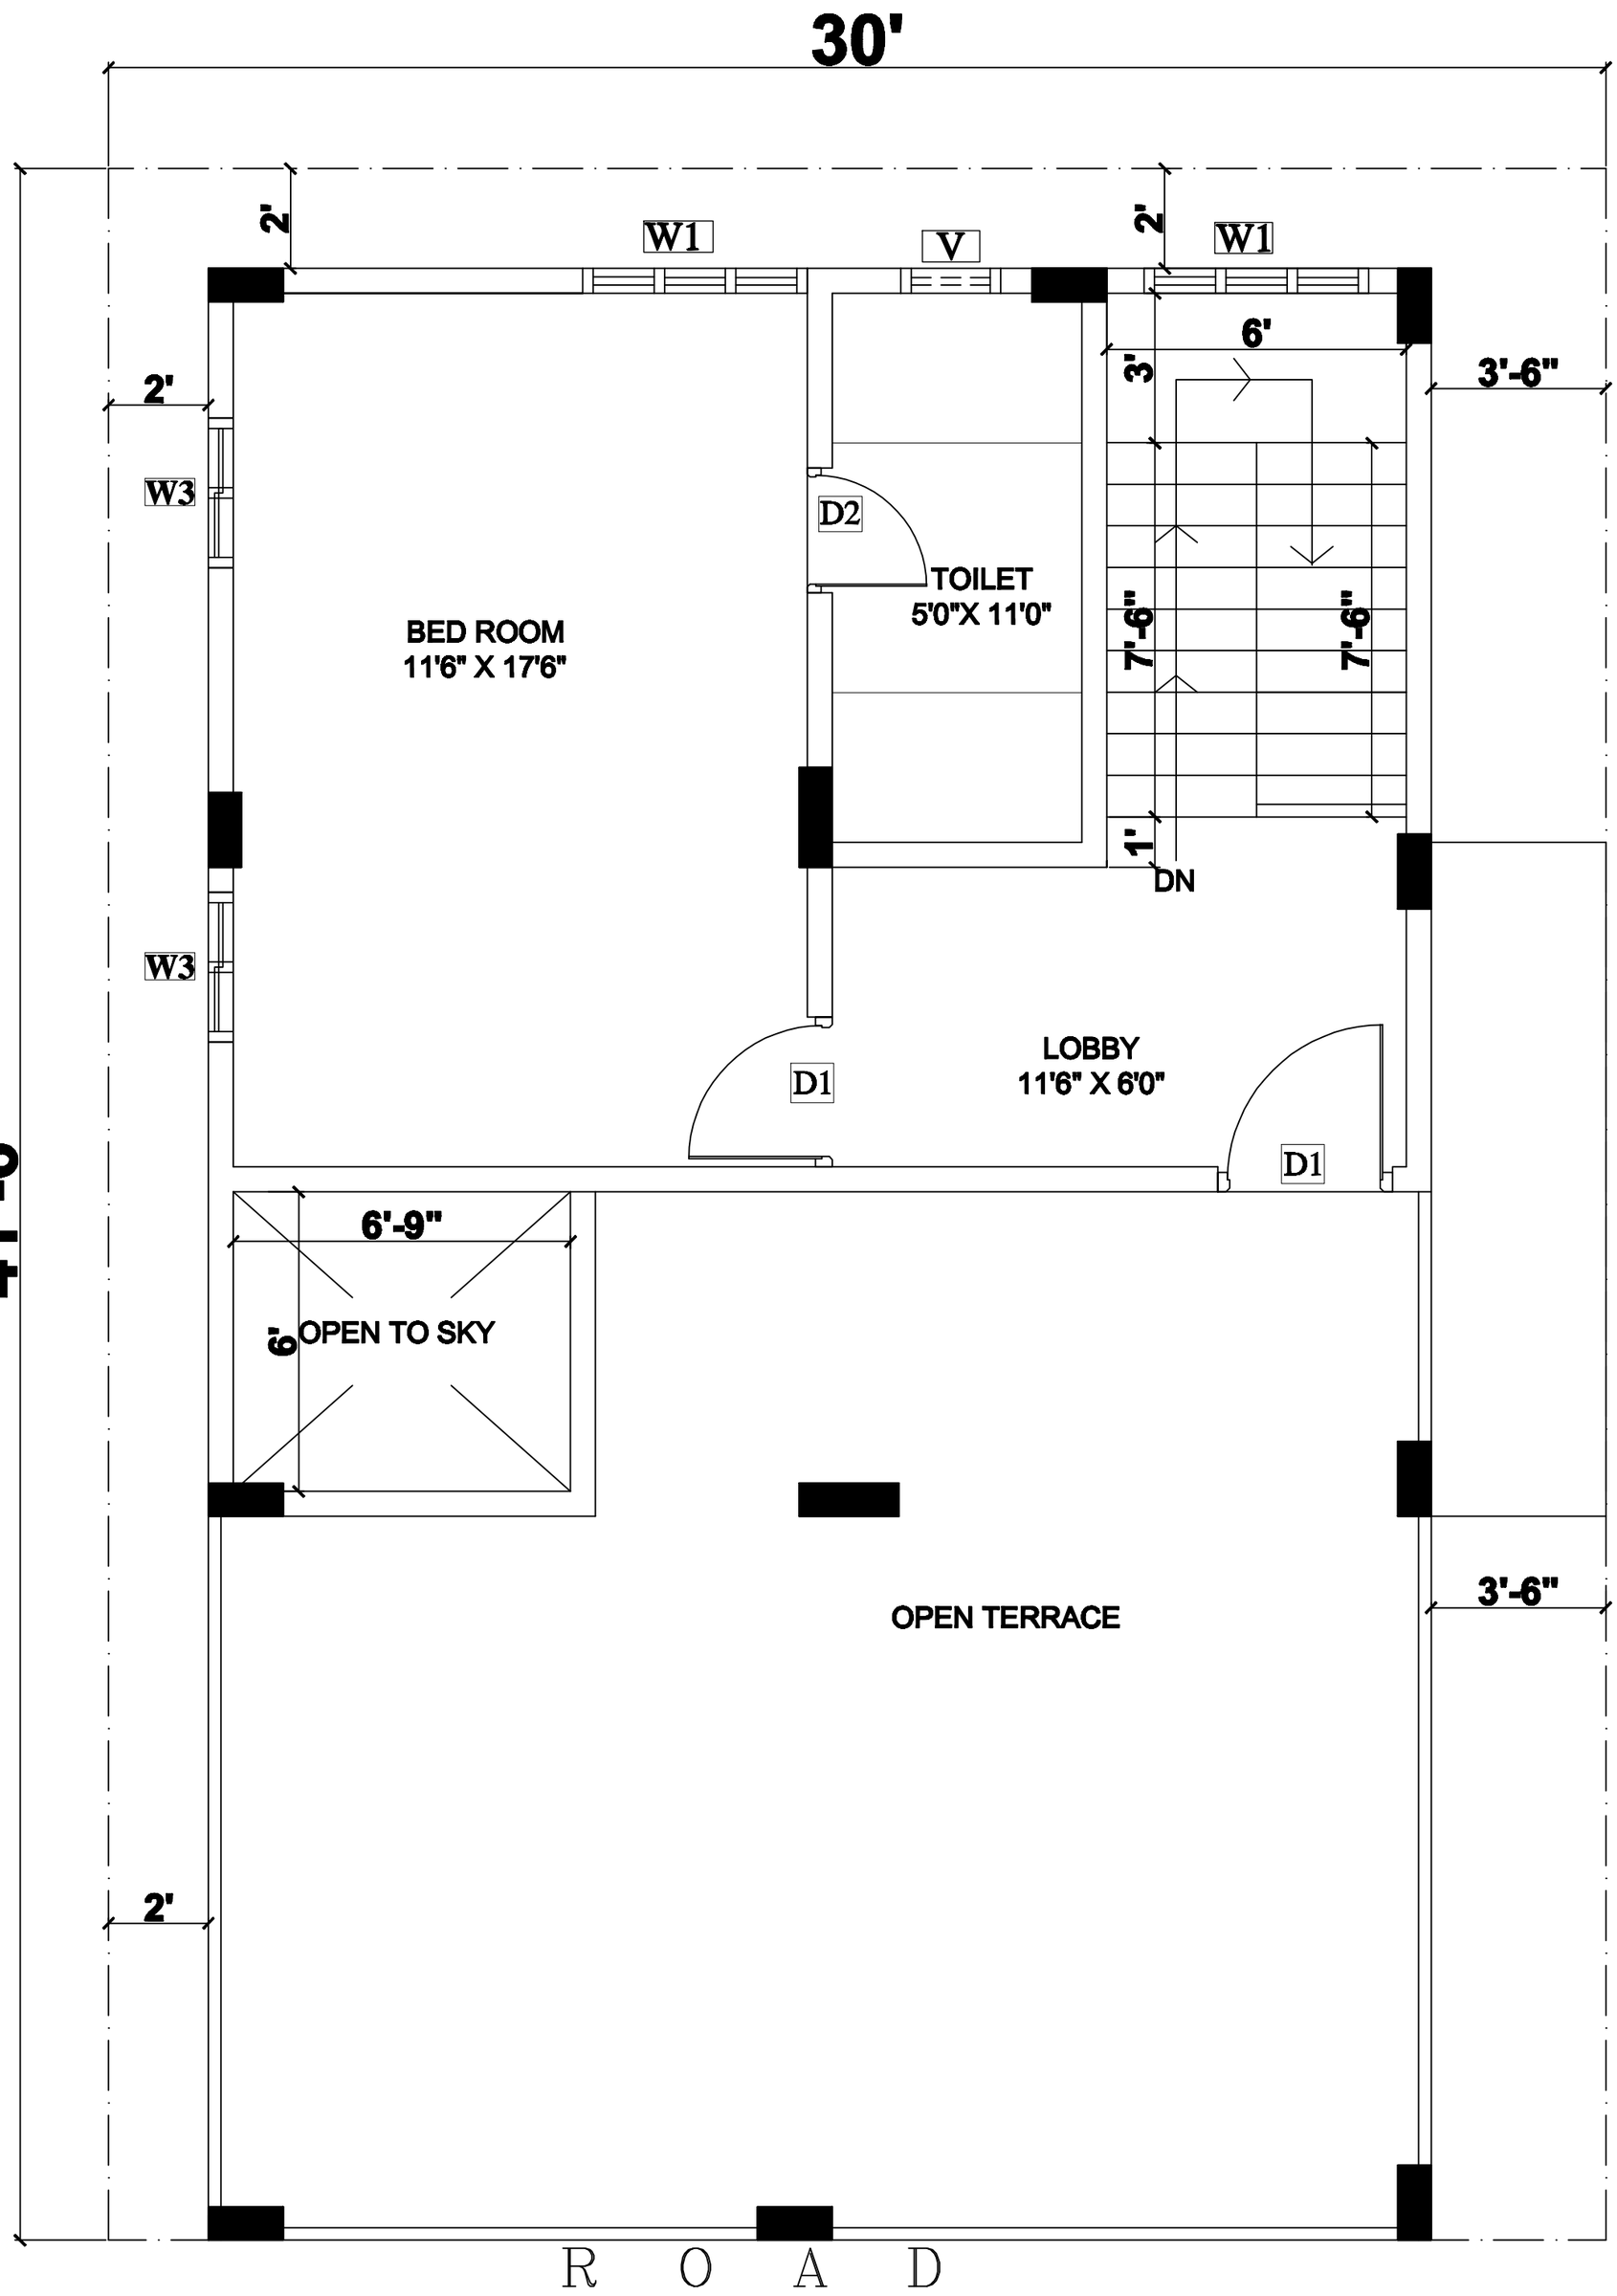


SCHEDULE OF OPENINGS

DOORS

SL NO,	TYPE	SIZE	REQ NO. GF	FF
01	ED	3'6" X 7'0"		
02	D1	3'0" X 7'0"		
03	D2	2'6" X 7'0"		
04				
05				

WINDOWS

SL NO,	TYPE	SIZE	REQ NO. GF	FF
01	W	6'0" X 4'6"		
02	W1	4'6" X 4'6"		
03	W2	4'6" X 3'0"		
04	W3	3"0" X 4'6"		
05	FW	6'0" X 7'0"		
06				

VENTILATORS

01	V	2'0" X 2'6"		
02				

BUILT UP AREA = 453.25 SFT

SKYLIGHT AREA = 50.50 SFT

NOTES

DRAWING NOT TO BE SCALED ,WRITTEN DIMENSIONS TO BE FOLLOWED ONLY

DIMENSIONS SHOULD BE CHECKED AND VARIFIED ON SITE BEFORE EXICUTION OF WORK.

READ ARCHITECTURAL DRAWING ALONG WITH STRUCTURAL DRAWING FOR CIVIL WORK BEFORE EXICUTION OF WORK.

THIS DRAWING IS THE PROPERTY OF VIJAY ASSOCIATES.
IT SHALL NOT BE COPIED, REPRODUCED OR TRANSFERED. IN ANY MANNER EITHER IN PART OR FULL WHAT SO EVER AND SHALL BE USED ONLY FOR THE JOB ISSUE FOR

N

CLIENT: Mr. SIDDARTH

DRG TITLE: TERRACE FLOOR FURNITURE & PLUMBING PLAN.

DRG No;

REVISIONS

SCALE: 1" = 4'0"

DATE

DSND BY ANJALIPRASAD

CHKD BY M.VIJAYENDRA.

ARCHITECTS
VIJAY ASSOCIATES.
ARCHITECTS, ENGINEERS & CONTRACTORS.
FIRST FLOOR SREERAMA SHOPPING COMPLEX
MARATHALLI , BANGALORE – 560 037.
Ph: No.9845026160