



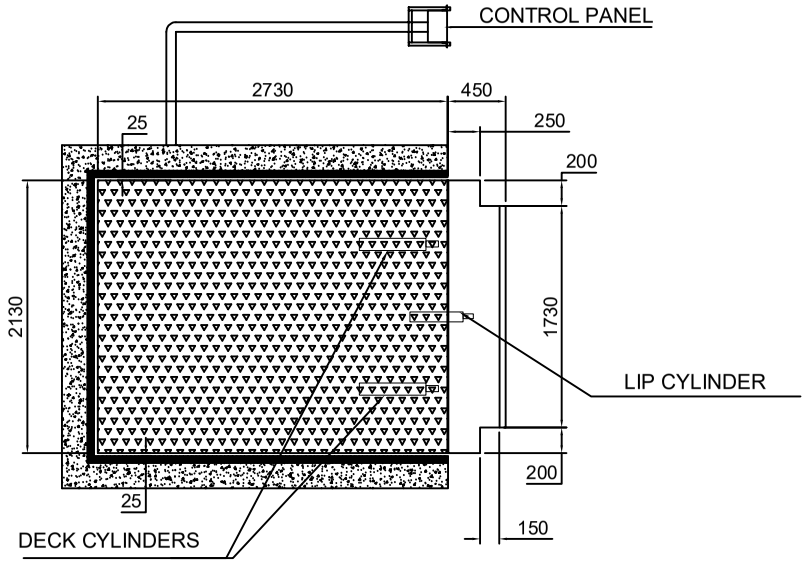


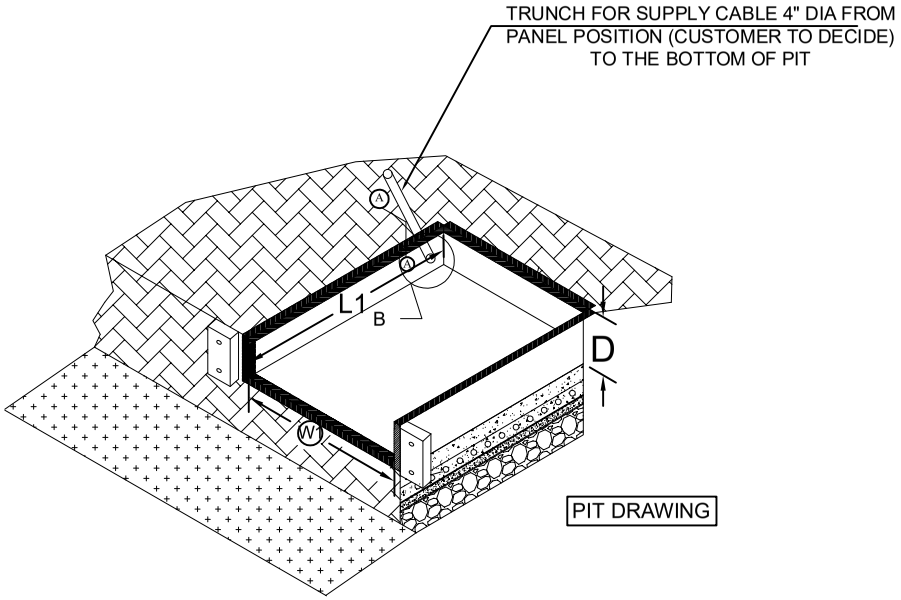

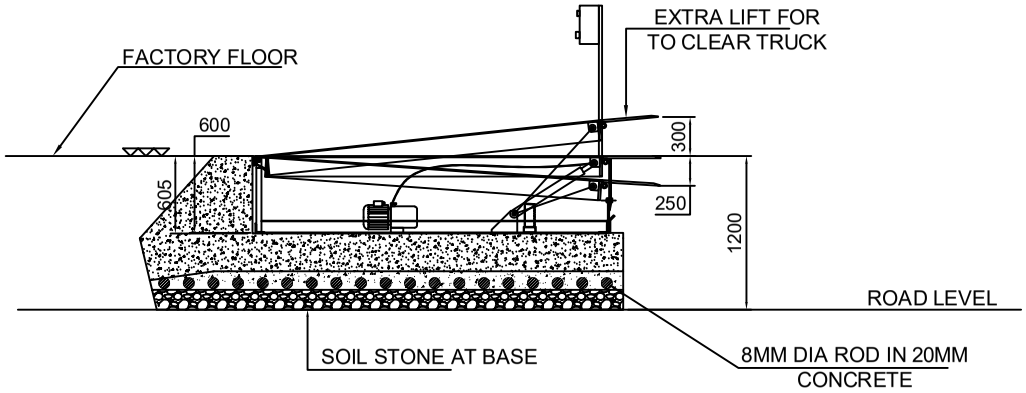

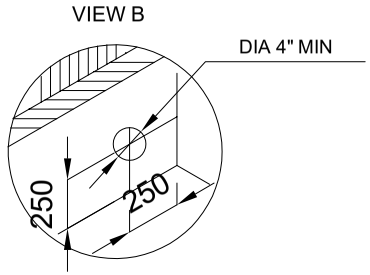

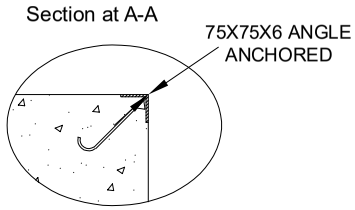

DOCK LEVELER SIZE	WIDTH (W)	LENGTH (L)	HEIGHT (H)	LIP (C) LENGTH
	2130	2730	600	450
PIT DIMENSION	WIDTH (W 1)	LENGTH (L 1)	DEPTH (D)	
DL	2180	2760	605	

NOTE: -
1. PROPER DRAINAGE SHOULD BE DONE
2. TRENCH AS SHOWN SHOULD BE MADE BY DECIDING THE POWER PACK POSITION.
3. LEVEL OF THE PIT SHOULD BE PLAIN AND SHOULD TAKE AT LEAST 18000 KG FLOOR LOADING
4. FABRICATION TOLERANCE FOR PLATFROM SIZE WILL BE ± 15 MM.
5.PIT,DUCT FOR HOSES & ALL CIVIL WORK IN CLIENT SCOPE

This drawing & design is the property of NIHVA TECHNOLOGIES. Not to be sold or copied to any other concern.

TITLE:- DOCK LEVELER GA DRAWING

	NAME	DATE	SIGN
DRAWN	SUJATA	22/12/2021	
CHECK	GANESH.P	22/12/2021	
APPRD.	A.K		

NIHVA TECHNOLOGIES PVT. LTD.
NIHVA TECHNOLOGIES PVT. LTD. PUNE
Tel : 020 66304033
Email:- info@nihva.com
Website:- www.nihva.com

CLIENT - Elegant Offset Printers Private Limited
LOCATION - BELGAUM
PRODUCT - DOCK LEVELER
If any queries contact : design@nihva.com
DWG NO:-NIHVA/21-22/CLT/0273 REV- 0
ALL DIMENSION ARE IN mm
SCALE: NTS SCALE:-- 1:1 SHEET: 01 OF 01

Rev No.	Revision	Date	Revised By