
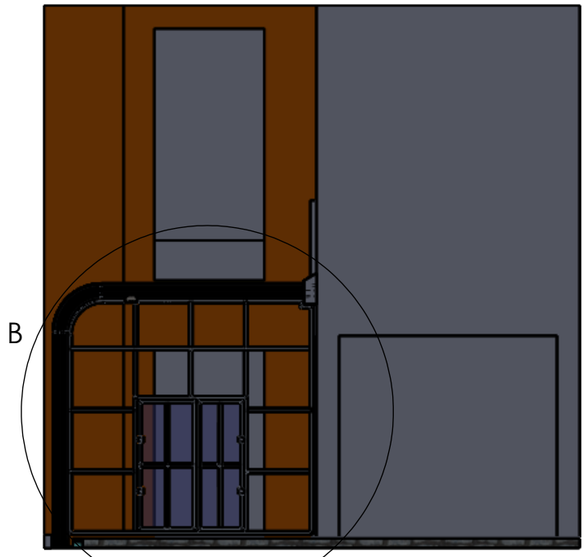


FRONT VIEW

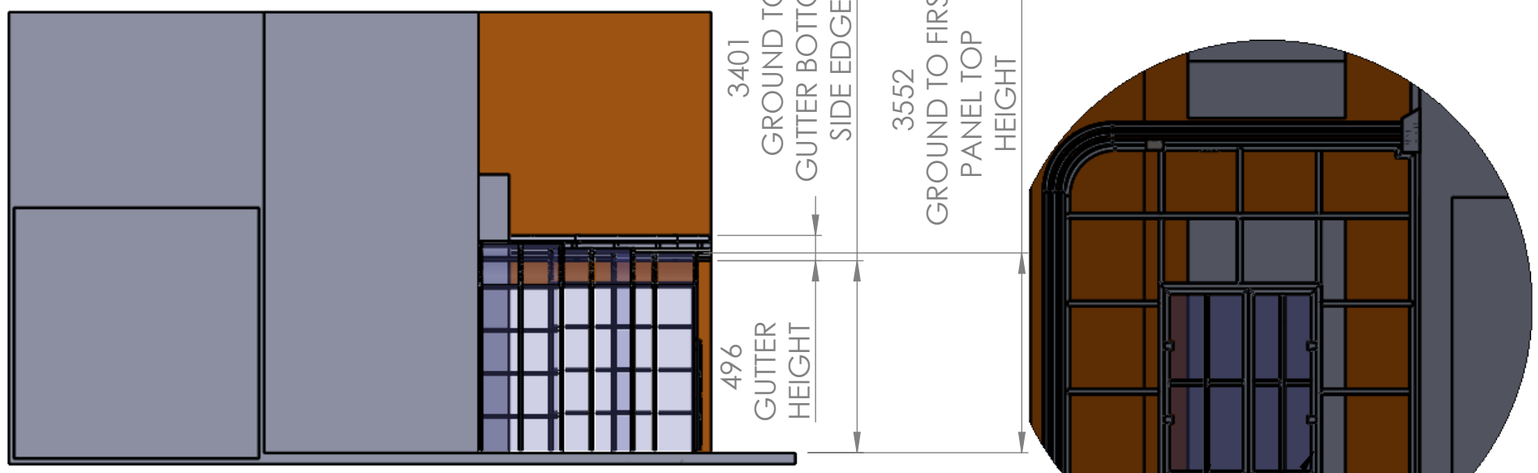


SIDE VIEW


DETAIL B
SCALE 1 : 70

DOOR 1
WIDTH -900MM
HEIGHT - 2200 MM
OPENING ANGLE- 180 degree


DOOR 2
WIDTH -900MM
HEIGHT - 2200 MM
OPENING ANGLE- 180 degree

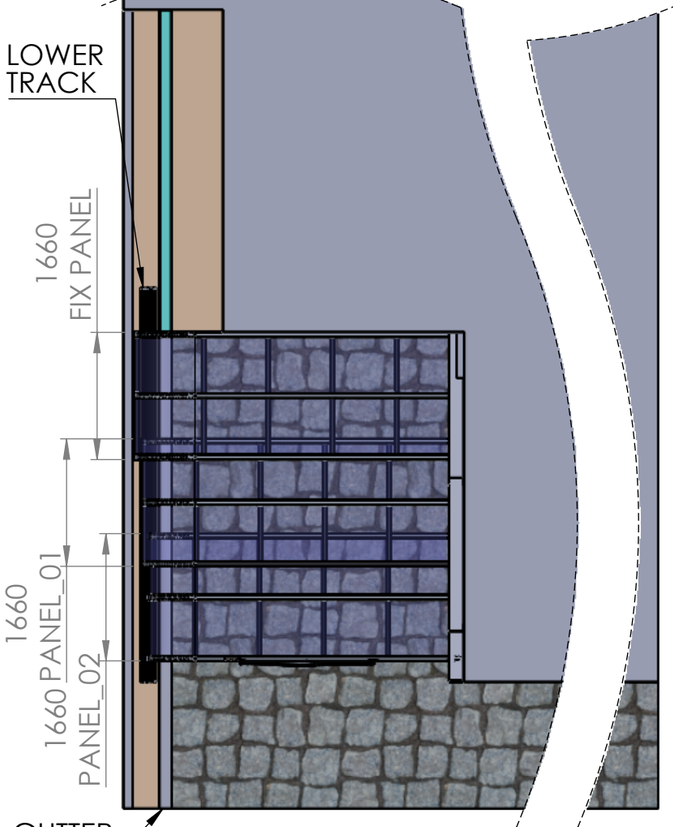

TOP VIEW CLOSE POSITION

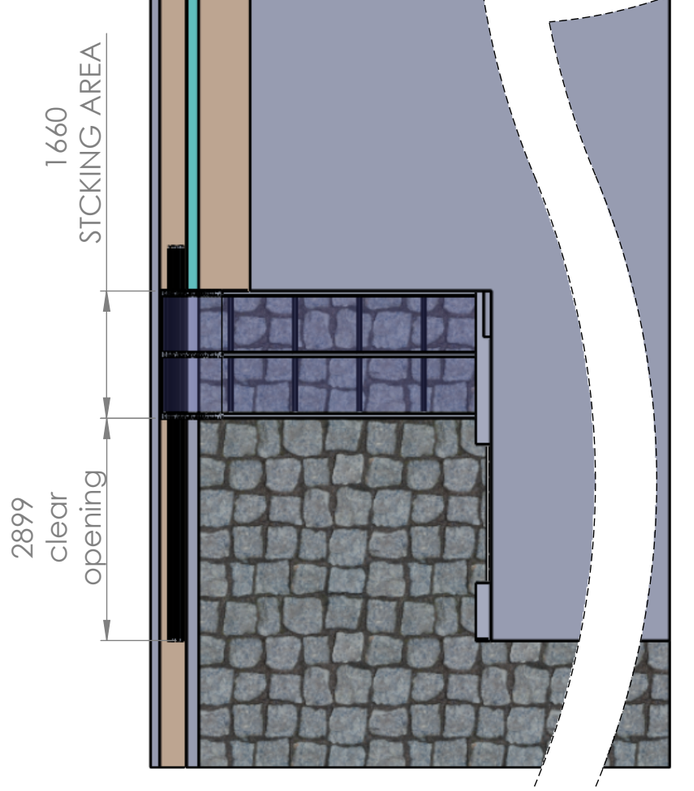


TOP VIEW OPEN POSITION

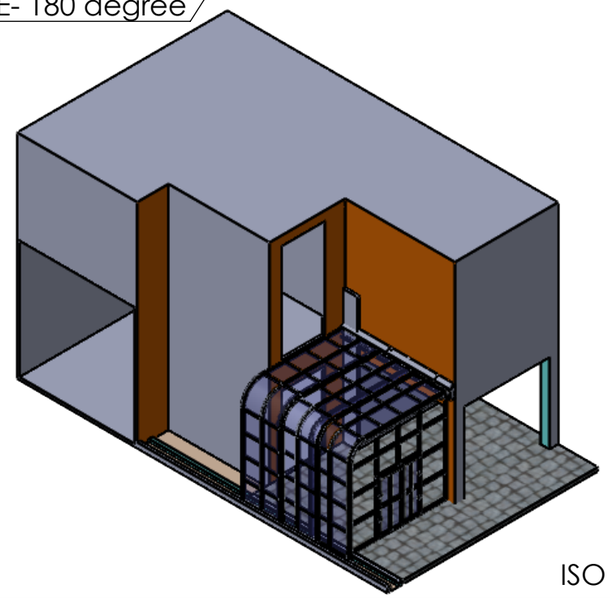

ISO VIEW

TITLE - BALCONY ENCLOSUR				NIHVA TECHNOLOGIES PVT.LTD.PUNE Website - www.nihva.com
DWG NO - NTPL-263-PM-GA			QTY - 1	
	NAME	SIGNATURE	DATE	PROJECT NO - NTPL-263-PM
DRAWN	S.W		14-04-2025	PRODUCT - BALCONY ENCLOSURE
CHK'D	P.M.		14-04-2025	SITE LOCATION - MUMBAI
APPV'D	V.T.		14-04-2025	
if any queries contact - supportautomation@nihva.com				REVISION - 04
ALL DIMENSION ARE IN mm			A3	SCALE - SHEET 1 OF 12

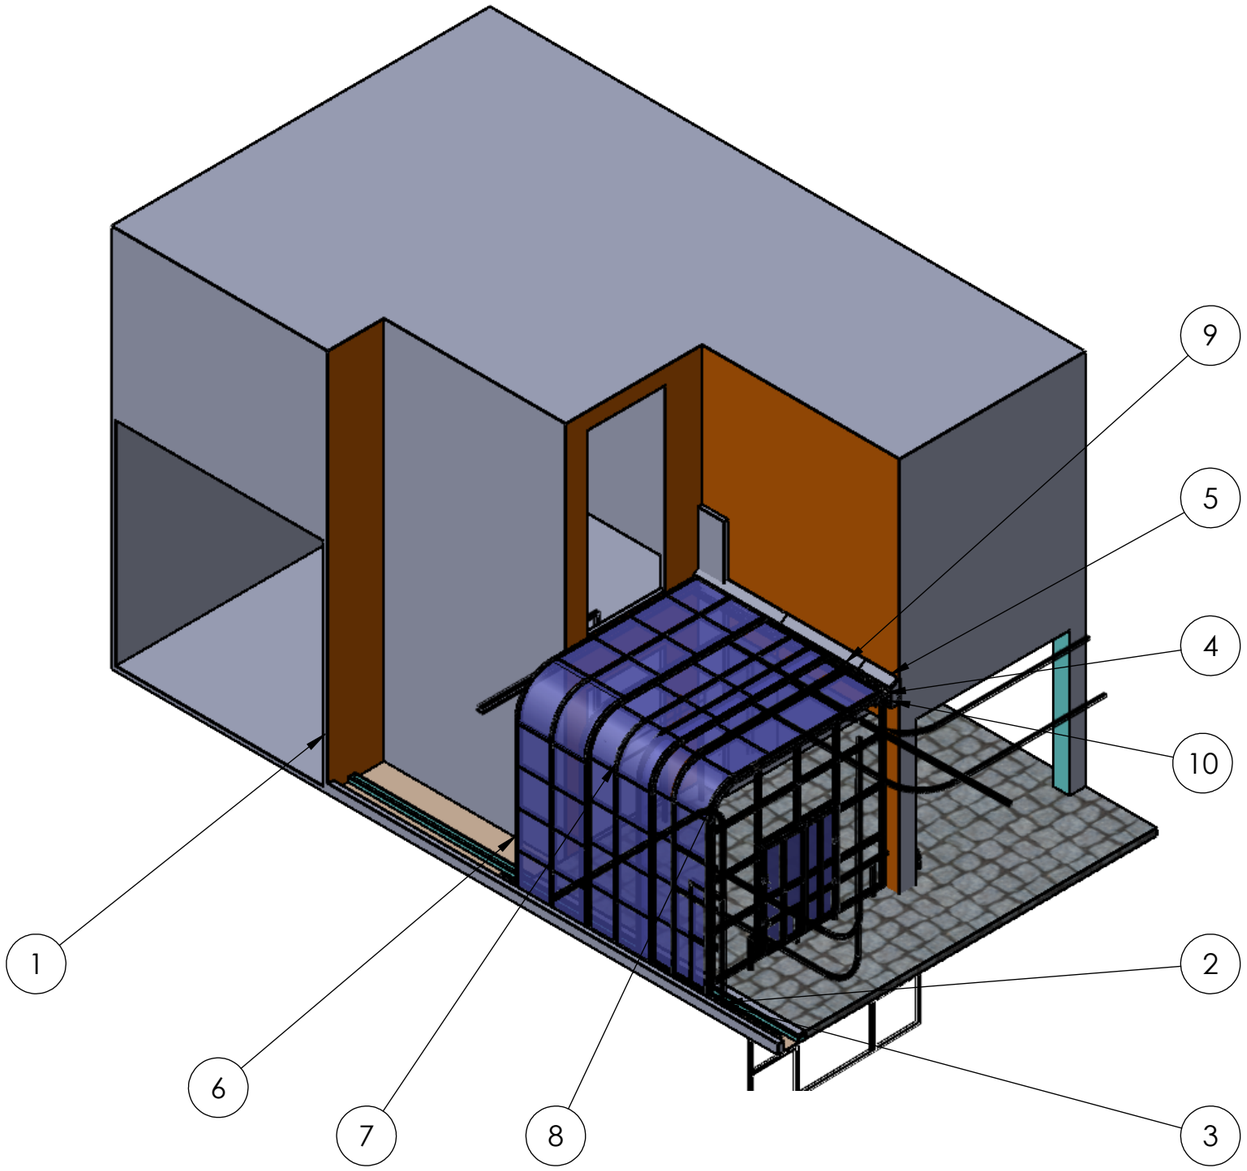

ISO VIEW

ITEM NO.	PART NUMBER	DESCRIPTION	QTY.
1	NEWCIVIL BASE	SITE BASE	1
2	NEWGNT_001	BOTTOM TRACK	1
3	NEWGNT_002	BOTTOM TRACK	1
4	NEWSBR GUIDE RAIL	STD PART	2
5	NEWGUIDE RAIL MTG PLATE	ALUMINIUM (PLATE ANCHORING TO WALL)	6
6	NEWFIX PANEL	(BIG)FIX PANEL	1
7	NEWPANEL_01FIX PANEL	PANEL_01(MOVEING)	1
8	NEWPANEL_02PANEL_01FIX PANEL	PANEL_02 (MOVEING)	1
9	Gutter		2
10	END PLATE AND GUTTER ASM		1

TITLE - BALCONY ENCLOSER				NIHVA TECHNOLOGIES PVT.LTD.PUNE
DWG NO - NTPL263-PM			QTY - 1	Website - www.nihva.com
	NAME	SIGNATURE	DATE	PROJECT NO - NTPL263-PM
DRAWN	S.W		30-01-2025	PRODUCT - BALCONY ENCLOSURE
CHK'D	P.M.		30-01-2025	SITE LOCATION - MUMBAI
APPV'D	V.T.		30-01-2025	
if any queries contact - supportautomation@nihva.com				REVISION -
ALL DIMENSION ARE IN mm			A3	SCALE - SHEET 2 OF 12


ITEM NO.	PART NUMBER	DESCRIPTION	QTY.
1	NEWGNT_001	BOTTOM TRACK	1
			1





TITLE - BALCONY ENCLOSER				NIHVA TECHNOLOGIES PVT.LTD.PUNE
DWG NO - NTPL263-PM			QTY - 1	Website - www.nihva.com
	NAME	SIGNATURE	DATE	PROJECT NO - NTPL263-PM
DRAWN	S.W		30-01-2025	PRODUCT - BALCONY ENCLOSURE
CHK'D	P.M.		30-01-2025	SITE LOCATION - MUMBAI
APPV'D	V.T.		30-01-2025	
if any queries contact - supportautomation@nihva.com				REVISION -
ALL DIMENSION ARE IN mm		A3		SCALE - SHEET 3 OF 12


ITEM NO.	PART NUMBER	DESCRIPTION	QTY.
1	NEWGNT_002	BOTTOM TRACK	1
			1

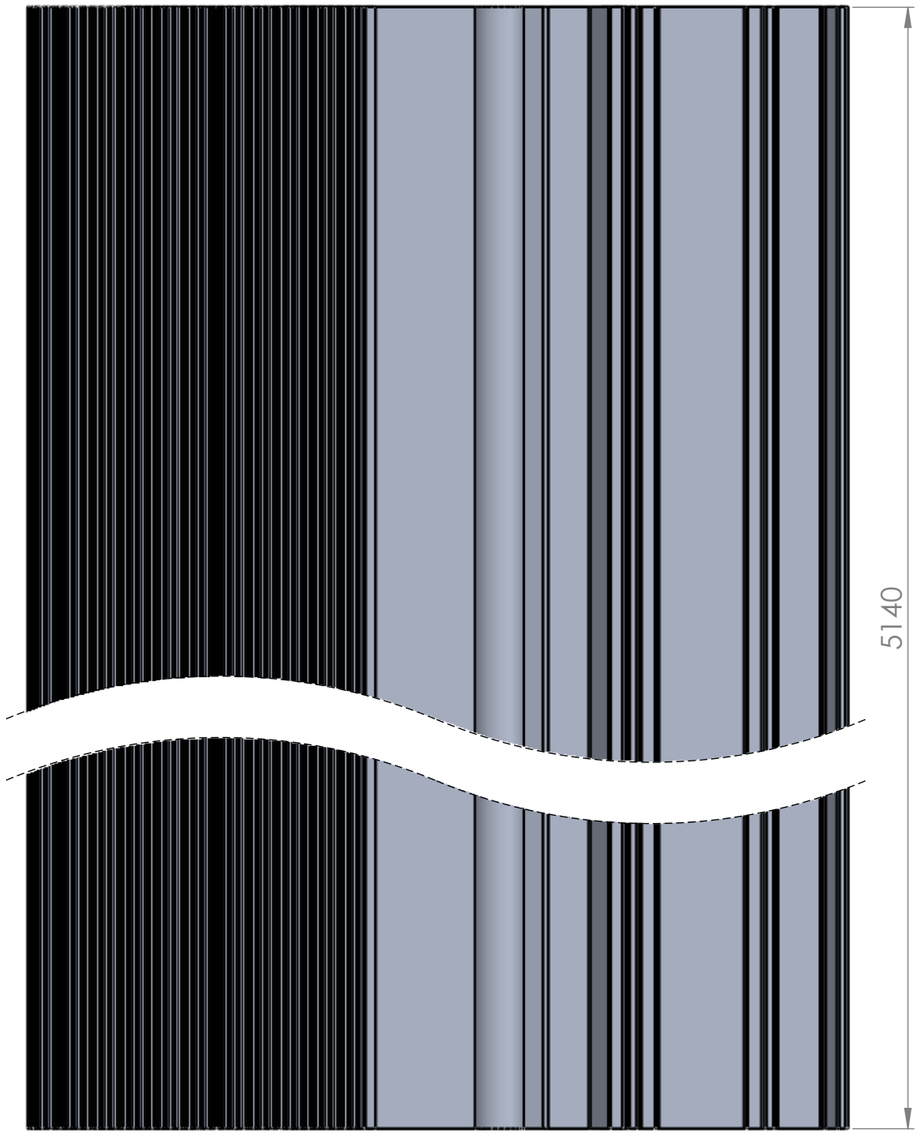




TITLE - BALCONY ENCLOSER				NIHVA TECHNOLOGIES PVT.LTD.PUNE
DWG NO - NTPL263-PM			QTY - 1	Website - www.nihva.com
	NAME	SIGNATURE	DATE	PROJECT NO - NTPL263-PM
DRAWN	S.W		30-01-2025	PRODUCT - BALCONY ENCLOSURE
CHK'D	P.M.		30-01-2025	SITE LOCATION - MUMBAI
APPV'D	V.T.		30-01-2025	
if any queries contact - supportautomation@nihva.com				REVISION -
ALL DIMENSION ARE IN mm		A3		SCALE - SHEET 4 OF 12


ITEM NO.	PART NUMBER	DESCRIPTION	QTY.
1	NEWSBR GUIDE RAIL	STD PART	5

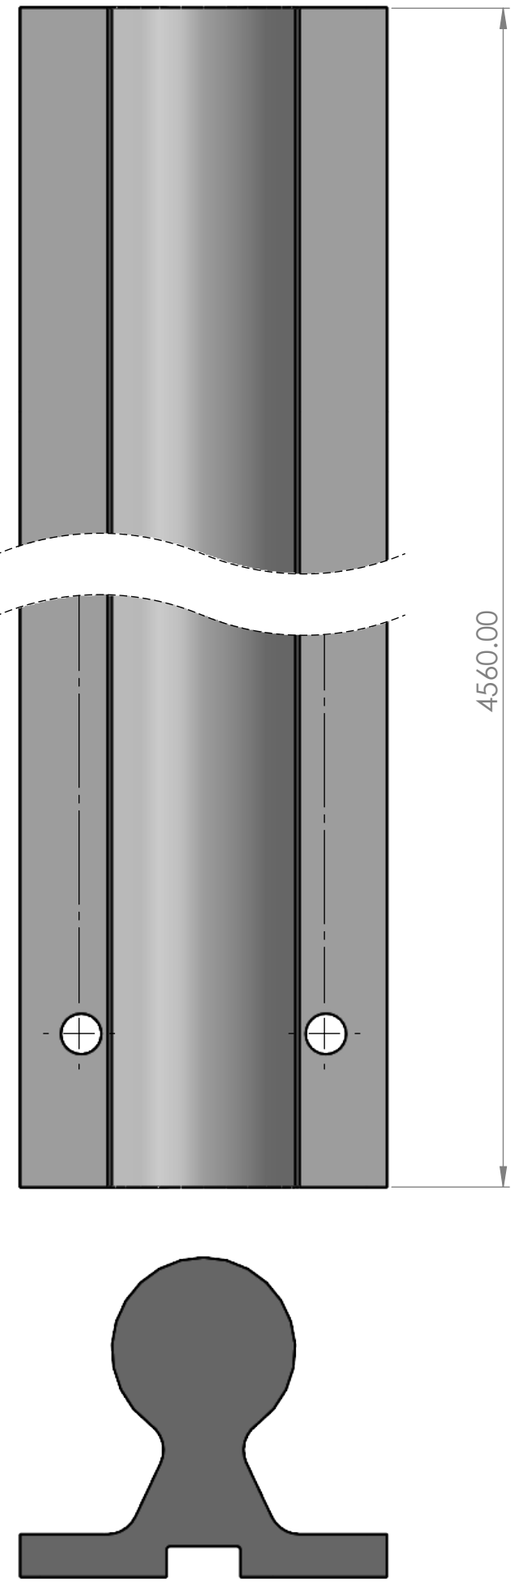


TITLE - BALCONY ENCLOSER				NIHVA TECHNOLOGIES PVT.LTD.PUNE
DWG NO - NTPL263-PM			QTY - 1	Website - www.nihva.com
	NAME	SIGNATURE	DATE	PROJECT NO - NTPL263-PM
DRAWN	S.W		30-01-2025	PRODUCT - BALCONY ENCLOSURE
CHK'D	P.M.		30-01-2025	SITE LOCATION - MUMBAI
APPV'D	V.T.		30-01-2025	
if any queries contact - supportautomation@nihva.com				REVISION -
ALL DIMENSION ARE IN mm			A3	SCALE - SHEET 5 OF 12

ITEM NO.	PART NUMBER	DESCRIPTION	QTY.
1	NEWGUIDE RAIL MTG PLATE	ALUMINIUM (PLATE ANCHORING TO WALL)	6

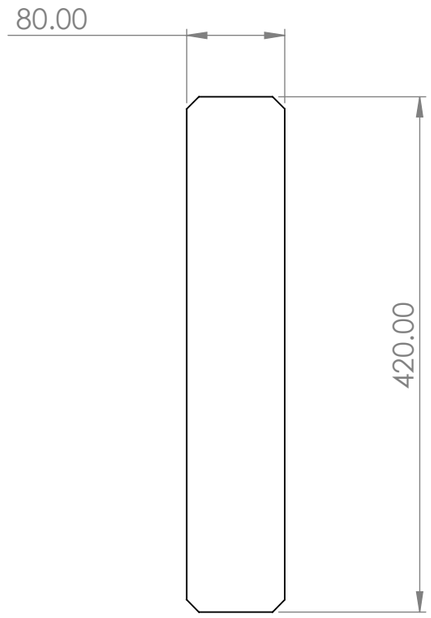


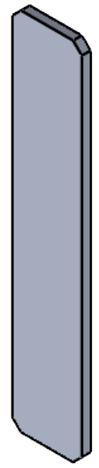


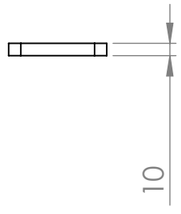



TITLE - BALCONY ENCLOSER				NIHVA TECHNOLOGIES PVT.LTD.PUNE Website - www.nihva.com
DWG NO - NTPL263-PM			QTY - 1	
	NAME	SIGNATURE	DATE	PROJECT NO - NTPL263-PM
DRAWN	S.W		30-01-2025	PRODUCT - BALCONY ENCLOSURE
CHK'D	P.M.		30-01-2025	SITE LOCATION - MUMBAI
APPV'D	V.T.		30-01-2025	
if any queries contact - supportautomation@nihva.com				REVISION -
ALL DIMENSION ARE IN mm			A3	SCALE -

ITEM NO.	PART NUMBER	DESCRIPTION	QTY.
1	NEWFIX PANEL PROFILE _ 01	GNT_006	3
2	NEWSBR BEARING FITTED PROFILE	GNT_006	1
3	NEWGNT_006	GNT_006 MOUNTING IN GROUND	1
4	AL Support tube SQ TUBE 40X40X1.5 MM L-734 MM	ALUMINIUM	16
5	polycarbonate sheet		1

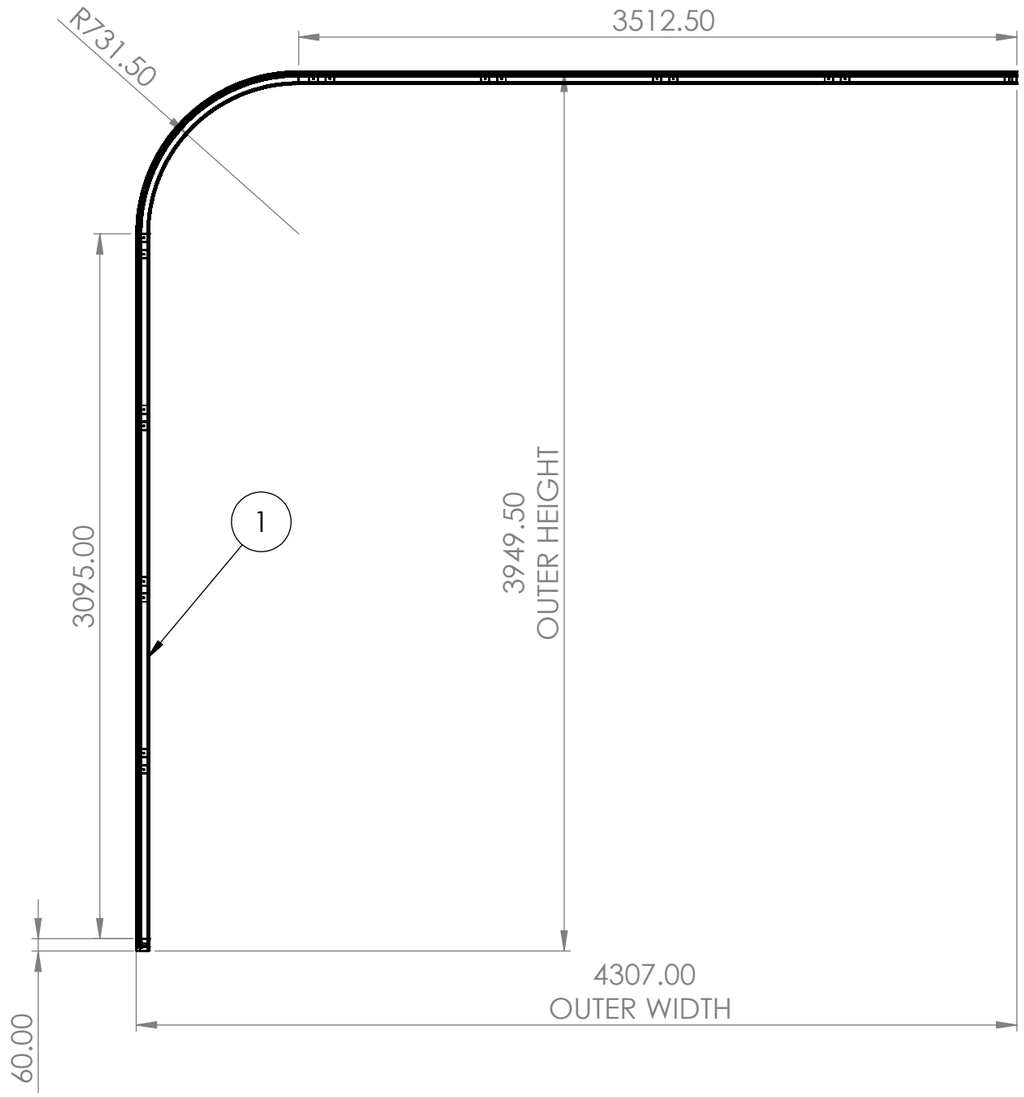

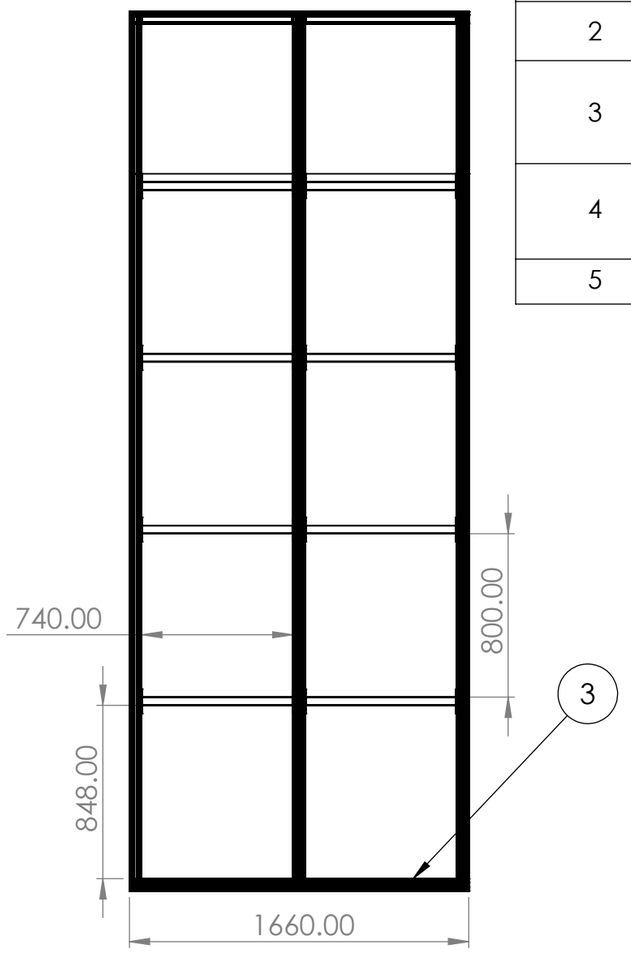

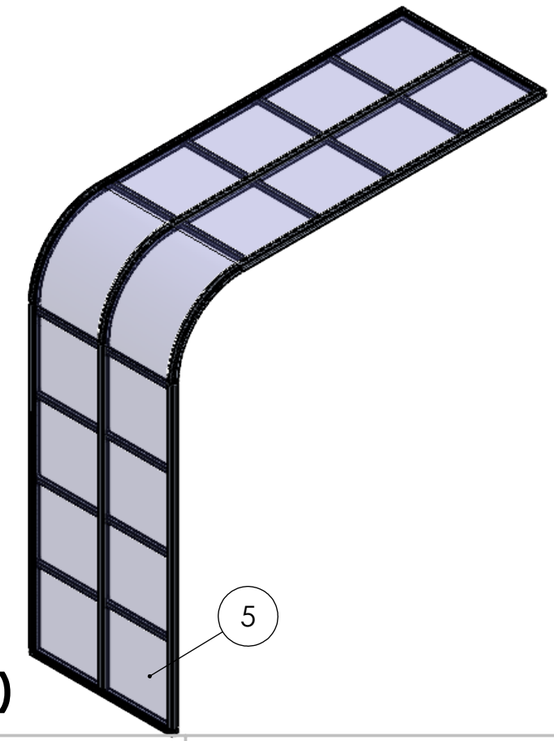


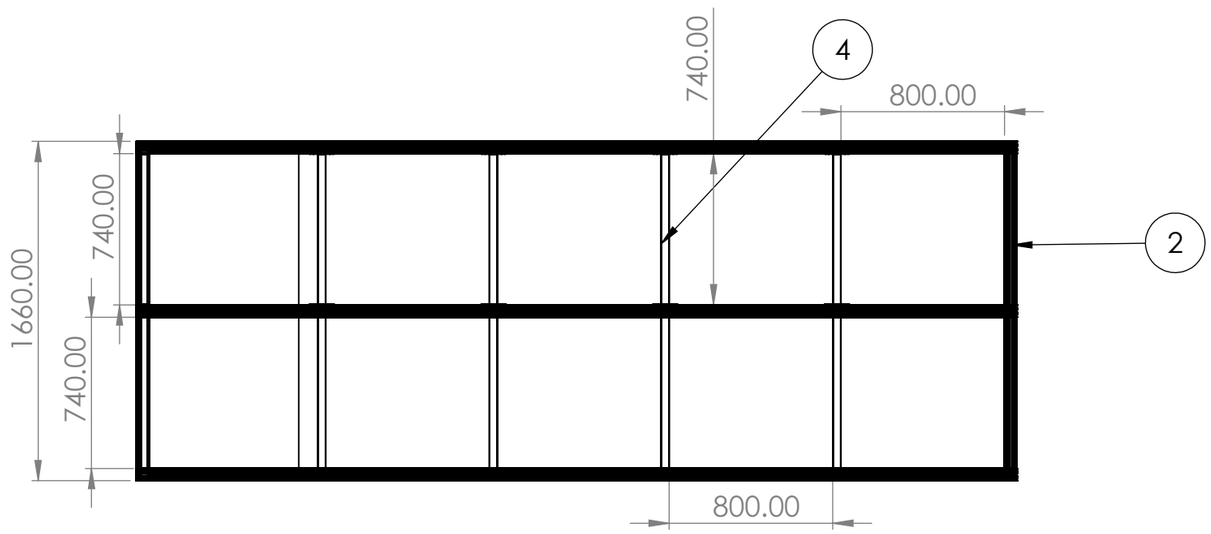



PANEL_01 (FIX PANEL)

TITLE - BALCONY ENCLOSER				NIHVA TECHNOLOGIES PVT.LTD.PUNE
DWG NO - NTPL263-PM			QTY - 1	Website - www.nihva.com
	NAME	SIGNATURE	DATE	PROJECT NO - NTPL263-PM
DRAWN	S.W		30-01-2025	PRODUCT - BALCONY ENCLOSURE
CHK'D	P.M.		30-01-2025	SITE LOCATION - MUMBAI
APPV'D	V.T.		30-01-2025	
if any queries contact - supportautomation@nihva.com				REVISION -
ALL DIMENSION ARE IN mm			A3	SCALE -

ITEM NO.	PART NUMBER	DESCRIPTION	QTY.
1	NEWREFSBR30 LUUOP BRG HSG MTG PLATE_1	(AL) 75X220X16 MM THK	6

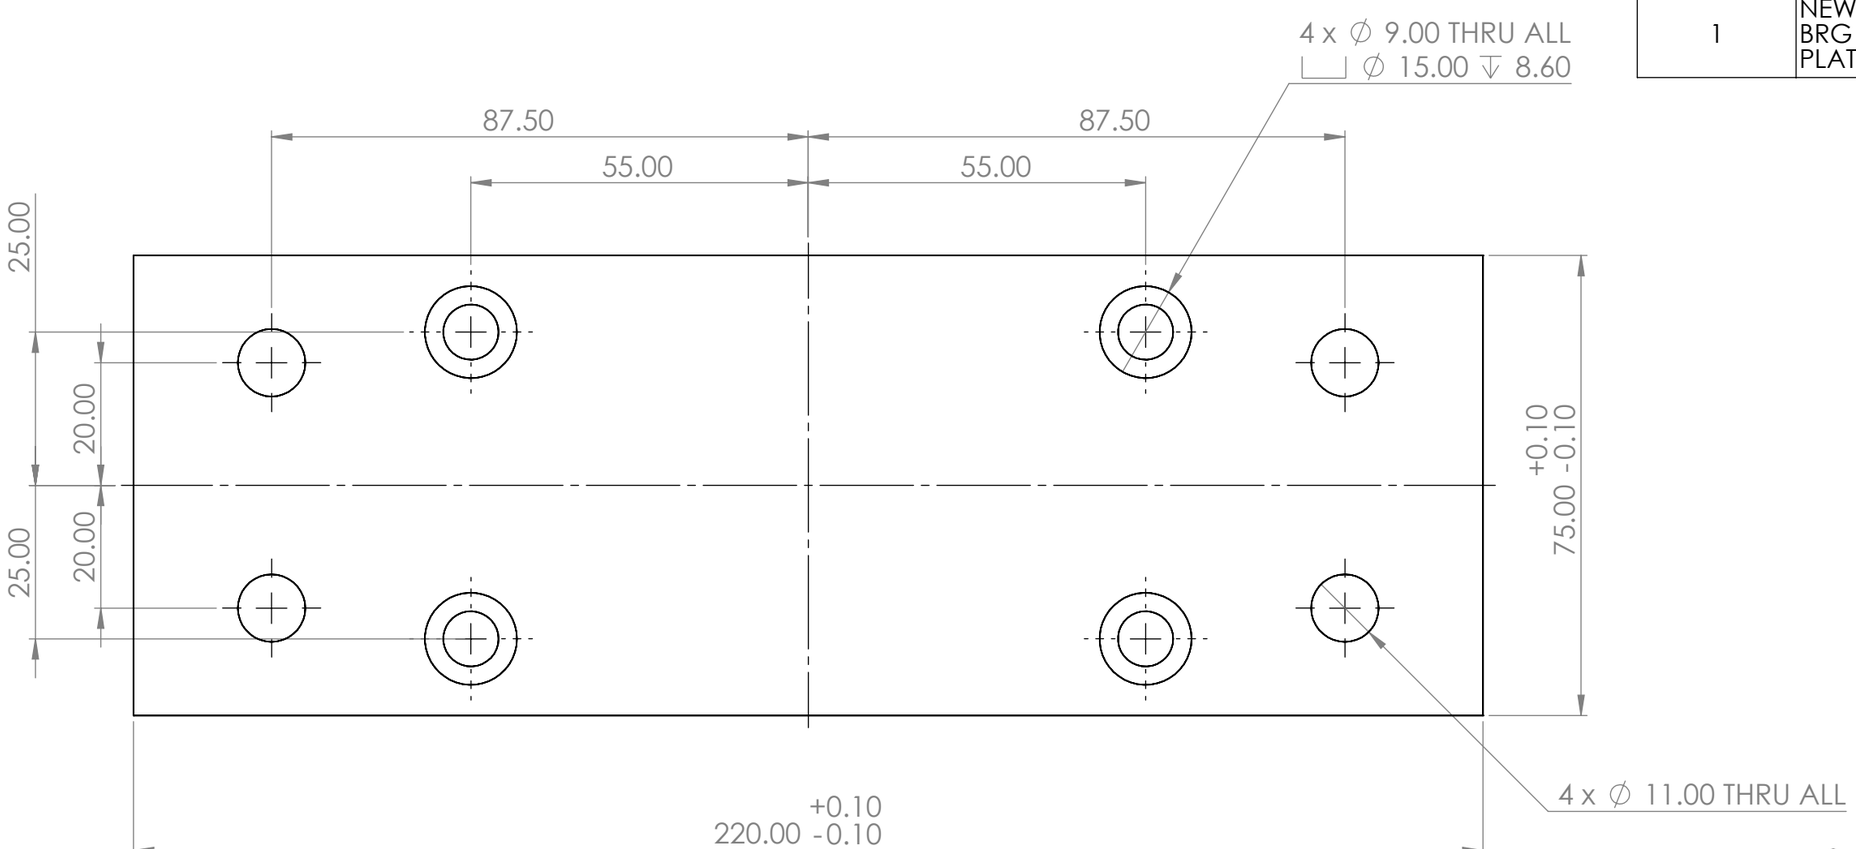


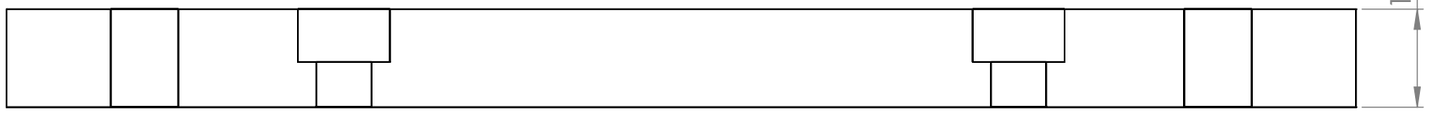


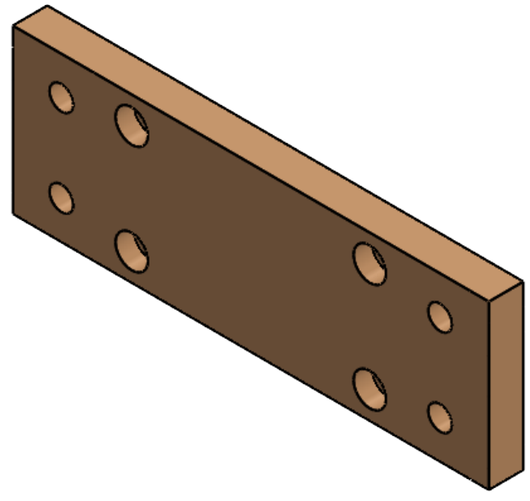

TITLE - BALCONY ENCLOSER				NIHVA TECHNOLOGIES PVT.LTD.PUNE
DWG NO - NTPL263-PM			QTY - 1	Website - www.nihva.com
	NAME	SIGNATURE	DATE	PROJECT NO - NTPL263-PM
DRAWN	S.W		30-01-2025	PRODUCT - BALCONY ENCLOSURE
CHK'D	P.M.		30-01-2025	SITE LOCATION - MUMBAI
APPV'D	V.T.		30-01-2025	
if any queries contact - supportautomation@nihva.com				REVISION -
ALL DIMENSION ARE IN mm			A3	SCALE - SHEET 8 OF 12


ITEM NO.	PART NUMBER	DESCRIPTION	QTY.
1	NEWPANEL_01REFSBR30 LUUOP BRG HSG MTG PLATE_2	(AL) 75X220X16 MM THK	6

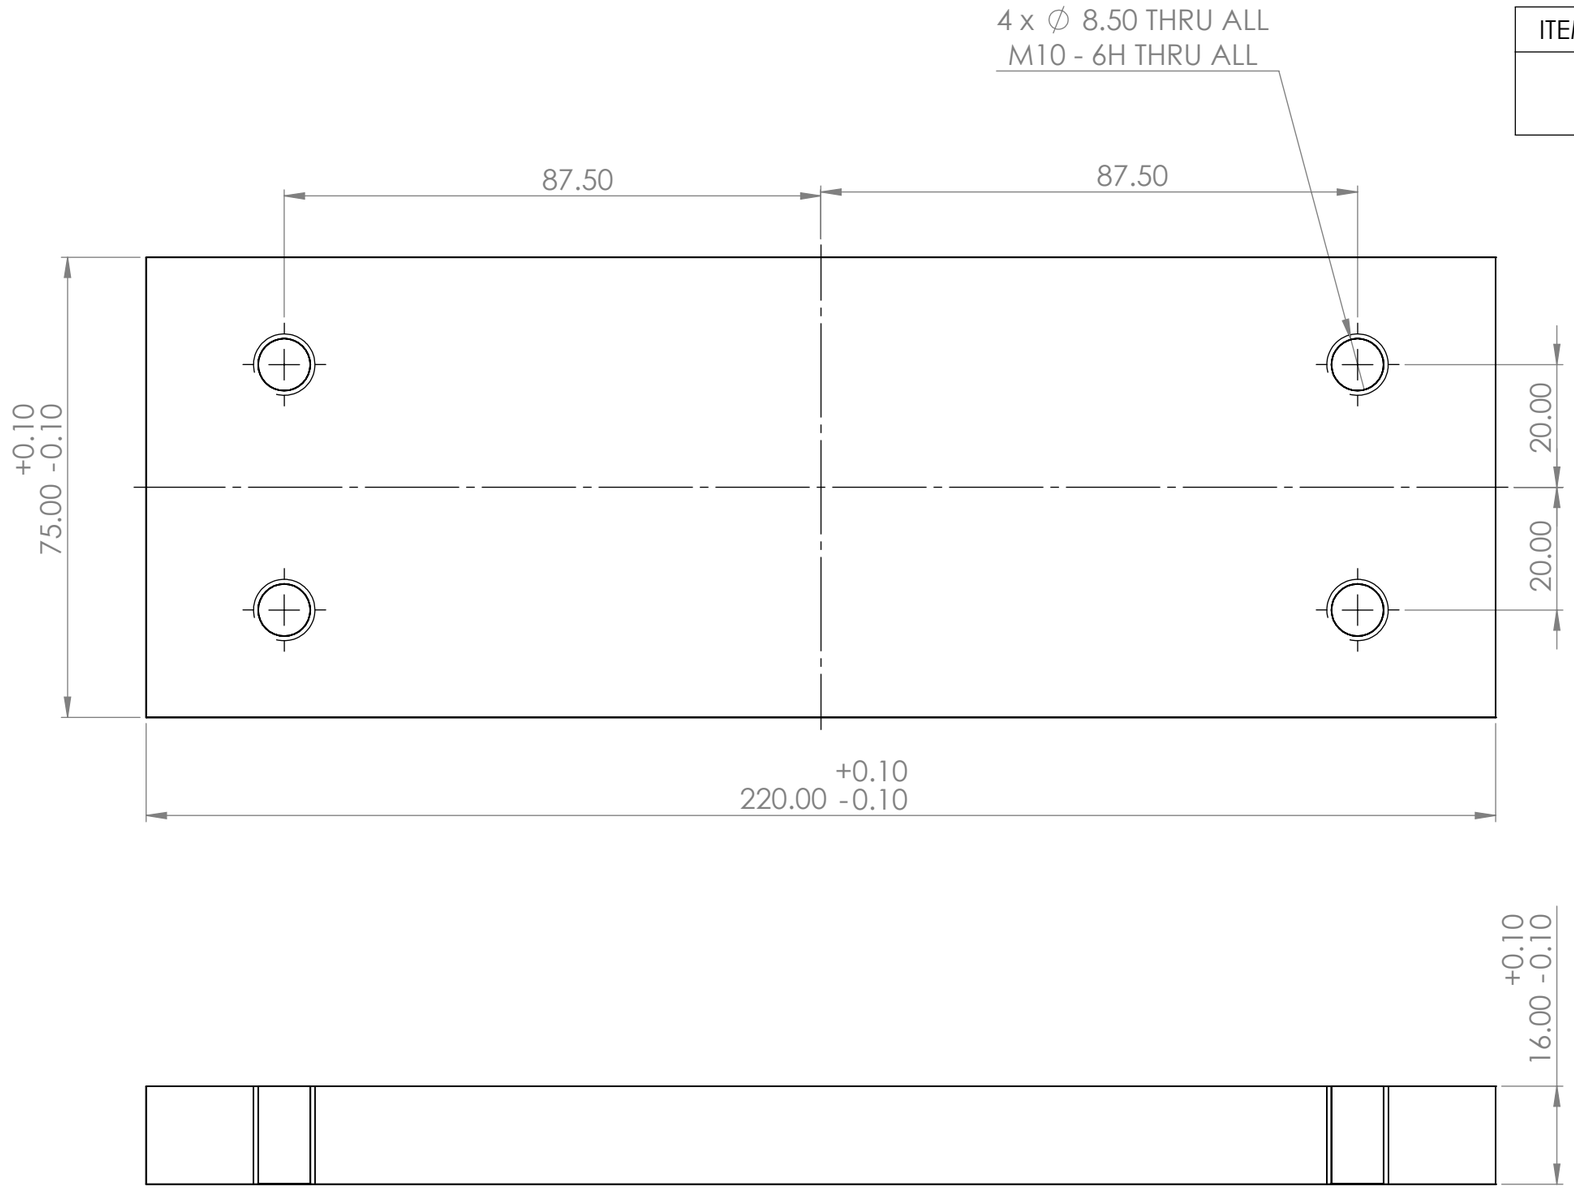


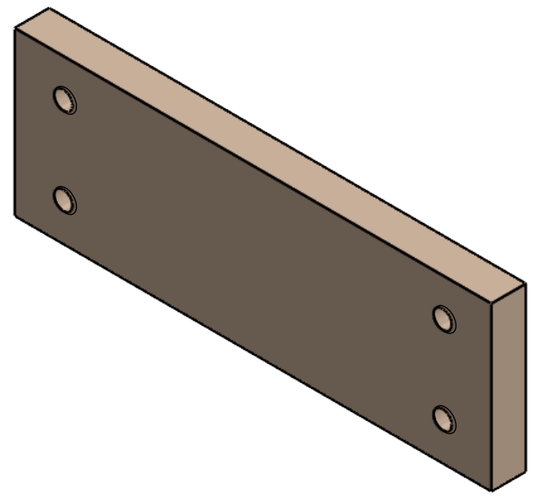


TITLE - BALCONY ENCLOSER				NIHVA TECHNOLOGIES PVT.LTD.PUNE
DWG NO - NTPL263-PM			QTY - 1	Website - www.nihva.com
	NAME	SIGNATURE	DATE	PROJECT NO - NTPL263-PM
DRAWN	S.W		30-01-2025	PRODUCT - BALCONY ENCLOSURE
CHK'D	P.M.		30-01-2025	SITE LOCATION - MUMBAI
APPV'D	V.T.		30-01-2025	
if any queries contact - supportautomation@nihva.com				REVISION -
ALL DIMENSION ARE IN mm			A3	SCALE -


ITEM NO.	PART NUMBER	DESCRIPTION	QTY.
1	AL Support tube SQ TUBE 40X40X1.5 MM L-734 MM	ALUMINIUM	50

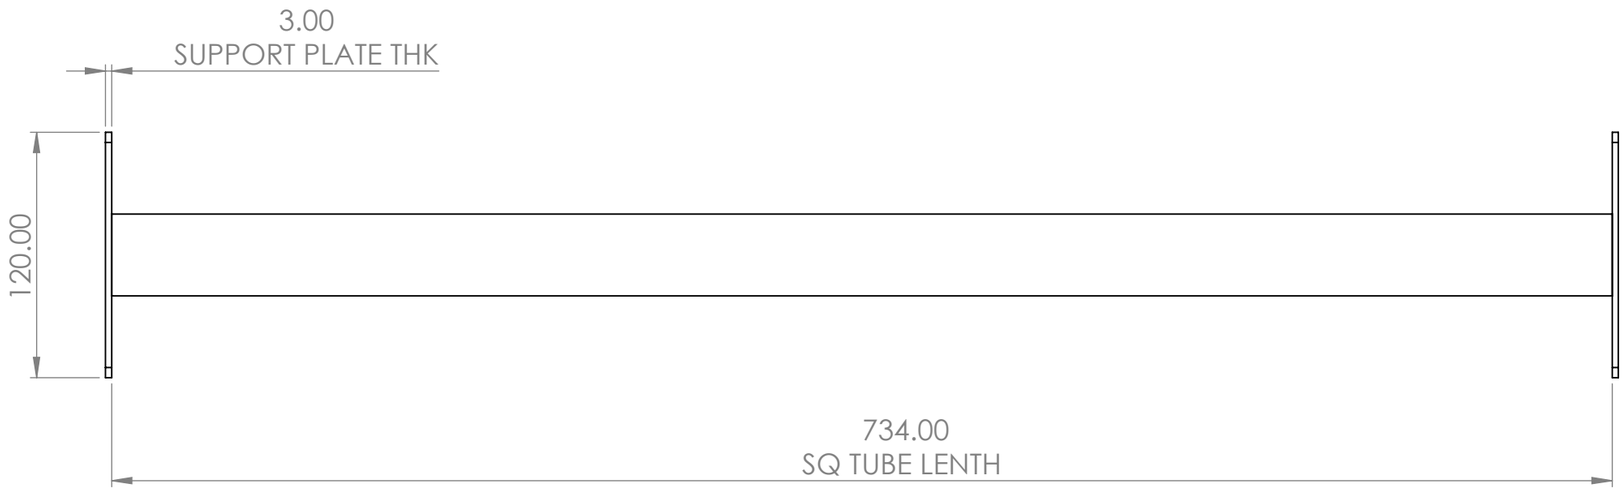


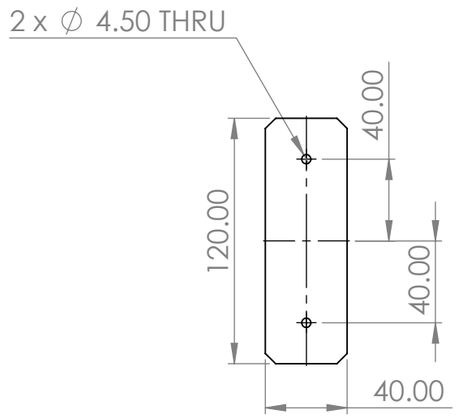

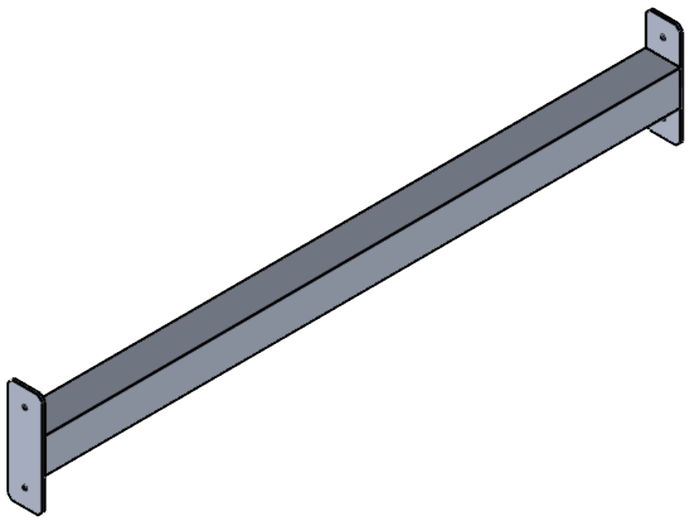



TITLE - BALCONY ENCLOSER				NIHVA TECHNOLOGIES PVT.LTD.PUNE Website - www.nihva.com
DWG NO - NTPL263-PM			QTY - 1	
	NAME	SIGNATURE	DATE	PROJECT NO - NTPL263-PM
DRAWN	S.W		30-01-2025	PRODUCT - BALCONY ENCLOSURE
CHK'D	P.M.		30-01-2025	SITE LOCATION - MUMBAI
APPV'D	V.T.		30-01-2025	
if any queries contact - supportautomation@nihva.com				REVISION -
ALL DIMENSION ARE IN mm			A3	SCALE - SHEET 10 OF 12

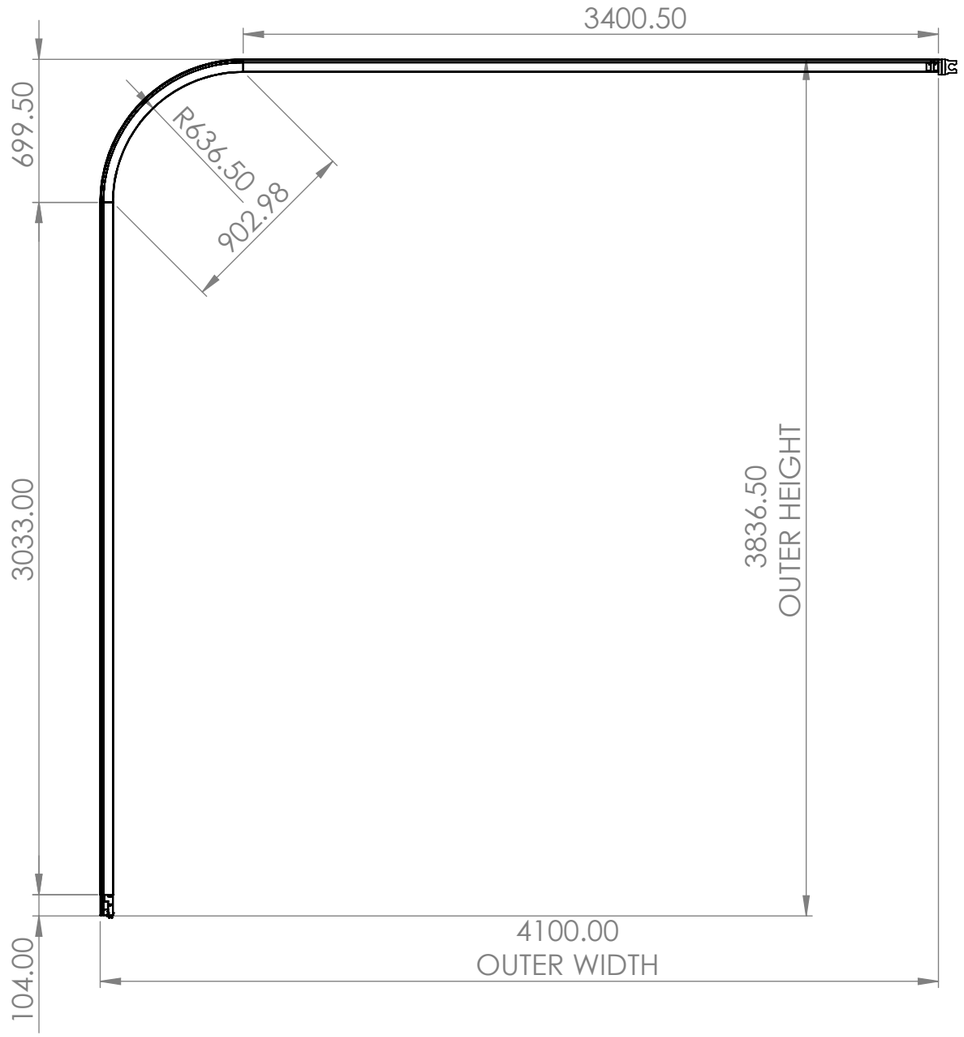

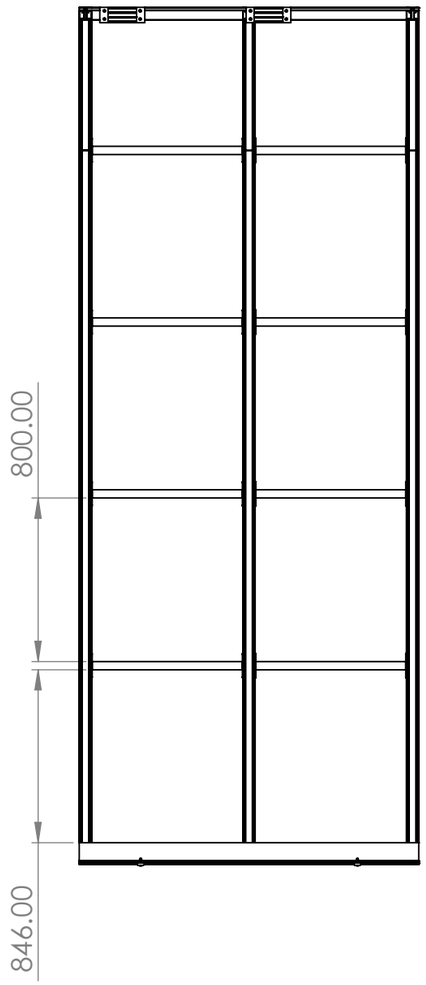


ITEM NO.	PART NUMBER	DESCRIPTION	QTY.
1	NEWPANEL_01FIX PANEL PROFILE _ 01	GNT_006	3
2	NEWPANEL_01SBR BEARING FITTED PROFILE	GNT_006	1
3	NEWPANEL_01GNT_007 TRACK	GNT_007	1
4	NEWPANEL_01REFSBR30 LUUOP (SBR BEARING BLOCK)	STD	2
5	SBR GUIDE RAIL MTG PLATE_01	(AL) 75X220X16 MM THK	2
6	NEWPANEL_01REFSBR30 LUUOP BRG HSG MTG PLATE_2	(AL) 75X220X16 MM THK	2
7	NEWPANEL_01NYLON WHEEL	NYLON WHEEL ∅65X18 WITH BEARING	2
8	AL Support tube SQ TUBE 40X40X1.5 MM L-734 MM	ALUMINIUM	16
9	polycarbonate sheet panel two	PC	1

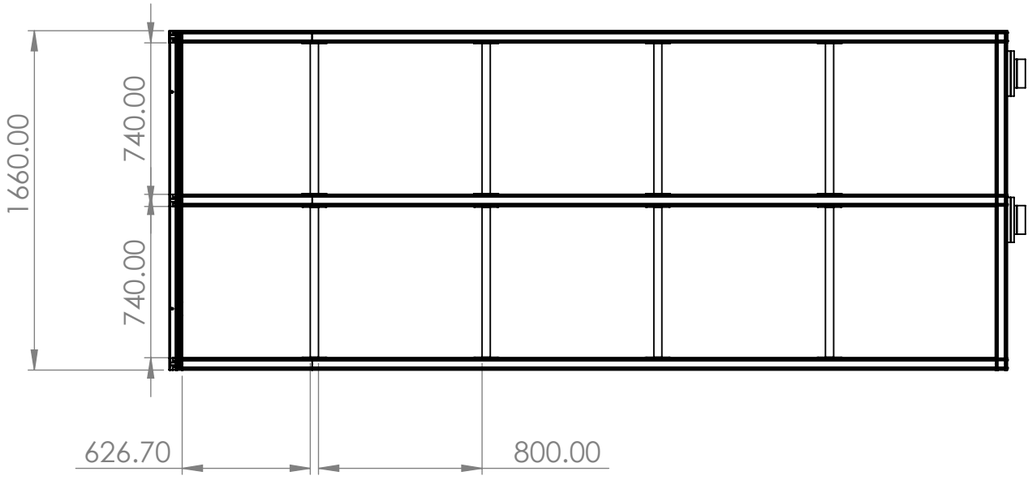

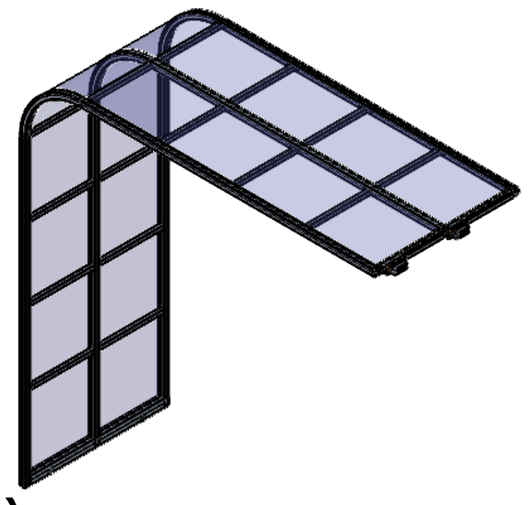

PANEL_02 (MIDDLE PANEL)

TITLE - BALCONY ENCLOSER				NIHVA TECHNOLOGIES PVT.LTD.PUNE
DWG NO - NTPL263-PM			QTY - 1	Website - www.nihva.com
	NAME	SIGNATURE	DATE	PROJECT NO - NTPL263-PM
DRAWN	S.W		30-01-2025	PRODUCT - BALCONY ENCLOSURE
CHK'D	P.M.		30-01-2025	SITE LOCATION - MUMBAI
APPV'D	V.T.		30-01-2025	
if any queries contact - supportautomation@nihva.com				REVISION -
ALL DIMENSION ARE IN mm			A3	SCALE - SHEET 11 OF 12

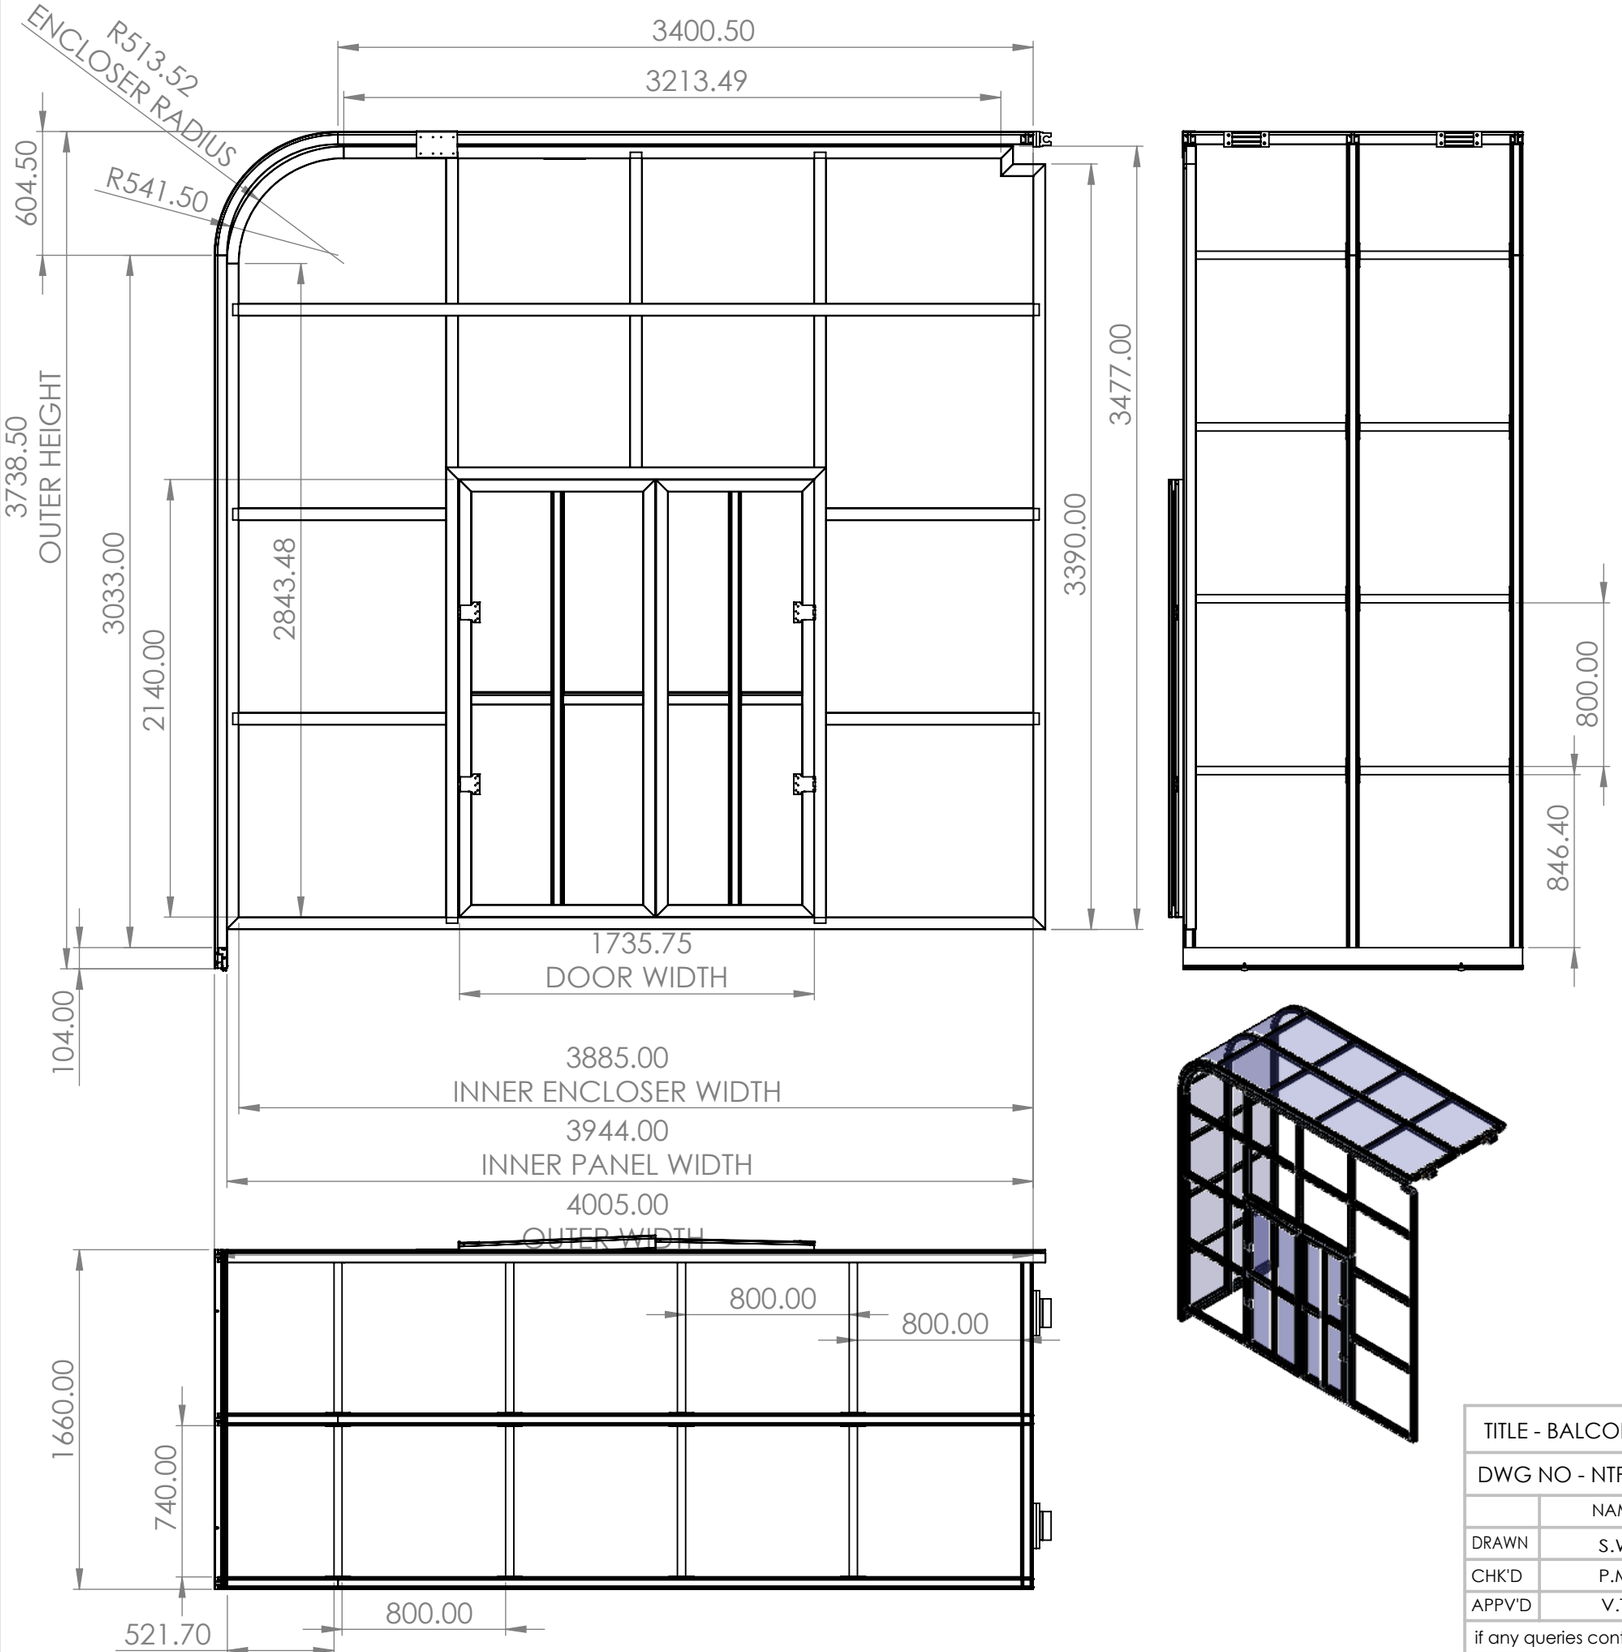

ITEM NO.	PART NUMBER	DESCRIPTION	QTY.
1	NEWPANEL_02PANEL_01FIX PANEL PROFILE _01		3
2	NEWPANEL_02PANEL_01SBR BEARING FITTED PROFILE		1
3	NEWPANEL_02PANEL_01GNT_007 TRACK		1
4	NEWPANEL_02PANEL_01REFSBR30 LUUOP (SBR BEARING BLOCK)	STD	2
5	STRAIGHT PLATE	(AL) 75X220X16 MM THK	2
6	NEWPANEL_02PANEL_01REFSBR30 LUUOP BRG HSG MTG PLATE_2	(MS) 75X220X16 MM THK	2
7	NEWPANEL_02PANEL_01NYLON WHEEL	NYLON WHEEL ∅65X18	2
8	encloser		1
9	AL Support tube SQ TUBE 40X40X1.5 MM L-734 MM	ALUMINIUM	16
10	polycarbonate sheet panel three		1
11	HINGE		4
12	HINGE FEMAIL		4
13	DOOR		1
14	DOOR_02		1
15	L BRACKET		1
16	L BRACKET _01		1

TITLE - BALCONY ENCLOSER				NIHVA TECHNOLOGIES PVT.LTD.PUNE
DWG NO - NTPL263-PM			QTY - 1	Website - www.nihva.com
	NAME	SIGNATURE	DATE	PROJECT NO - NTPL263-PM
DRAWN	S.W		30-01-2025	PRODUCT - BALCONY ENCLOSURE
CHK'D	P.M.		30-01-2025	SITE LOCATION - MUMBAI
APPV'D	V.T.		30-01-2025	
if any queries contact - supportautomation@nihva.com				REVISION -
ALL DIMENSION ARE IN mm			A3	SCALE - SHEET 12 OF 12