

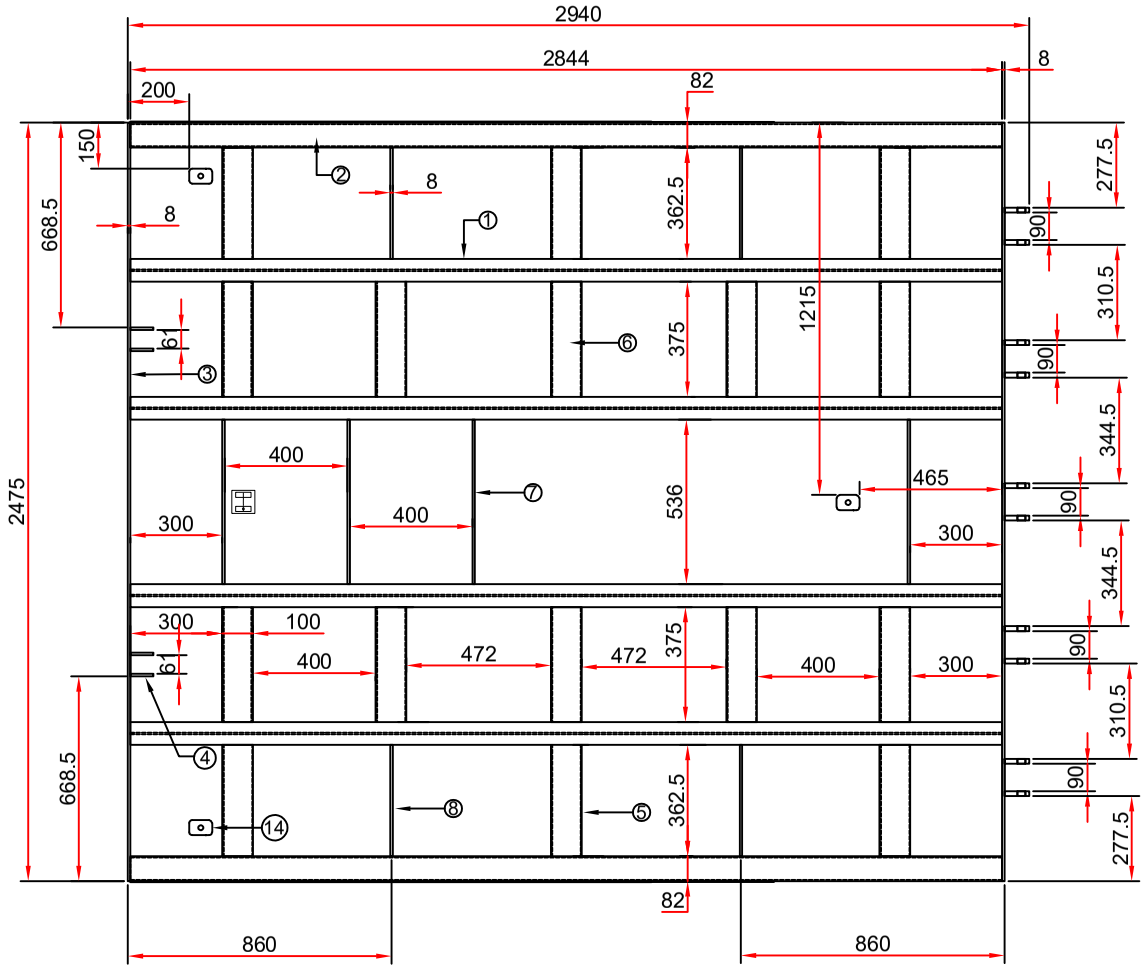


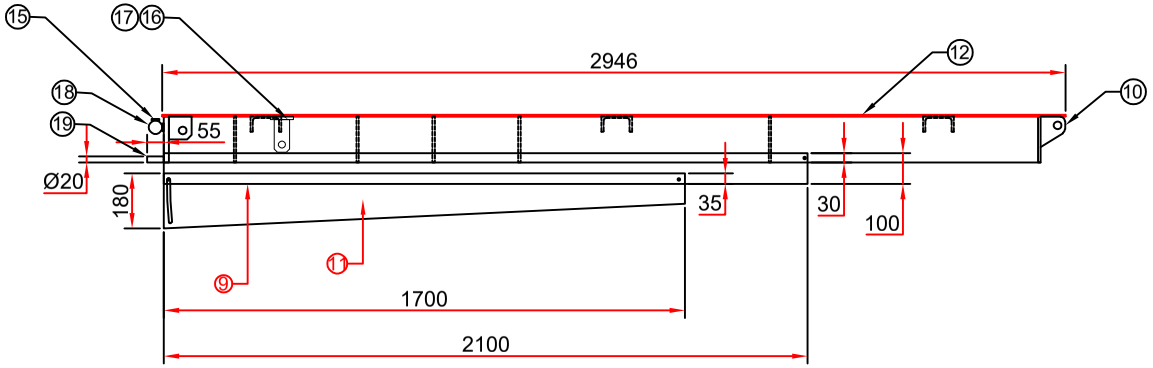

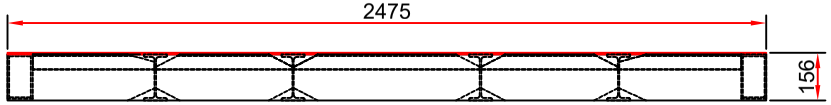

BOM			
SL NO.	DESCRIPTION	SPECIFICATION	QTY
1	ISMB	150X75X2844L	4NOS
2	MS RECT.TUBE	145X82X2844X4.8THK	2NOS
3	MS FLAT	150X8X2475L	2NOS
4	CYLINDER MTG BKT	75X75X16THK	4NOS
5	C CHANNEL	100X50x5X362.5L	6NOS
6	C CHANNEL	100X50x5X375L	10NOS
7	MS FLAT	100X8X536L	3NOS
8	MS FLAT	100X8X362.5L	4NOS
9	L BEND	100X2100X1.6THK	2NOS
10	HOLDING BKT	100X80X16THK	10NOS
11	SIDE COVER	180X1700X1.6THK	2NOS
12	CHEQ.SHEET	2475X2946X6THK	1NO
13	EYE BOLT	M16XSTD WITH NUT	3NOS
14	EYE BOLT MTNG BKT	50X75X16	3NOS
15	MS FLAT	25X5X100	20NOS
16	MS BRACKET	50X106X16	2NOS
17	MS FLAT	75X10X115	1NO
18	MS BUSH	OD45X26ID	20NOS
19	BRIGHT BAR	24DIAX1970MM	1NO
20	LIP PLATE	2500X400X16	1NO
21	ROUND BAR	Ø20X55L	2NOS
22	BRIGHT BAR	24DIAX2500MM	1NO

This drawing & design is the property of NIHVA TECHNOLOGIES. Not to be sold or copied to any other concern.

TITLE: DECK FRAME

NIHVA TECHNOLOGIES PVT. LTD.

	NAME	DATE	SIGN
DRAWN	SUJATA	11/02/2023	
CHECK	A.K	11/02/2023	
APPRD.	V.T	11/02/2023	

If any queries contact : design1@nihva.com

ALL DIMENSION ARE IN mm

CLIENT - Aegis Infrasolutions(India) Pvt Ltd

LOCATION - Pune

PRODUCT - Dock leveler

DWG NO:-NIHVA/22-23/MFG/0111 | REV- 0

SCALE: NTS | SCALE:-- 1:1 | SHEET: 01 OF 01

Rev No.	Revision	Date	Revised By