


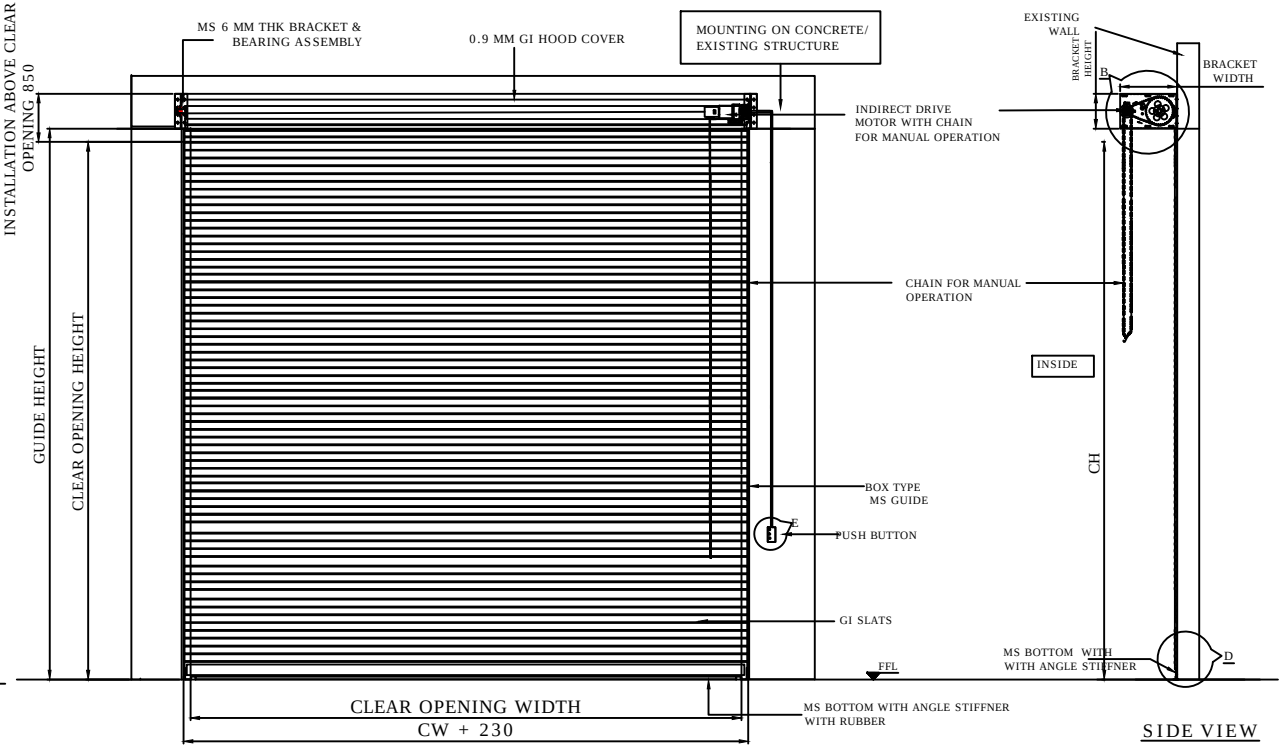


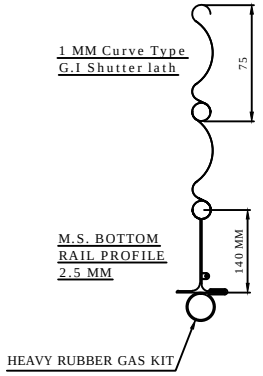


DETAILS : D

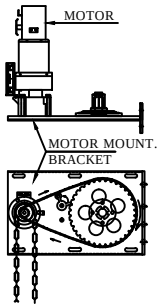


DETAILS : A & B

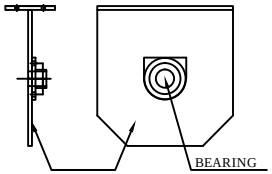

DETAILS : C

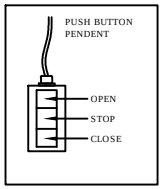

DETAILS : E

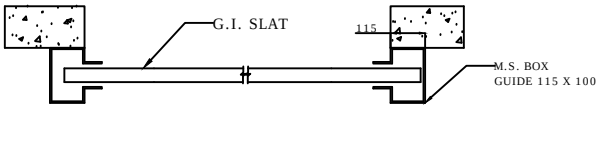

RAL CODE	SHADE	COLOUR
RAL 9001	CREAM	
RAL 9002	GREY WHITE	
RAL 9010	PURE WHITE	
RAL 5002	ULTRAMARINE BLUE	
RAL 7035	LIGHT GREY	
RAL 7001	SILVER GREY	

SR NO	CLEAR OPENING WIDTH(CW)	CLEAR OPENING HEIGHT(CH)	QTY	LOCATION	MOTOR SIDE (RH/LH SEEN FROM INSIDE)	MOUNTING AREA (STANDARD-INSIDE)	RAL SHADE
2	6000	5700	2				
1	3000	4000	6				

NOTES-

1. IF REQUIRED M.S. STRUCTURE ,FITTING & ALL CIVIL WORK IS IN CLIENT SCOPE.
2. KINDLY REFER NIHVA STANDARD AVAILABLE ATTACHED RAL SHADE & CONFIRM RAL SHADE FOR POWDER COATING.INFORM IF OTHER ANY.
3. KINDLY CONFIRM INSTALLATION LOCATION , MOTOR SIDE (RH -STANDARD) , SURFACE MOUNTING SURFACE & INSIDE/OUTSIDE(INSIDE-STANDARD) .
4. FREE SPACE OF 850 MM IS REQUIRED ABOVE CLEAR OPENING HEIGHT .

This drawing & design is the property of NIHVA TECHNOLOGIES. Not to be sold or copied to any other concern.

TITLE- GI SLAT MOTORIZED ROLLING SHUTTER

NIHVA TECHNOLOGIES PVT. LTD.

NIHVA TECHNOLOGIES PVT. LTD. PUNE
Tel : 020 66304033
Email:- info@nihva.com
Website:- www.nihva.com

	NAME	SIGN	DATE
DRAWN	SIDDHESHWAR		8.1.2021
CHECK	SIDDHESHWAR		8.1.2021
APPRD.			

CLIENT - RMK INFRA

PROJECT -

SITE LOCATION - PUNE

If any queries contact : projectsupport@nihva.com

DWG. NO. : NIHVA/20-21/0124 REV- R00

ALL DIMENSION ARE IN mm

SCALE: NTS WT: SHEET: