

NOTE :
1. DOOR HINGES : GEZE MAKE.
2. DOOR CLOSER : GEZE MAKE.
3. DOOR PANIC BAR : YELE MAKE.

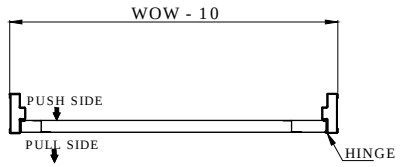


TOP VIEW

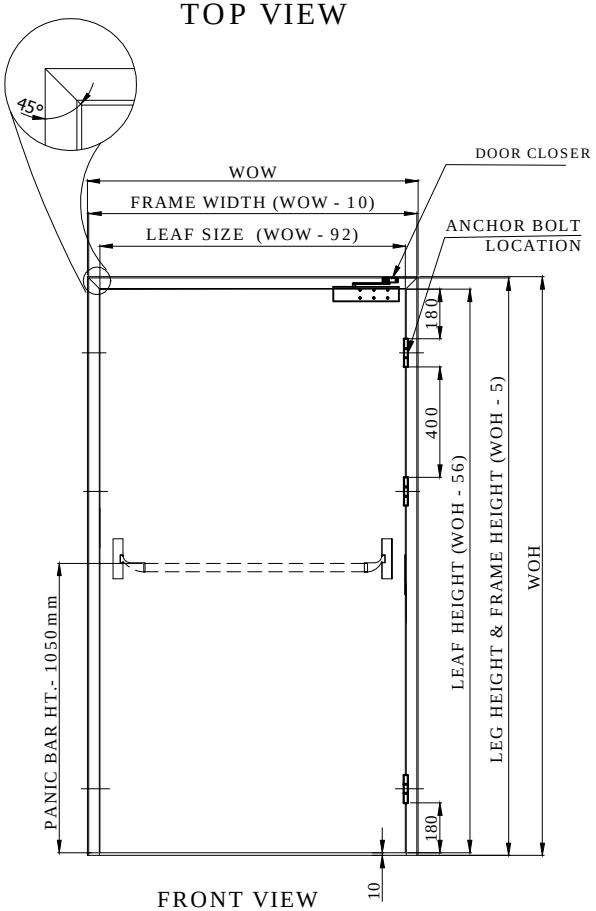


FRONT VIEW




SIDE VIEW
SECTION A-A'

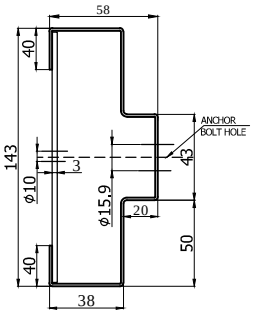

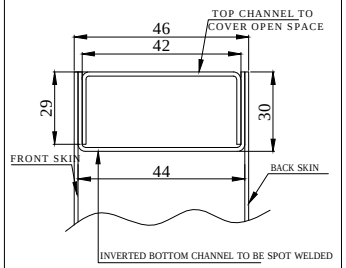

DOOR TOP SECTION DETAIL

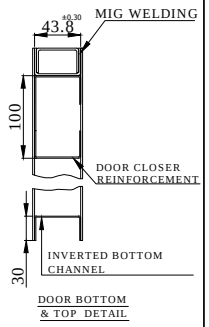

DOOR BOTTOM & TOP DETAIL

SR. NO	WALL OPENING WIDTH	WALL OPENING HEIGHT	QTY	RAL	LOCATION	HARDWARE
02	1200	2100	01	9002		Hinges , Panic Bar, External Trim
01	1200	2100	13	9002		Hinges , Panic Bar, External Trim

TOLERANCE - ±05mm

This drawing & design is the property of NIHVA TECHNOLOGIES. Not to be sold or copied to any other concern.

TITLE	NAME	SIGN	DATE
SINGLE LEAF STEEL DOOR			
DRAWN	P.A		08.01.2020
CHECK	G.J		08.01.2020
APPRD.			

NIHVA TECHNOLOGIES PVT. LTD.
NIHVA TECHNOLOGIES PVT. LTD. PUNE
Tel : 020 66304033
Email:- info@nihva.com
Website:- www.nihva.com

CLIENT -
PROJECT -
SITE LOCATION -

If any queries contact : design@nihva.com
DWG. NO. : NIHVA/19-20/VDR/275 | REV- R00
ALL DIMENSION ARE IN mm
SCALE: NTS | WT: | SHEET: 01 OF 01