
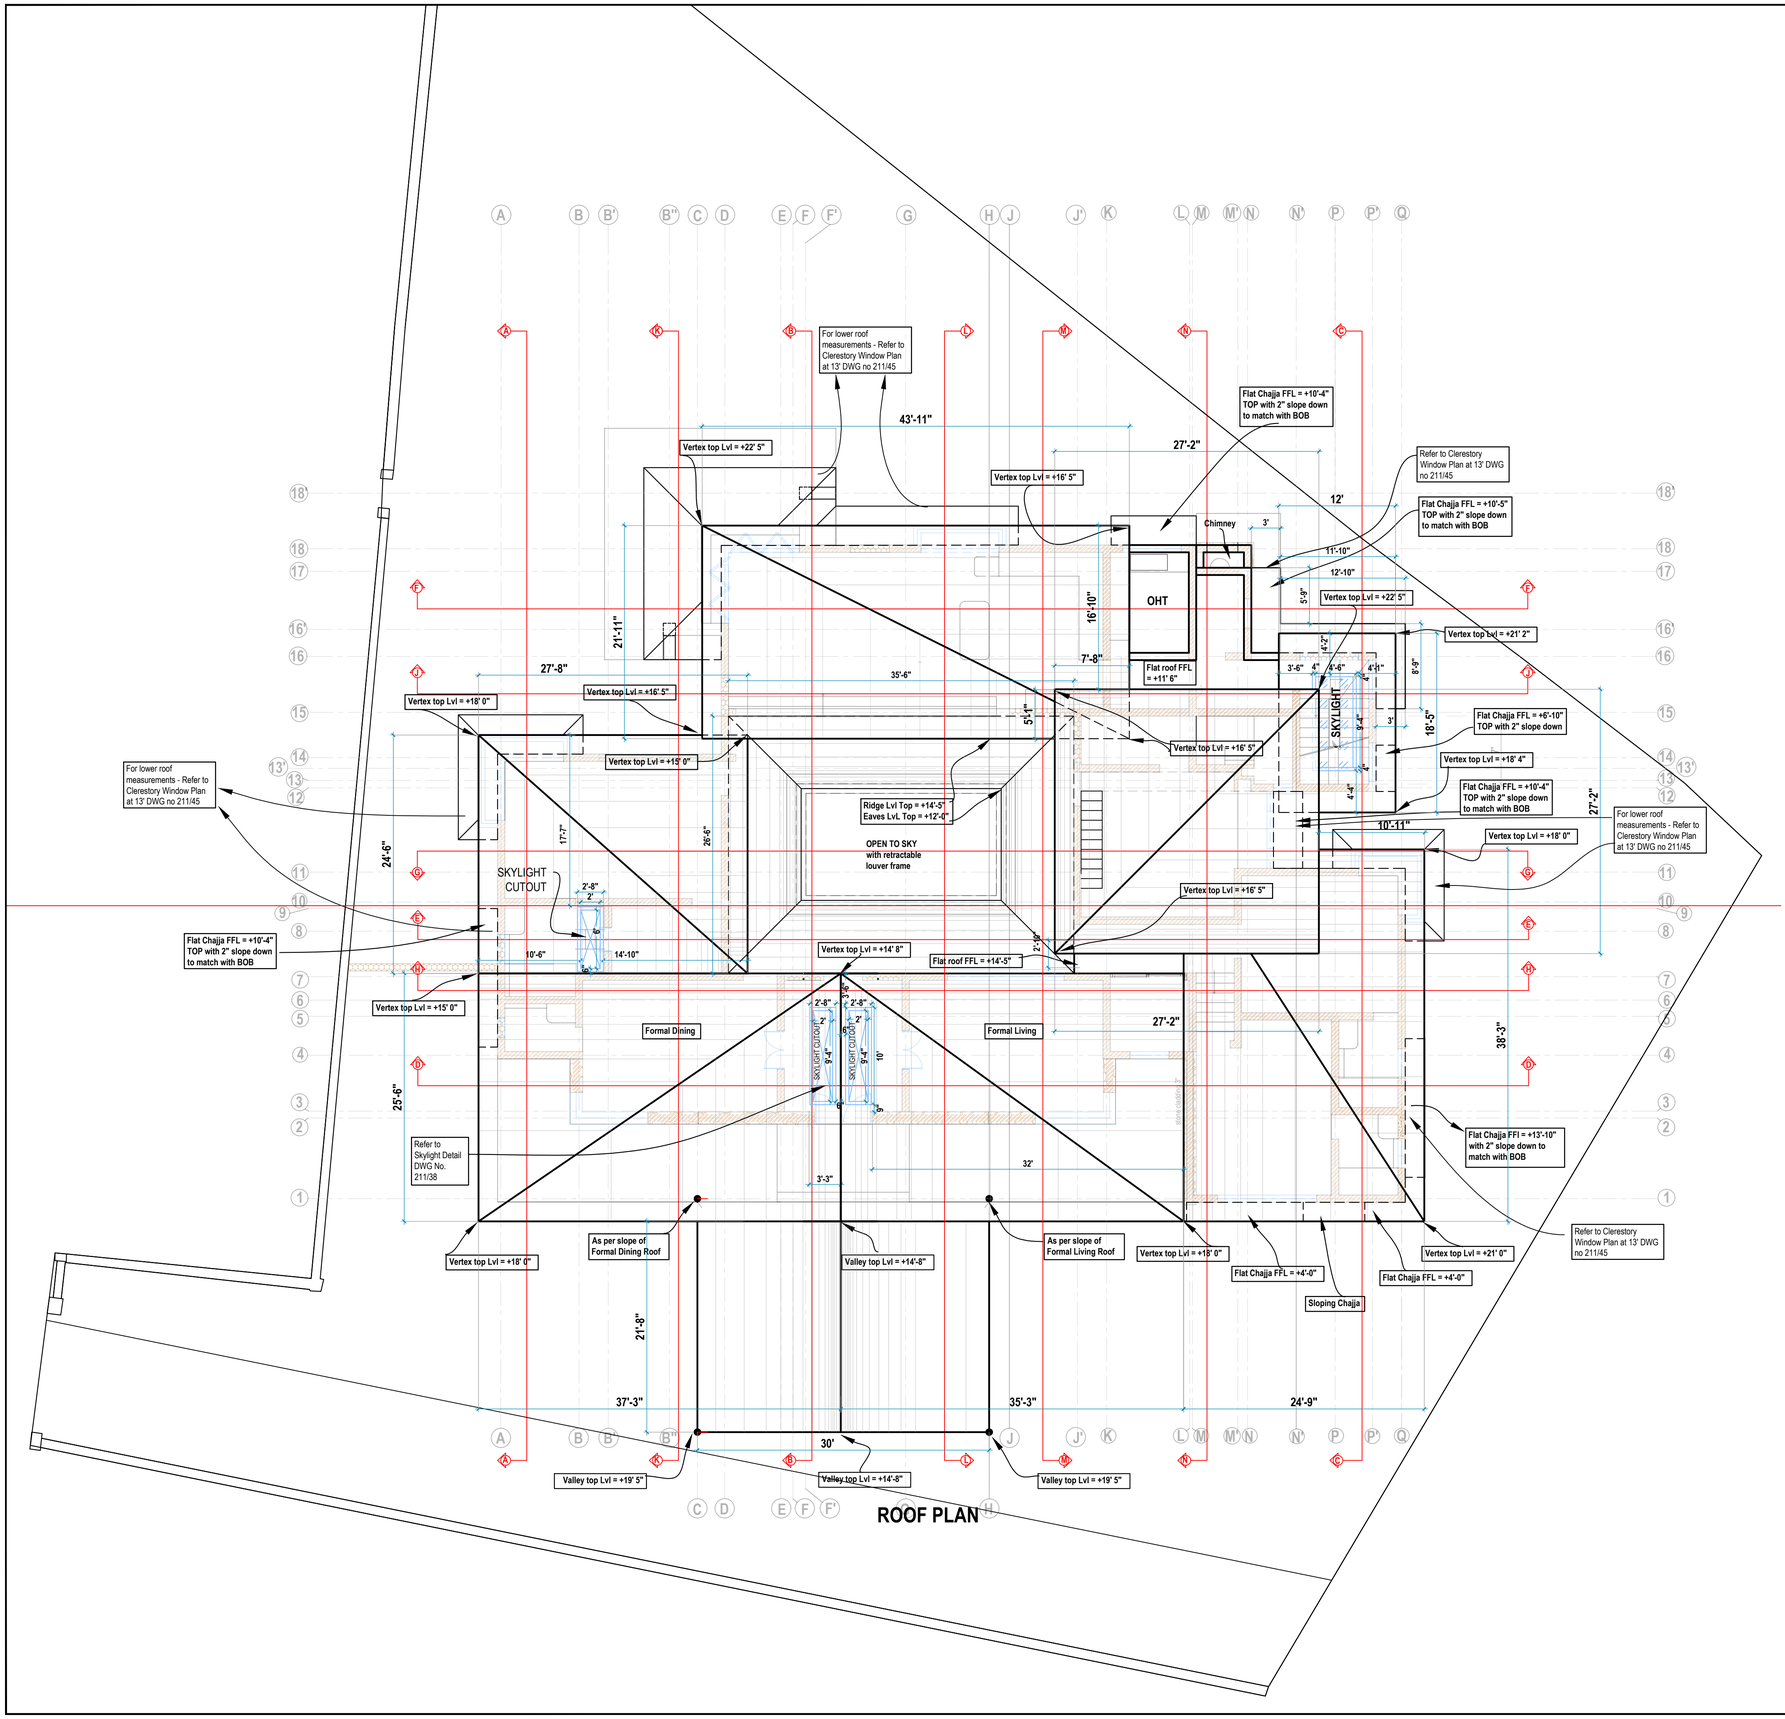


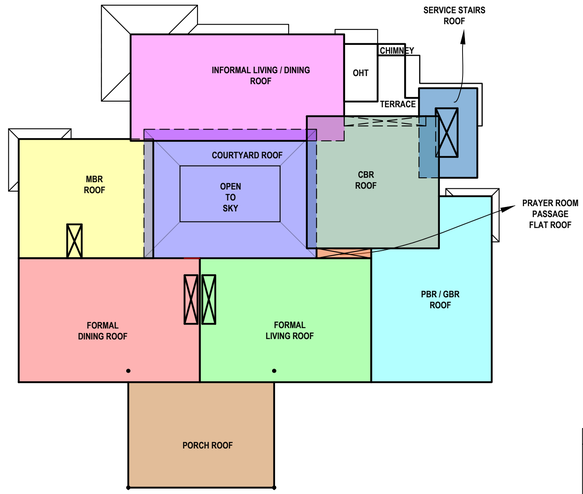

- Porch ROOF = 30'-0" X 21'-8"
- Formal Dining ROOF = 37'-3" X 25'-6"
- Formal Living ROOF = 35'-3" X 25'-6"
- MBR ROOF = 27'-8" X 24'-6"
- Courtyard ROOF = 35'-6" X 26'-6"
- Informal Living / Dining ROOF = 43'-11" X 21'-11"
- Service Staircase ROOF = 12'-0" X 18'-5"
- CBR ROOF = 27'-2" X 27'-2"
- PBR/GBR ROOF = 24'-9" X 38'-3"
- Prayer Room Passage Flat ROOF = 11'-3" X 2'-0"

PLEASE NOTE:
This drawing is the copyright of Design Harmony.
This drawing should not be reprinted or copied without prior permission of Design Harmony for any purpose - academic, personal or commercial.
All measurements are to be read only.
Any intended deviations at site from details in drawing need to be approved by Design Harmony.
Any noted discrepancies from drawing to site status need to be brought to the notice of Design Harmony immediately.

S.NO.	REVISION	DATE
R1	i.Service area roof updated as per changes in plan ii.Courtyard roof extended	17-04-21
R2	i.Sloped roofs of Bay window's top matched till beam top ii.The overhang of 2ft on Northside and Westside and Southside for the formal living roof, keeping the vertex height the same iii.A flat roof extention above the CBR window upto tie beamtop level	26-05-21
R3	Sloped roofs at Formal Living and Formal Dining meet at common edge now Informal Living and CBR Roof Top Vertex corrected to 22'-5" Service Area Sloped Roof added	26-06-21
R4	Change to portico roof	11-08-21
R5	Removal of courtyard passage skylight Revision of foyer skylight	12-10-21

PROJECT
PROPOSED RESIDENCE FOR MRS. HIBA AND MR.MOHAMAD SHAKEER AT MANGALORE.

DRAWING TYPE
GFC

DRAWING TITLE
Roof Plan

Dwg no.	211/gfc/02/R5
Date	30-01-2021
Drawn By	Shrey

POETRY OF SPACE
design harmony
Sustainable Architecture I Interiors I Landscape
Lake View Farm
Siddhapura, Bengaluru - 560066
+919886669602 jaya@designharmony.in