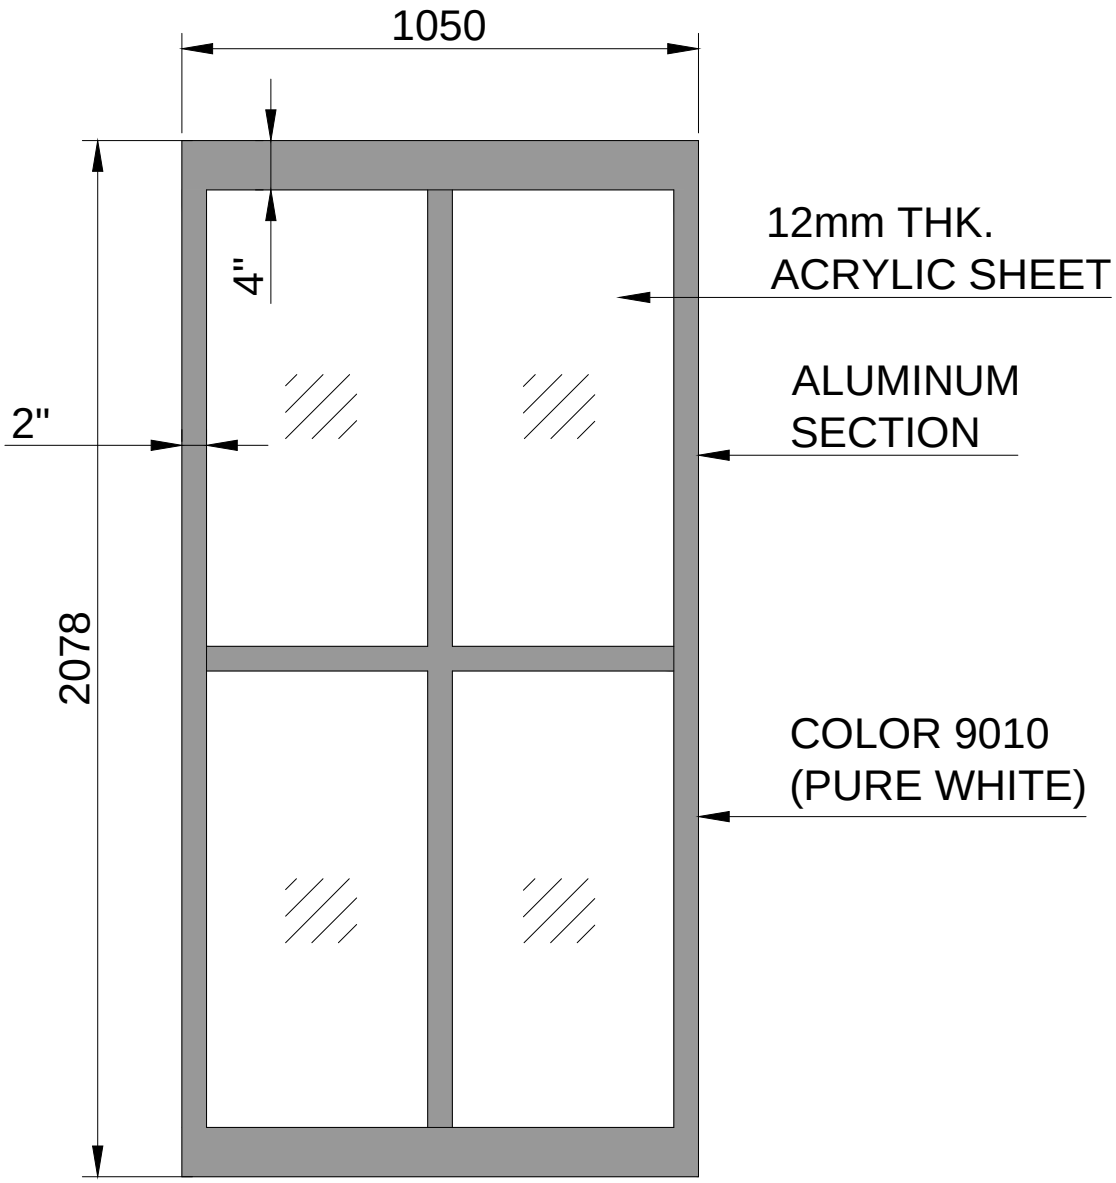

REV NO	DATE	DESCRIPTION
REV 0	08-11-2017	INITIAL DRAWING
REV 1	21-11-2017	HEIGHT OF DOOR REVISED
REV 2	22-12-2017	HEIGHT OF DOOR REVISED FROM 2105 TO 2078.

This drawing & design is the property of NIHVA TECHNOLOGIES. Not to be sold or copied to any other concern.

TITLE

SLIDING DOOR LEAF

CLIENT APPROVAL

ALL DIMENSION ARE IN mm

	NAME	SIGN	DATE
DRAWN	OMKAR		08/11/17
CHECK	SHEKHAR		08/11/17
APPRD.	SHEKHAR		08/11/17
MFG			
Ref. No.			

NIHVA TECHNOLOGIES PVT. LTD.

NIHVA TECHNOLOGIES PVT. LTD. PUNE
Tel : 020 66304033
Email:- info@nihva.com
Website:- www.nihva.com

CLIENT -

PROJECT -

SITE -

DWG. NO. -NIHVA/17-18/VDR/0176/R02 | REV-02

SCALE: NTS | WT: | SHEET: 01 OF 01

If any queries contact : projects@nihva.com