


DRAWING

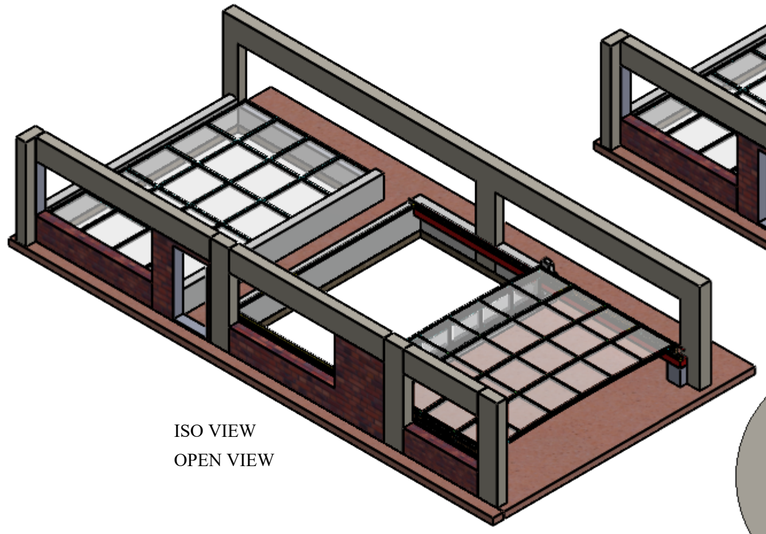


ISO VIEW
OPEN VIEW

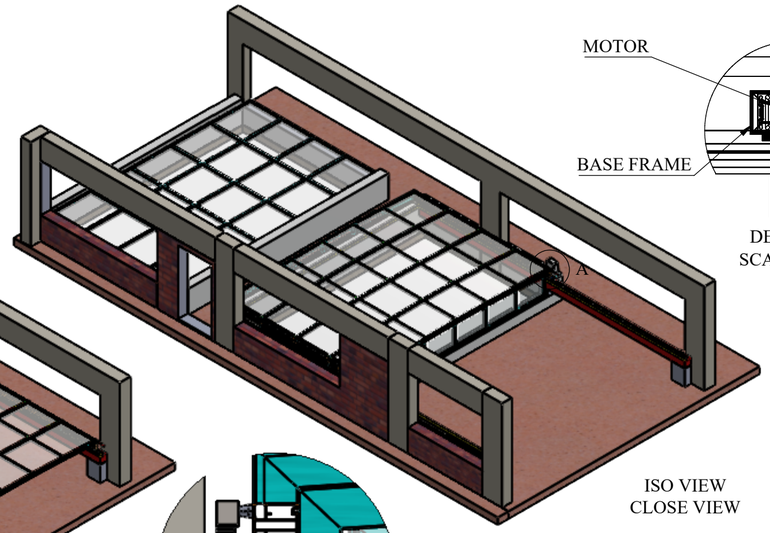


ISO VIEW
CLOSE VIEW

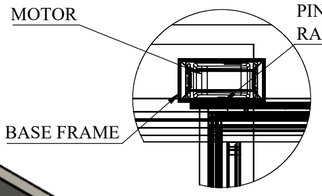



DETAIL B
SCALE 1 : 20

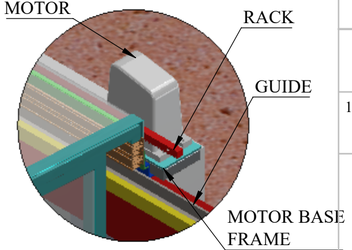



DETAIL A
SCALE 1 : 16

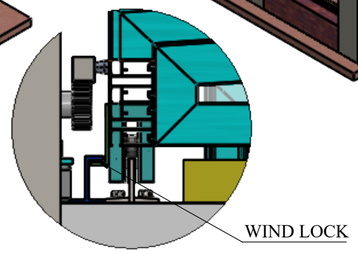



DETAIL D
SCALE 1 : 6

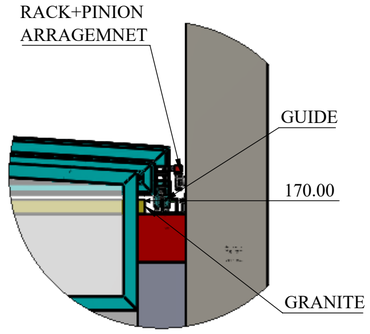



DETAIL C
SCALE 1 : 18

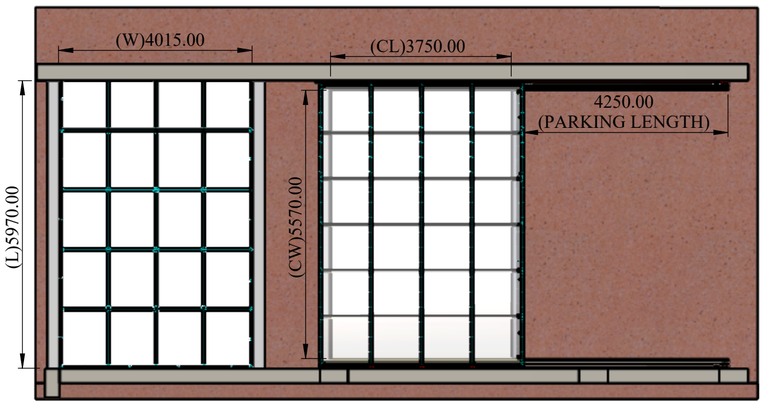



T.V.

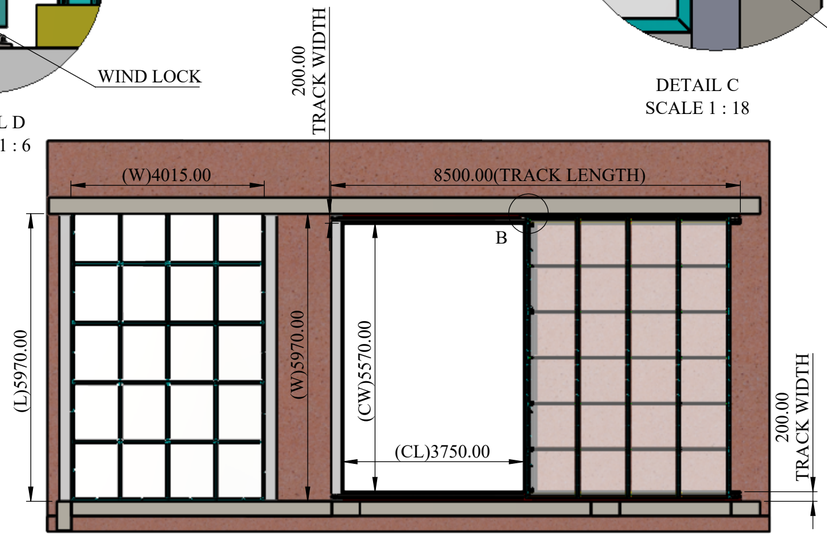


T.V.

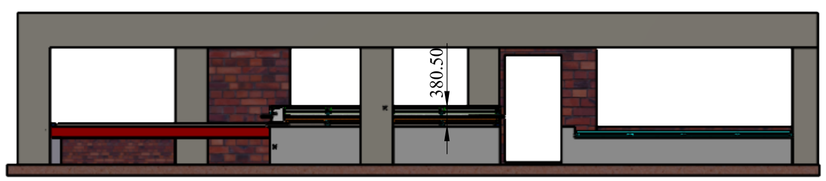


S.V.

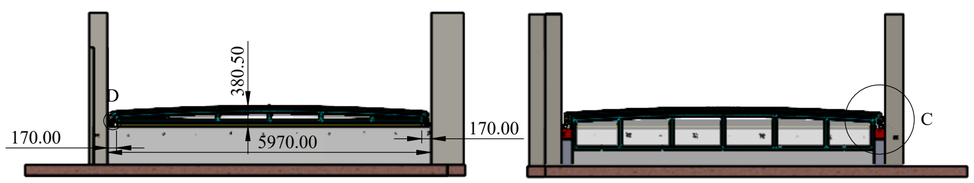


F.V.

B.V.

| REV DESCRIPTION | DATE | REV NO |
|---|---|---|
| | 24-09-2026 | REV 00 |
| 1. | | |

NOTE :

GA DRAWING:
THIS DRAWING IS ONLY FOR CLIENT APPROVAL.
FIX ROOF WEIGHT - 600 KG.
RECTRACTABLE ROOF SYSTEM WEIGHT - 800KG.

SPECIAL INSTRUCTION'S :

This drawing & design is the property of NIHVA TECHONOLOGIES PVT. LTD. Not to be sold or copied to any other concern

TITLE - ROOF AUTOMATION


DWG NO - NTPL-


NIHVA TECHNOLOGIES PVT.LTD.PUNE
Website - www.nihva.com


| | NAME | SIGNATURE | DATE |
|---|---|---|---|
| DRAWN | V.W. | | 24-09-2026 |
| CHK'D | S.P. | | 25-09-2026 |
| APPV'D | V.T. | | 25-09-2026 |

PRODUCT - RECTRACTABLE ROOF
CLIENT NAME - DR.NIKAM.
SITE LOCATION - KARAD.
MATRIAL -
QTY - 1
If any queries contact - info@nihva.com
PROJECTION METHOD:
SCALE :
ALL DIMENSION ARE IN mm
A2
SHEET 1 OF 2


DRAWING

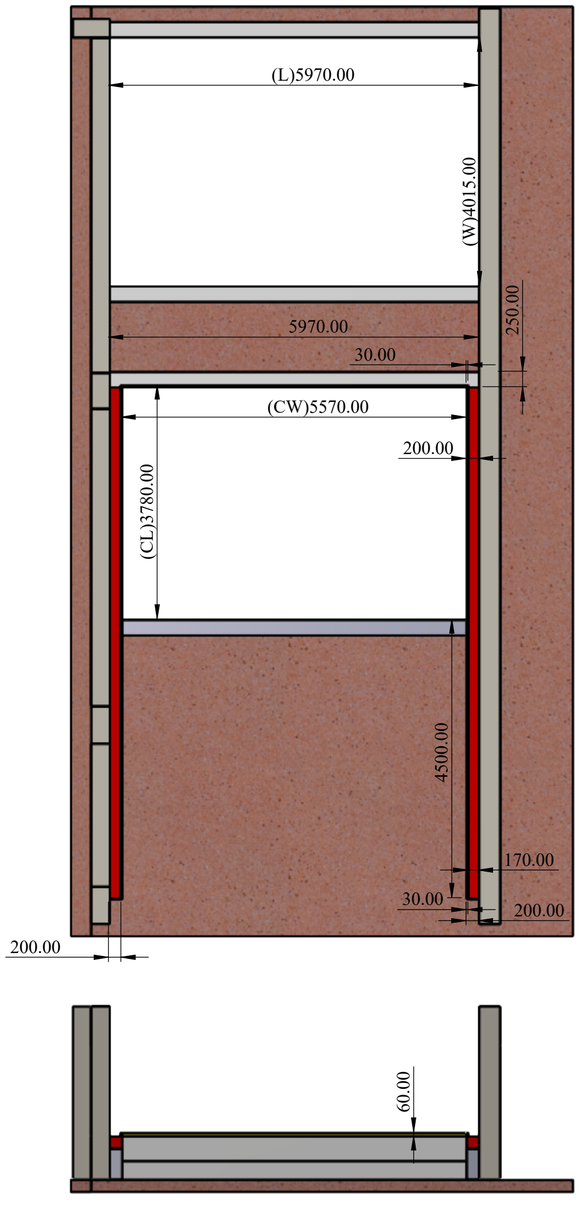

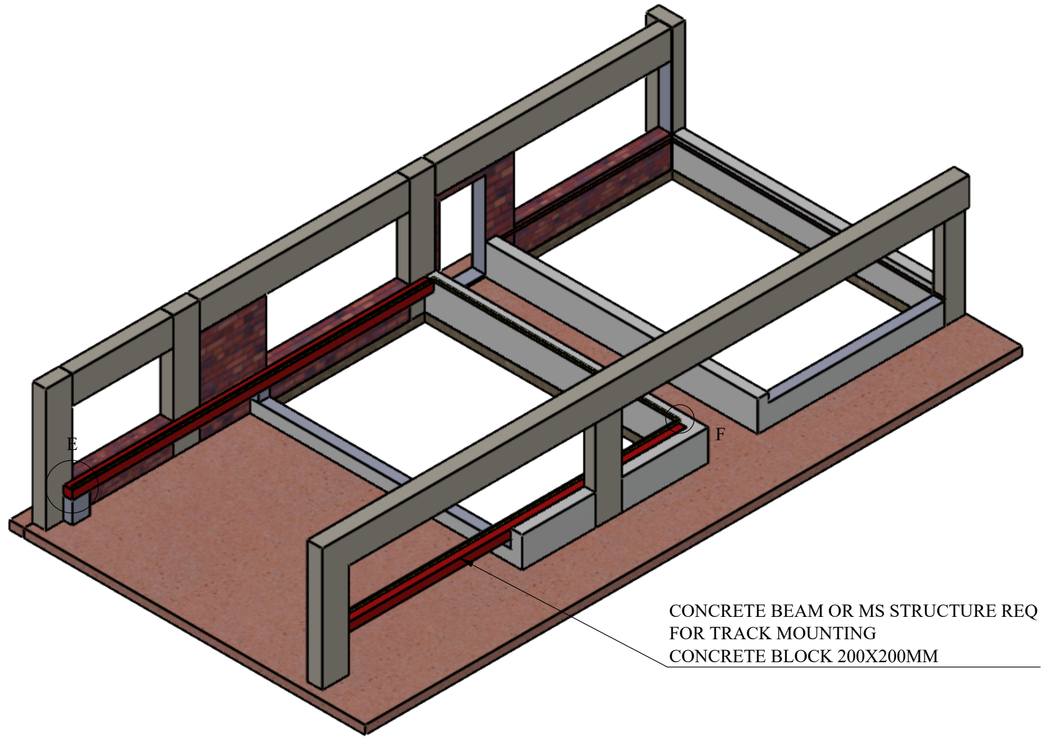
DETAIL E
SCALE 1 : 16

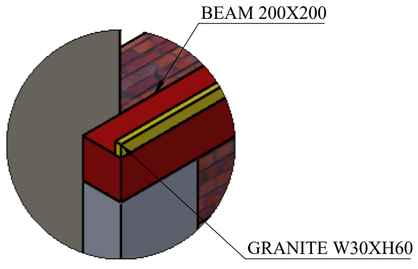


DETAIL F
SCALE 1 : 8
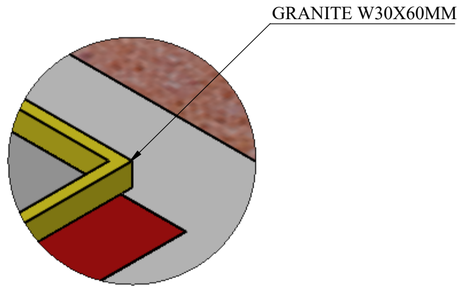
| REV DESCRIPTION | DATE | REV NO |
|---|---|---|
| | 24-09-2026 | REV 00 |
| 1. | | |

NOTE :

CIVIL DRAWING:
BASE STRUCTURE IN CLIENT SCOPE.
CONCRETE BEAM 200X200 REQ BOTH SIDE FOR TRACK MOUNTING.
GRANITE STRIP 30X60 REQUIRED FOR WATER RESTRICATION ALL SIDES

SPECIAL INSTRUCTION'S :

This drawing & design is the property of NIHVA TECHONOLOGIES PVT. LTD. Not to be sold or copied to any other concern

TITLE - ROOF AUTOMATION

DWG NO - NTPL-

NIHVA TECHNOLOGIES PVT.LTD.PUNE
Website - www.nihva.com

| | NAME | SIGNATURE | DATE |
|---|---|---|---|
| DRAWN | V.W. | | 24-09-2026 |
| CHK'D | S.P. | | 25-09-2026 |
| APPV'D | V.T. | | 25-09-2026 |

PRODUCT - RECTRACTABLE ROOF
CLIENT NAME - DR.NIKAM.
SITE LOCATION - KARAD.
MATRIAL -
QTY - 1
If any queries contact - info@nihva.com
PROJECTION METHOD:
SCALE :
ALL DIMENSION ARE IN mm
A2