

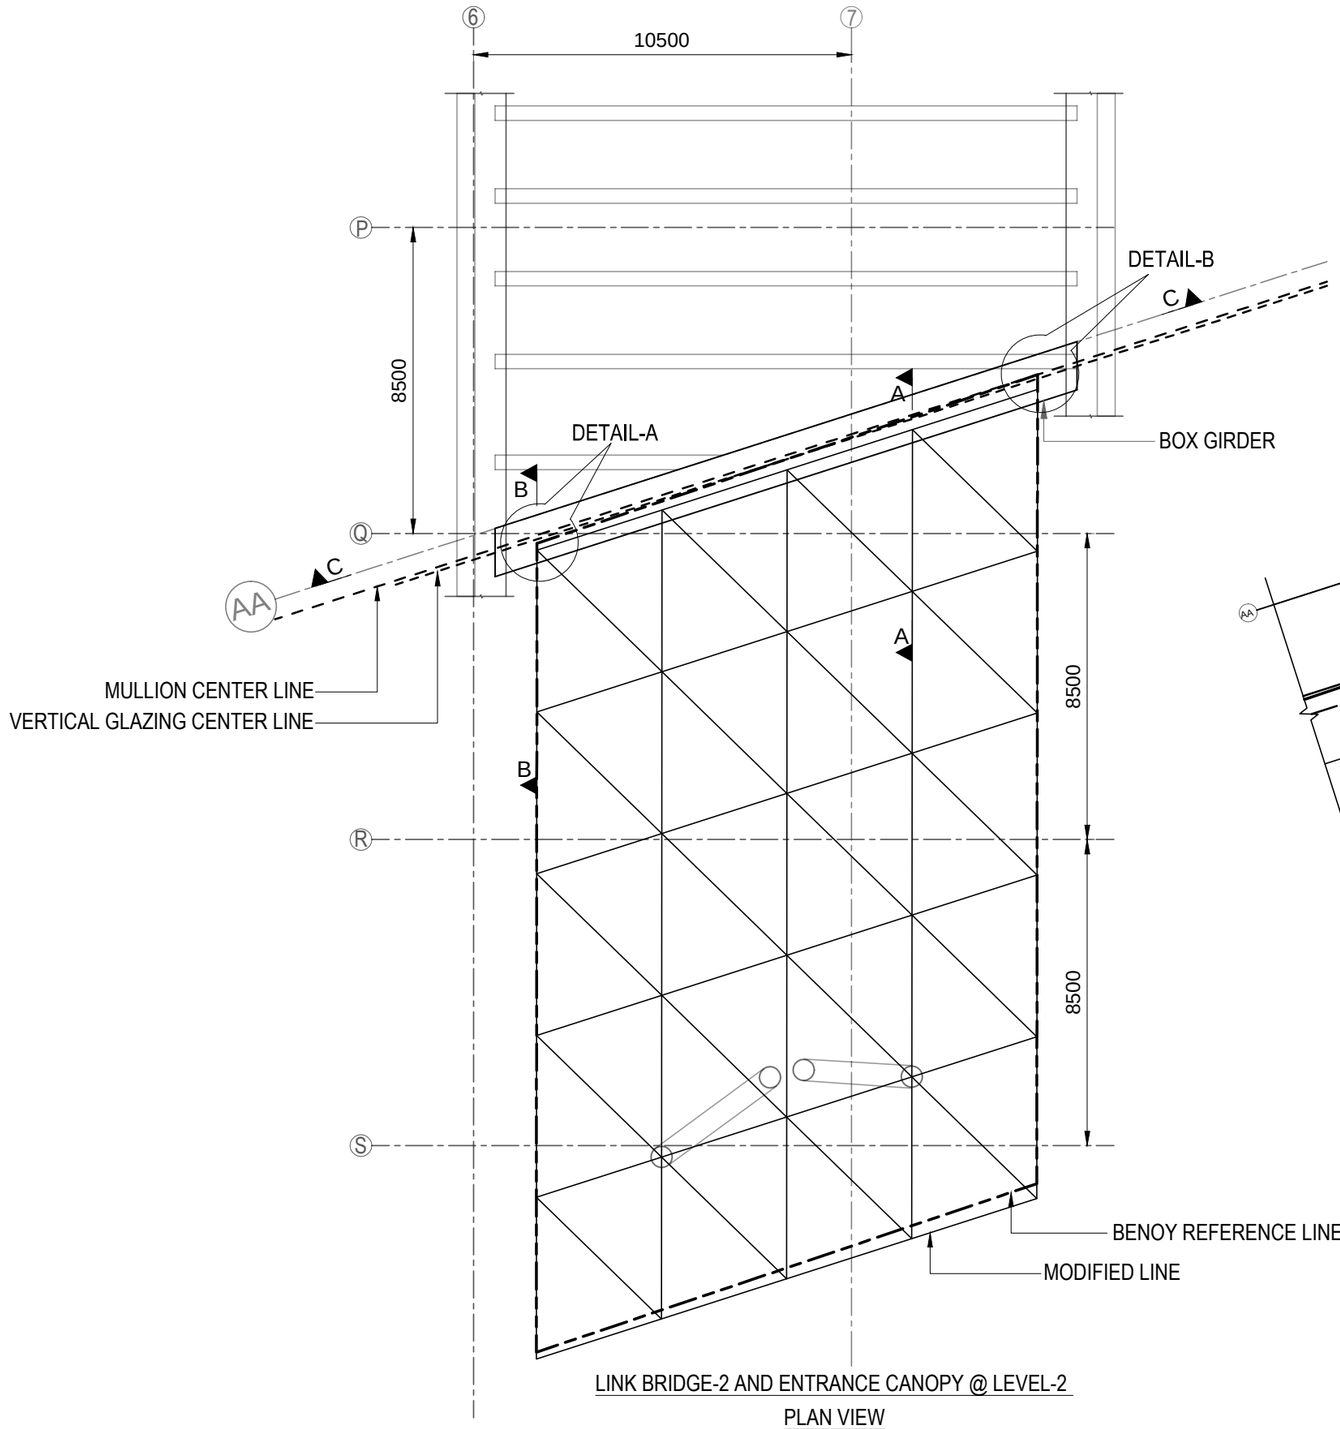


LINK BRIDGE-2 AND ENTRANCE CANOPY @ LEVEL-2

PLAN VIEW

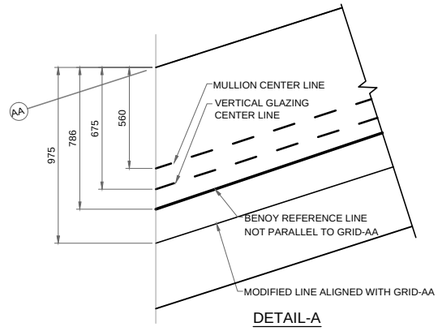


DETAIL-A

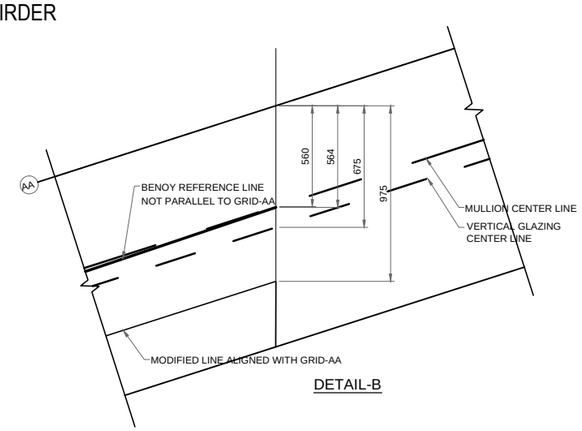

DETAIL-B

NOTES:

1. ALL DIMENSIONS ARE IN mm & UNLESS OTHERWISE MENTIONED.
2. GRADE OF STEEL IS E350.

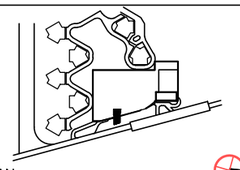

KEY PLAN

SCALE : NTS

N

REVISIONS

R0	FOR APPROVAL	15/02/2023
REV NO	DESCRIPTION	DATE

CLIENT

OBEROI REALTY

STRUCTURAL AND MEP CONSULTANT

WME
T +971 4 368 1616
E info@wmeglobal.com
W www.wmeglobal.com
Dubai | Abu Dhabi | London | Bangalore | Mumbai | Singapore

CONSULTANTS

BENOY
E: asiapacific@benoy.com
T: +852 2250 7222
www.benoy.com

PROJECT

Borivali Mixed Use
Borivali East, Mumbai, India

DRAWING TITLE

CANOPY LAYOUT & SECTION DETAILS

■ G.A ☐ ASSEMBLY ☐ SUB ASSLY ☐ COMPONENT

GOOD FOR CONSTRUCTION

DRAWN BY: GRK	DATE: 15/02/2023
DESIGNED BY: AK	DATE: 15/02/2023
CHECKED BY: GRK	DATE: 15/02/2023
APPROVED BY: SA	SCALE: 1:200

FILE NAME: G/3180/S/03-1139

DRAWING NUMBER: G / 3180 / S / 03 -1139

REV 0

These drawings are under copyright and are the property of Geodesic Techniques Pvt. Ltd. None of the drawings and related documents can be reproduced, copied in whole or in part whithout prior expressed written consent of Geodesic Techniques Pvt. Ltd. These drawings cannot be handed over to a third party or used for any purpose, other than that for which it has been loaned.

GEODESIC TECHNIQUES
Geodesic Techniques Pvt. Ltd.
N4, 4th Cross, 1st Stage, Peenya Industrial Area,
Bangalore, Karnataka – 560 058. INDIA
Tel: +91 80 6745 1200
Fax: +91 80 6745 1210
Email: enquiry@geodesictechniques.com