



Abbrevation's:
WOW-Wall Opening Width
WOH-Wall Opening Height
UC-Under Cut
FFL-Finished Floor Level

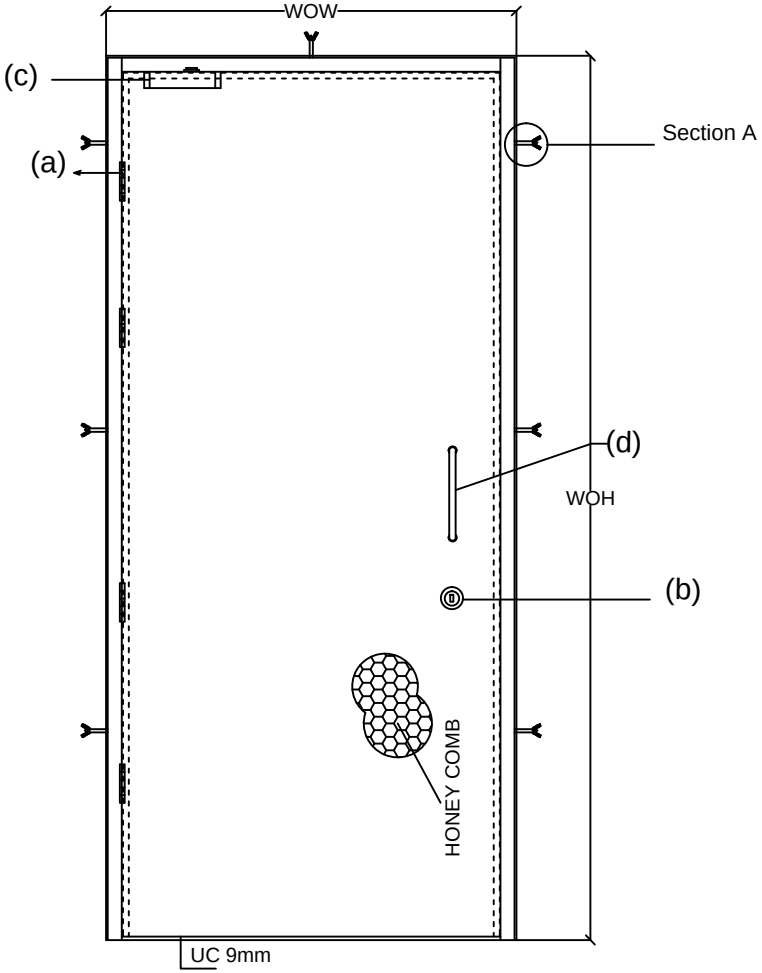

Elevation



Top View

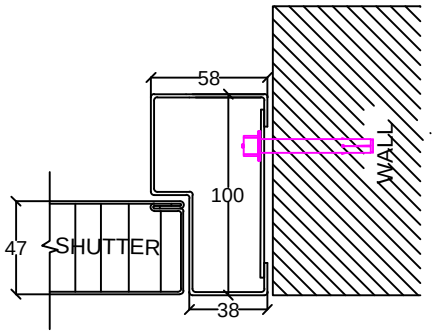

Detail view of Section A

ASSESORIES DETALES

(a) HINGES: SS Ball bearing butt hinges 100x75x3mm.

(b) LOCK: Mortise dead lock,Cylinder(one side key& thumb turn other side) with escutcheon.

(c) DOOR CLOSER

(d) HANDLE : D Handle(254mm)

Shutter thickness : 47 mm
Frame Sheet thick : 1.2mm
Shutter sheet thick : 0.8mm
Fixing : On Soliid Brick plasterd wall with Anchors
Electrostatic powder coated

NOTE:- *All Dimensions are in mm.
*Tolerance:-All Linear Dimensions ±3mm,Others ±0.5mm.
*The Drawing Is For Location of Hardware only. Drawing Does Not Represent The Hardware For More Clarity, Please Go Through Hardware Broucher.

DOOR TYPE	WOW	WOH	TYPE 1	TYPE 2	TYPE 3	TYPE 4	TOTAL
FIRE DOOR	1200	2200					4

Client should mention door handling type from door handling sheet.

COLOR - RAL 7035 LIGHT GREY

This drawing & designing is the property of NIHVA TECHNOLOGIES. Not be sold or copy to any other concern.

SINGLE LEAF STEEL DOOR

CLIENT APPROVAL

ALL DIMENSION ARE IN mm

	NAME	DATE	SIGN.
DRAWN	OMKAR	31/08/16	
CHECK	ANIL	31/08/16	
REV.	0		
APPRD.			
MFG			

NIHVA TECHNOLOGIES PVT. LTD.
NIHVA TECHNOLOGY PVT. LTD. PUNE
Tel : 020 66304033
Email:- info@nihva.com
Website:-www.nihva.com

CLIENT - INDOSPACE
PROJECT - KVR INDUSTRIAL PARK PVT. LTD.
SITE - RANJANGAON
DWG. NO. - NIHVA/16-17/0067
SCALE: NTS | WT: | SHEET: 01 OF 01
If any queries contact : projects@nihva.com