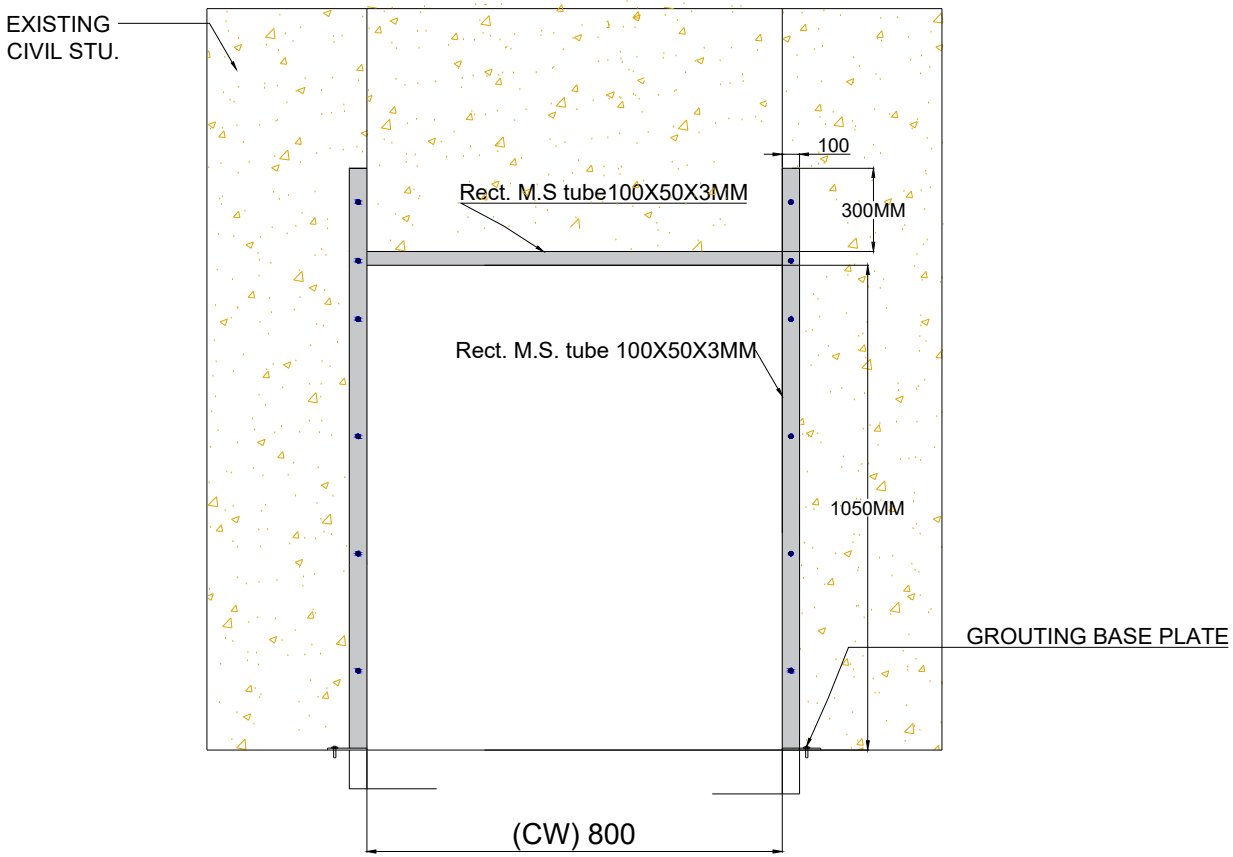


M.S. STRUCTURE DETAILS

Sr	Description	Clear Width (CW)	Clear Height (CH)	QTY
1	HSD	**800**	**1000**	3

This drawing & design is the property of NIHVA TECHNOLOGIES. Not to be sold or copied to any other concern.

TITLE: HIGH SPEED DOOR STRUCTURE DRAWING

NIHVA TECHNOLOGIES PVT. LTD. PUNE
Tel : 020 66304033
Email:- info@nihva.com
Website:- www.nihva.com

	NAME	SIGN	DATE
DRAWN	J.P		22.11.2025
CHECK	B.S		22.11.2025
APPRD.	V.T		22.11.2025

CLIENT - MARS PETCARE
PROJECT - HIGH SPEED DOOR
FORMAT NO - NIHVA-DD-F-03
If any queries contact : Design@nihva.com
DWG. NO. : NIHVA/25-26/010 | REV- R00
ALL DIMENSION ARE IN mm | SCALE: NTS | WT: | SHEET: