

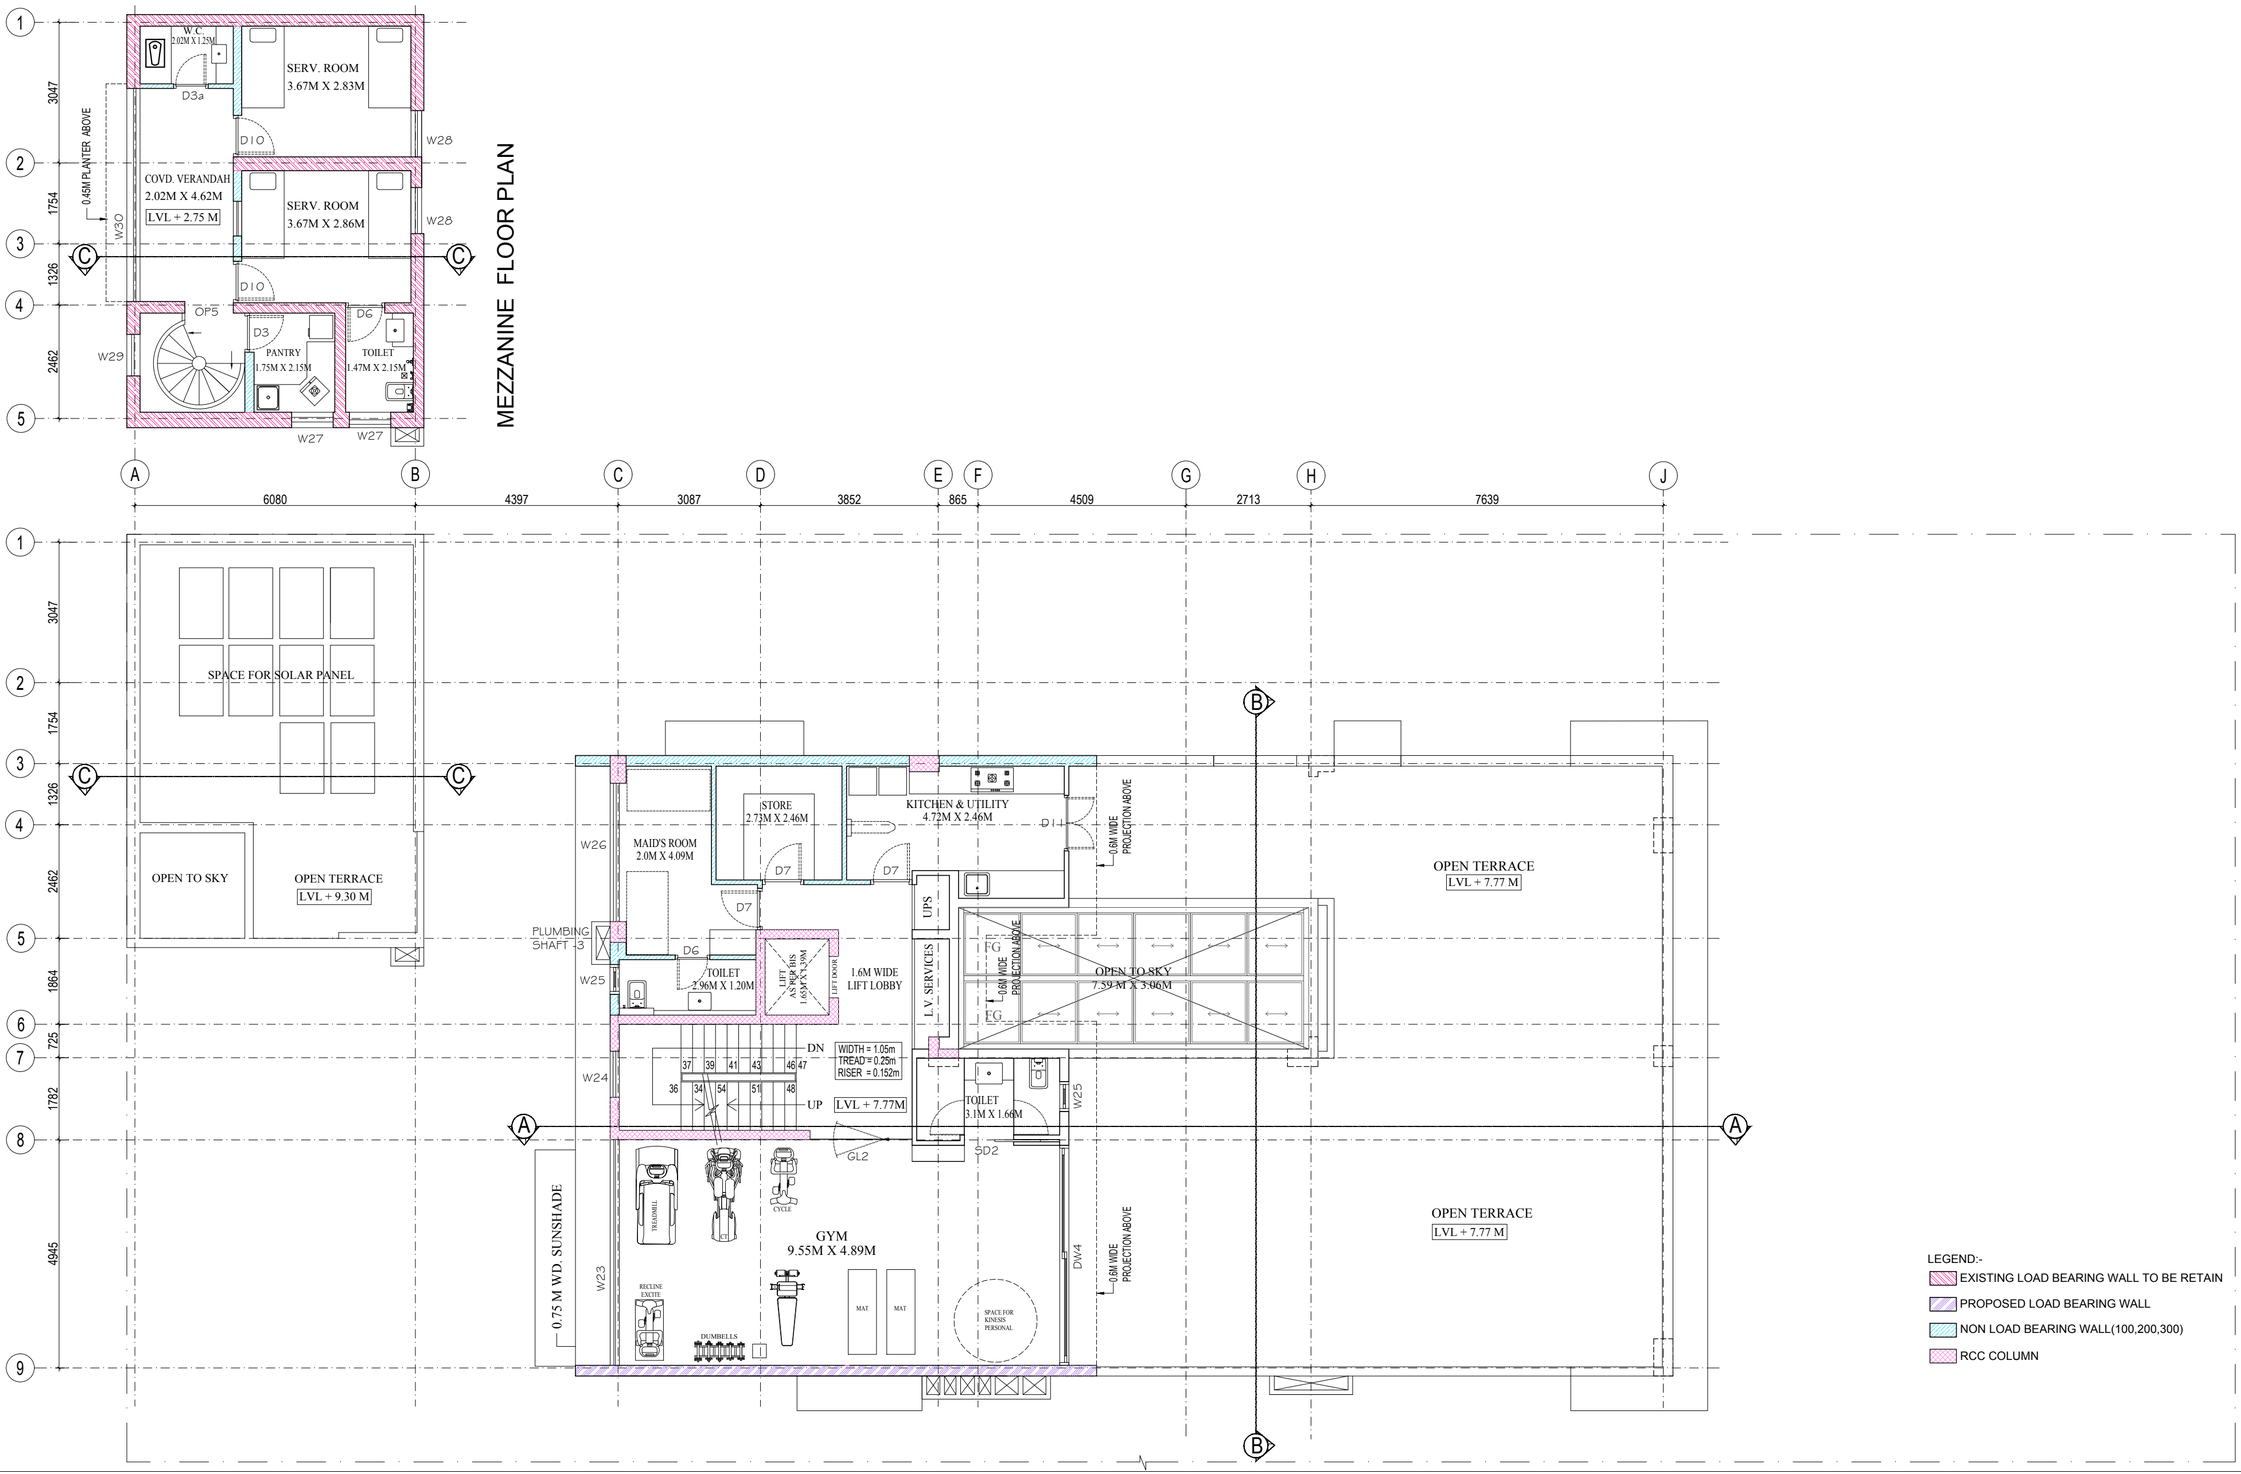



Rajeev Agarwal Architects J-1963, Chittaranjan Park,New Delhi -110019 PH: 26271576,26274272		NORTH	STAGE - Working Drawing
PROJECT COURTYARD HOUSE			DRAWN BY - R.SINGH / CHECKED BY - AMIN SCALE - 1:100 (A2) / DATE - 30.07.2021

DRAWING TITLE -
Second Floor Plan

DRAWING NO.
CH | A-1.03 | R0

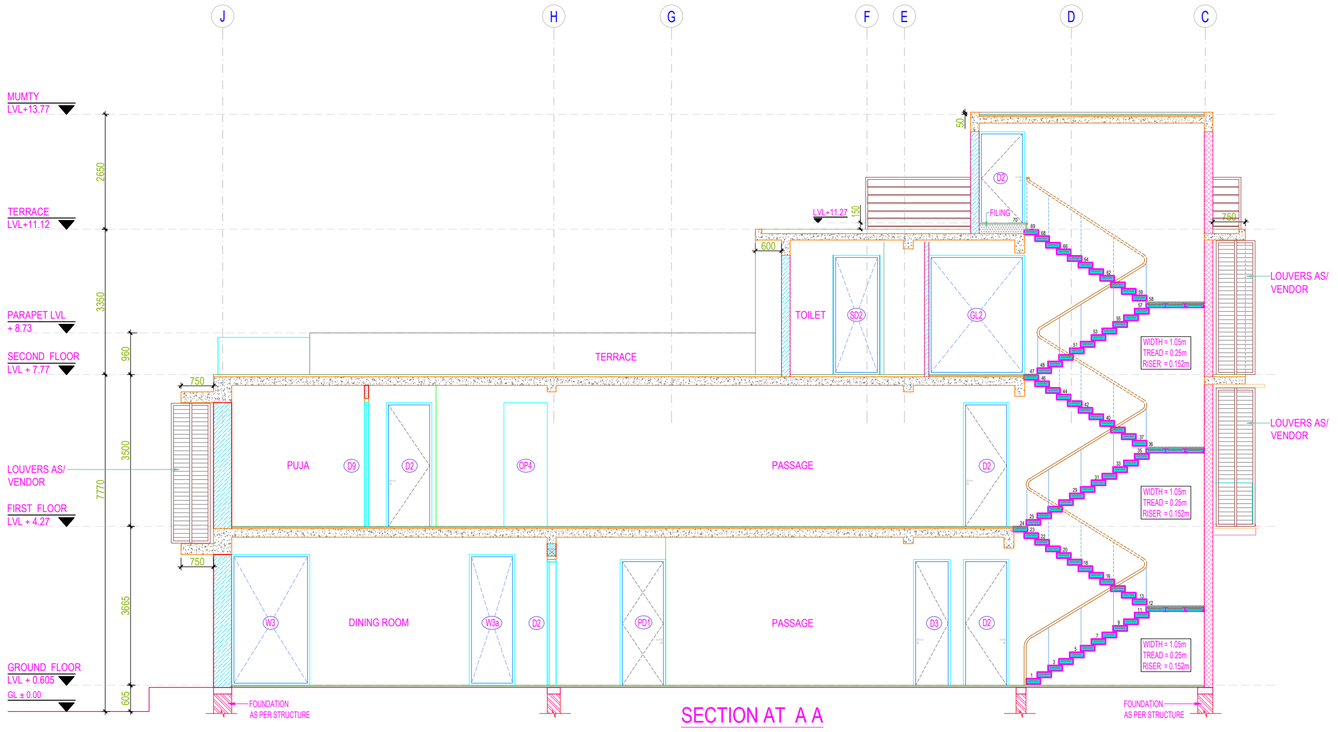

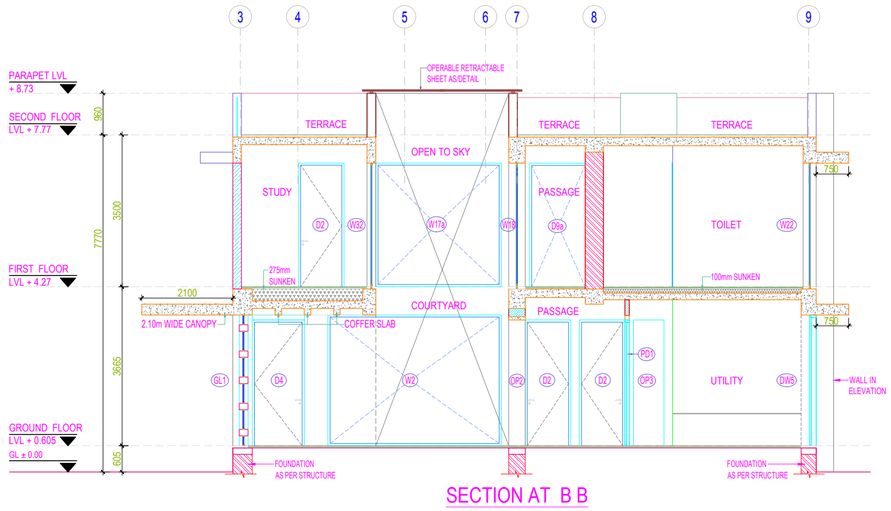

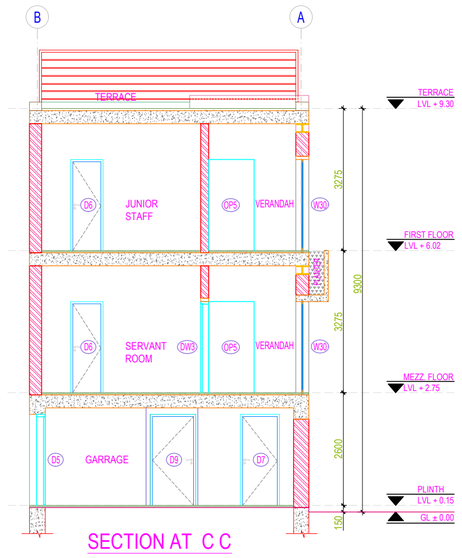

Rajeev Agarwal Architects J-1963, Chittaranjan Park,New Delhi -110019 PH: 26271576,26274272		STAGE - Working Drawing	DRAWING TITLE - Section at AA, BB & CC
PROJECT COURTYARD HOUSE		DRAWN BY - R.SINGH CHECKED BY - AMIN	DRAWING NO. CH A-3.01 R0
		SCALE - 1:100 (A2) DATE - 27.08.2021	