

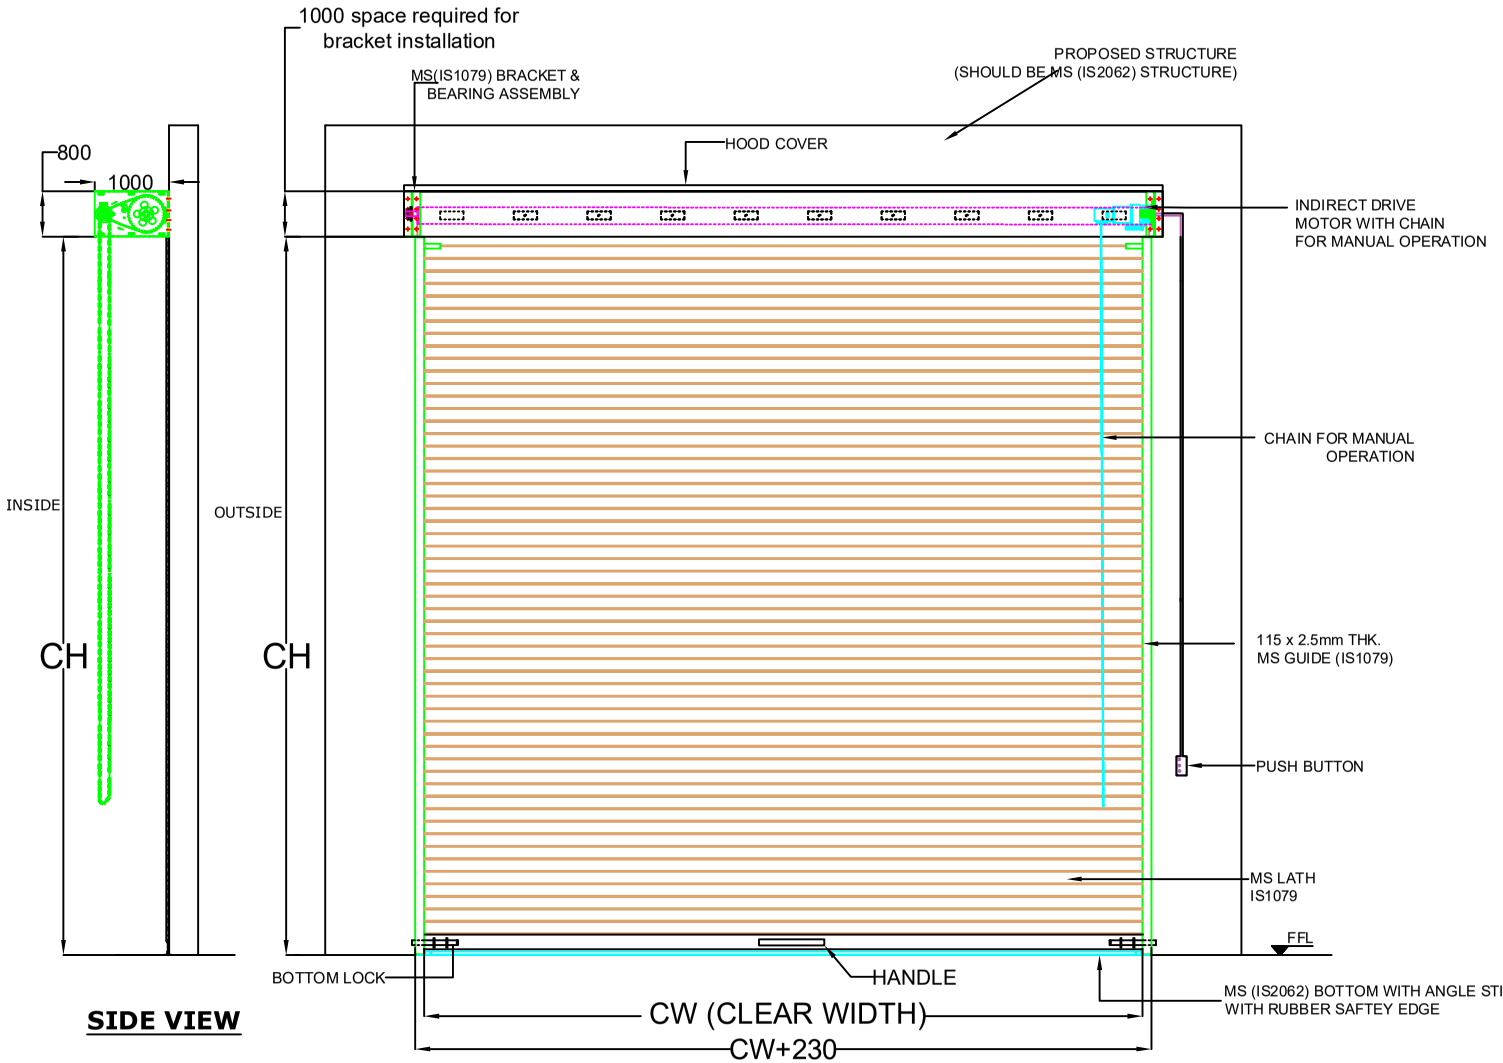


SIDE VIEW


ELEVATION

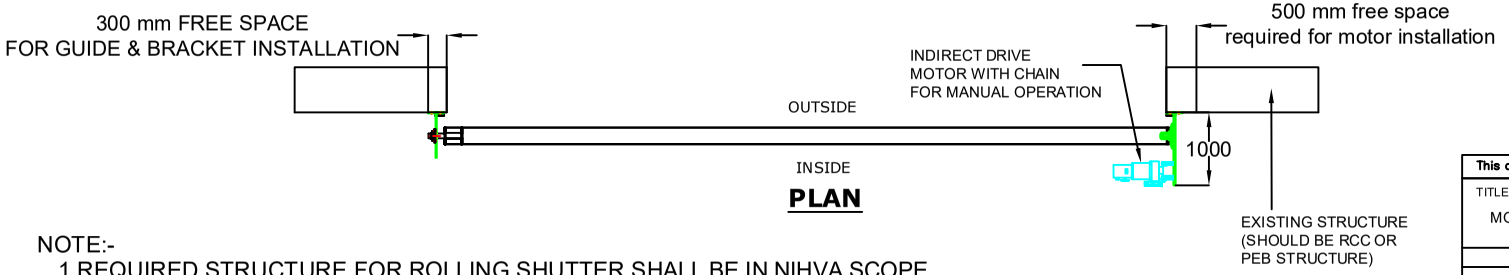

PLAN

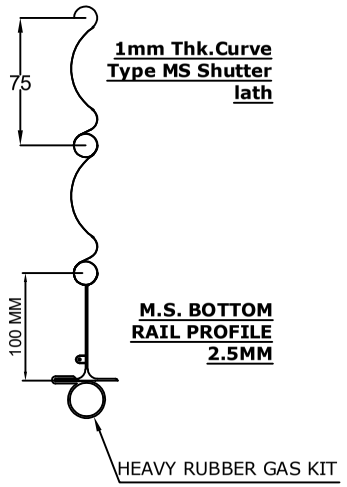

M.S. BOTTOM RAIL PROFILE 2.5MM

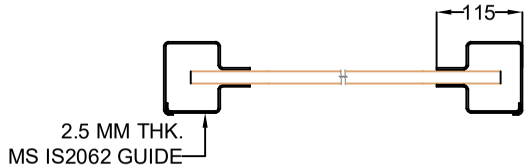

COLOR:-
1. RAL7035(LIGHT GRAY) ☐
2. RAL9016(TRAFFIC WHITE) ☐
3. RAL5005(SIGNAL BLUE) ☐
4. RAL7004(SIGNAL GRAY) ☐
5. RAL5015(SKY BLUE) ☑

CLEAR WIDTH (CW)	CLEAR HEIGHT (CH)	QUANTITY
5000	6000	8

Rev 01:- 04/02/2022
1. Added IS material specification for MS material.
2. Added motor capacity details.
3. Mentioned RAL code.

Rev 02:- 11/ 02/ 2022
1. Reduced quantity of shutter.

Rev 03:- 04/ 04/ 2022
1. Motor and paint details to be added

NOTE:-
1. REQUIRED STRUCTURE FOR ROLLING SHUTTER SHALL BE IN NIHVA SCOPE.
2. ALL REQUIRED CIVIL WORK IN CLIENT SCOPE.
3. 3 PHASE POWER SUPPLY SHOULD BE PROVIDED BY CLIENT.
4. MOTOR : JIELONG , 1.5 TON, 1.25 KW, 3PH
5. PRIMER COAT THICKNESS WILL BE 40 MICRON AND FINISH COAT THICKNESS WILL BE 60 MICRON

This drawing & designing is the property of NIHVA TECHNOLOGIES. Not to be sold or copied to any other concern.

TITLE			
MOTORIZED ROLLING SHUTTER			
	NAME	SIGN	DATE
DRAWN	G.P.		13/09/21
CHECK	A.K.		13/09/21
APPROVAL	V.T.		13/09/21

NIHVA TECHNOLOGIES PVT. LTD.

NIHVA TECHNOLOGIES PVT. LTD. PUNE
Tel : 020 66304033
Email:- info@nihva.com
Website:- www.nihva.com

CLIENT - REWARD CONSTRUCTION
PROJECT -
SITE - INDAPUR
If any queries contact : design@nihva.com
DWG. NO. : NIHVA/21-22/0232
REV. - 03
ALL DIMENSION ARE IN mm
SCALE: NTS
WT:
SHEET: 01 OF 01