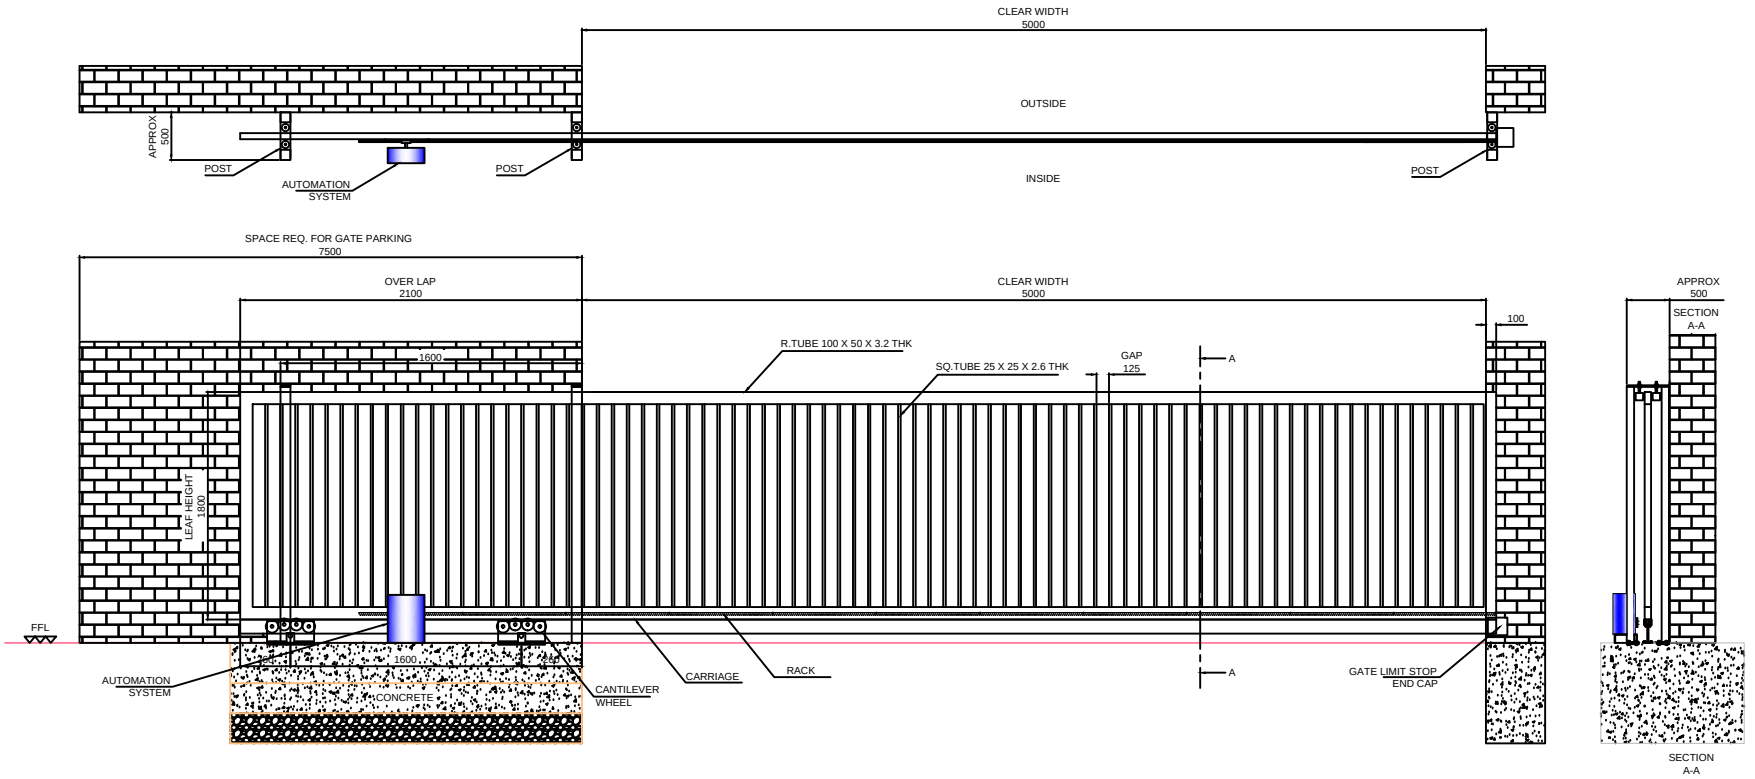


TOLERANCE - ±10mm

QTY : 2 NOS

NOTE-
1. ALL REQUIRED CIVIL WORK WILL BE IN CLIENTS SCOPE.
2. TWO COATS OF PRIMER AND TWO COATS OF SYNTHETIC ENAMEL PAINT OF APPROVE SHADE.
3. SAFETY ACCESSORIES : FLASHING LIGHT, SAFETY PHOTOCELL.
4. GATE LEAF WILL BE IN TWO PARTS FOR TRANSPORTATION & WILL BE WELD TOGETHER ON SITE.

This drawing & design is the property of NIHVA TECHNOLOGIES. Not to be sold or copied to any other concern.

TITLE				
AUTOMATIC CANTILEVER GATE				NIHVA TECHNOLOGIES PVT. LTD. PUNE Tel : 020 66304033 Email:- info@nihva.com Website:- www.nihva.com
	NAME	SIGN	DATE	
DRAWN	P.A		23.12.2019	CLIENT - DESAI CONSTRUCTION
CHECK	G.J		23.12.2019	PROJECT -
APPRD.				SITE LOCATION - GUJARAT
If any queries contact : design@nihva.com				DWG. NO. : NIHVA/19-20/0183 / REV- R00
ALL DIMENSION ARE IN mm				SCALE: NTS / WT: / SHEET: 01 OF 01