
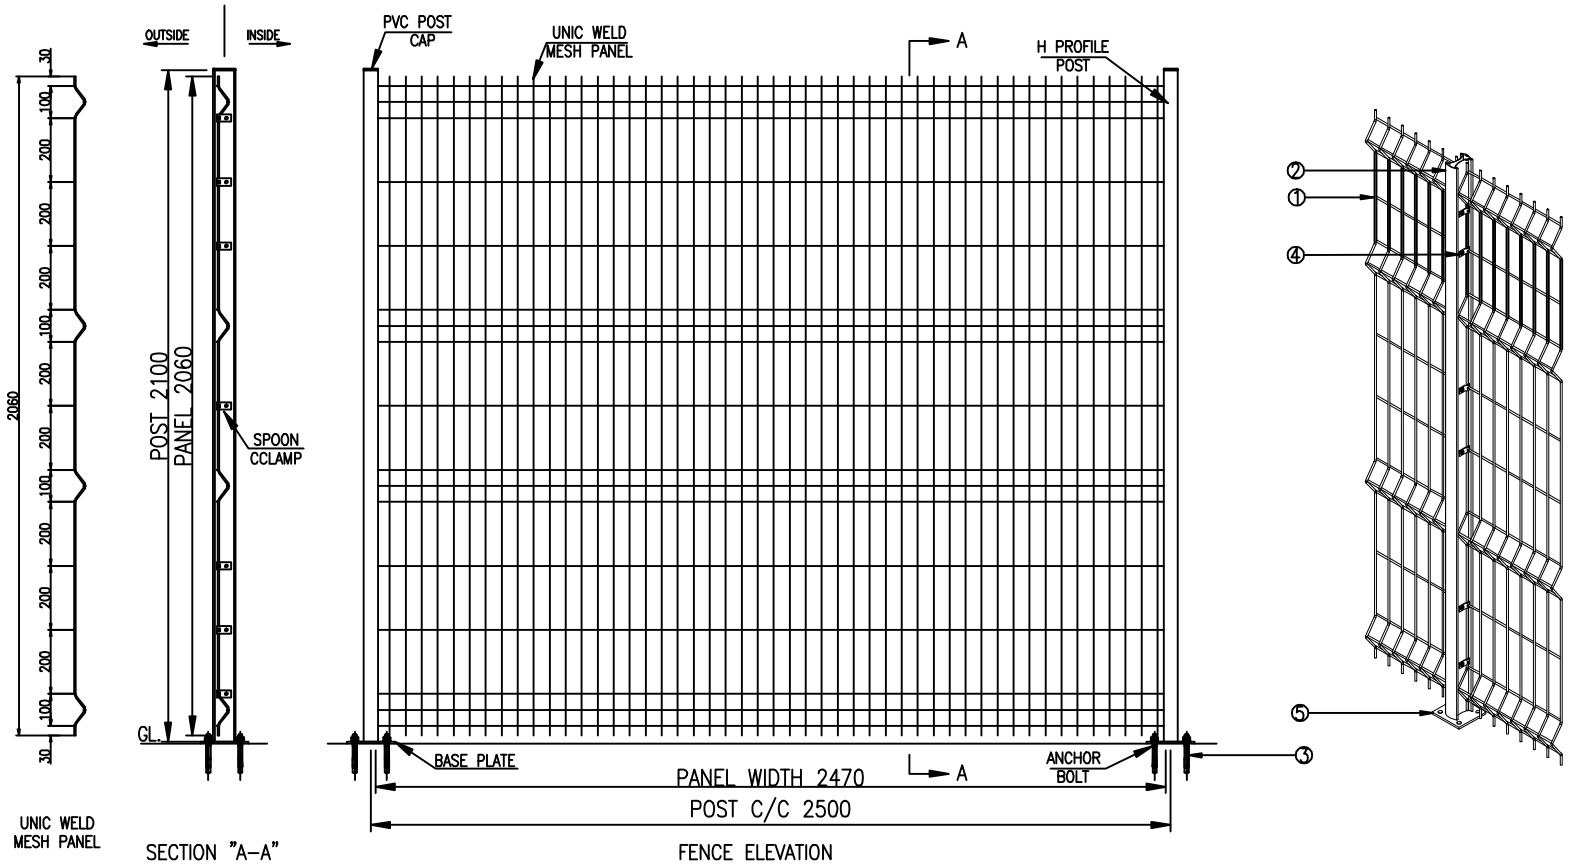


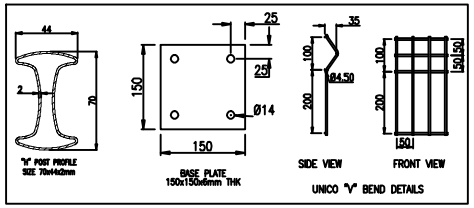

Total quantity of Panel = 13 NOS.
Total quantity of H post = 42 NOS.
MOC is Galvanized Steel
Temperature sustainability around 50 deg
Colour: RAL 7044

BILL OF MATERIAL

SR.NO.	PART	SIZES	QTY.
1	WELD MESH PANEL	MESH SIZE 50x200mm, PANEL HEIGHT 2060mm, PANEL WIDTH 2470mm WIRE Ø 4.5mm, WITH 2 V BENDS.	1 NOS.
2	H PROFILE POST	H PROFILE POST, 2100 ABOVE THE GROUND LEVEL, WITH BASE PLATE 150x150x6mm THK.	1 NOS.
3	ANCHOR BOLT	M12x150mm LONG.	4 NOS.
4	CLAMPS	SPOON CLAMPS WITH SECURITY NUT & BOLT	7 NOS.
5	BASE PLATE	150X150X6mm THK	1 NOS.

This drawing & designing is the property of NIHVA TECHNOLOGIES. Not be sold or copy to any other concern.

TITLE	FENCE DETAILS (H POST)		NIHVA TECHNOLOGIES PVT. LTD.
	SIGN	DATE	
DRAWN	ABHIJIT	23/06/15	CLIENT -SMS INDIA
CHECK	ANIL	23/06/15	PROJECT-TATA STEEL
ENG			SITE -JAMSHEDPUR
APPRD.			DWG. NO. -NIHVA/15-16/047
Ref. No.			SCALE:01 | WT: | SHEET:01
ALL DIMENSION ARE IN mm			If any queries contact : projects@nihva.com

NIHVA TECHNOLOGY PVT. LTD. PUNE
Tel : 020 66304033
Email:- info@nihva.com
Website:- www.nihva.com