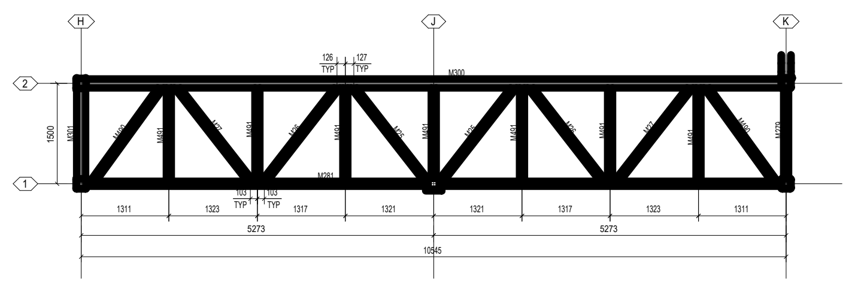

SECTION D - D
1:40

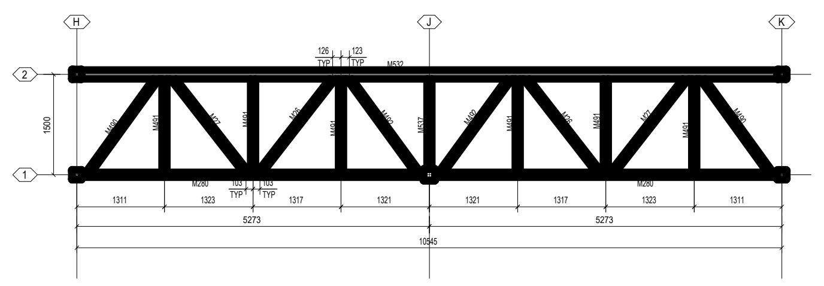

SECTION C - C
1:40

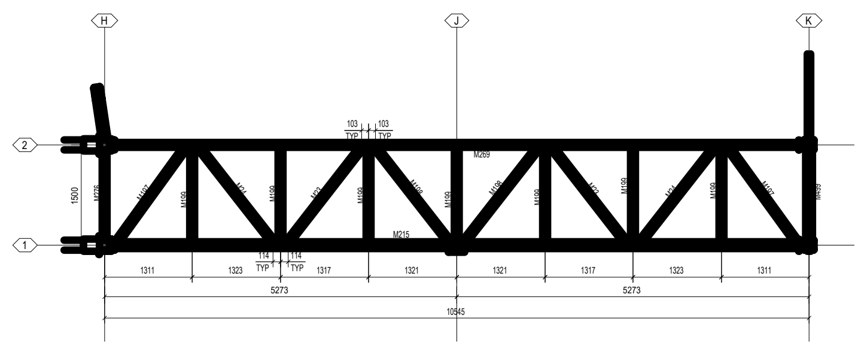

SECTION B - B
1:40

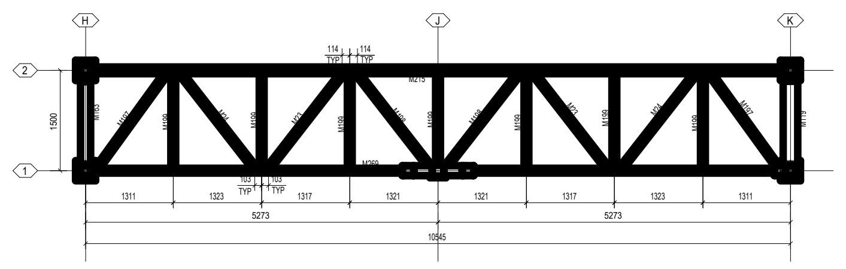

SECTION A - A
1:40

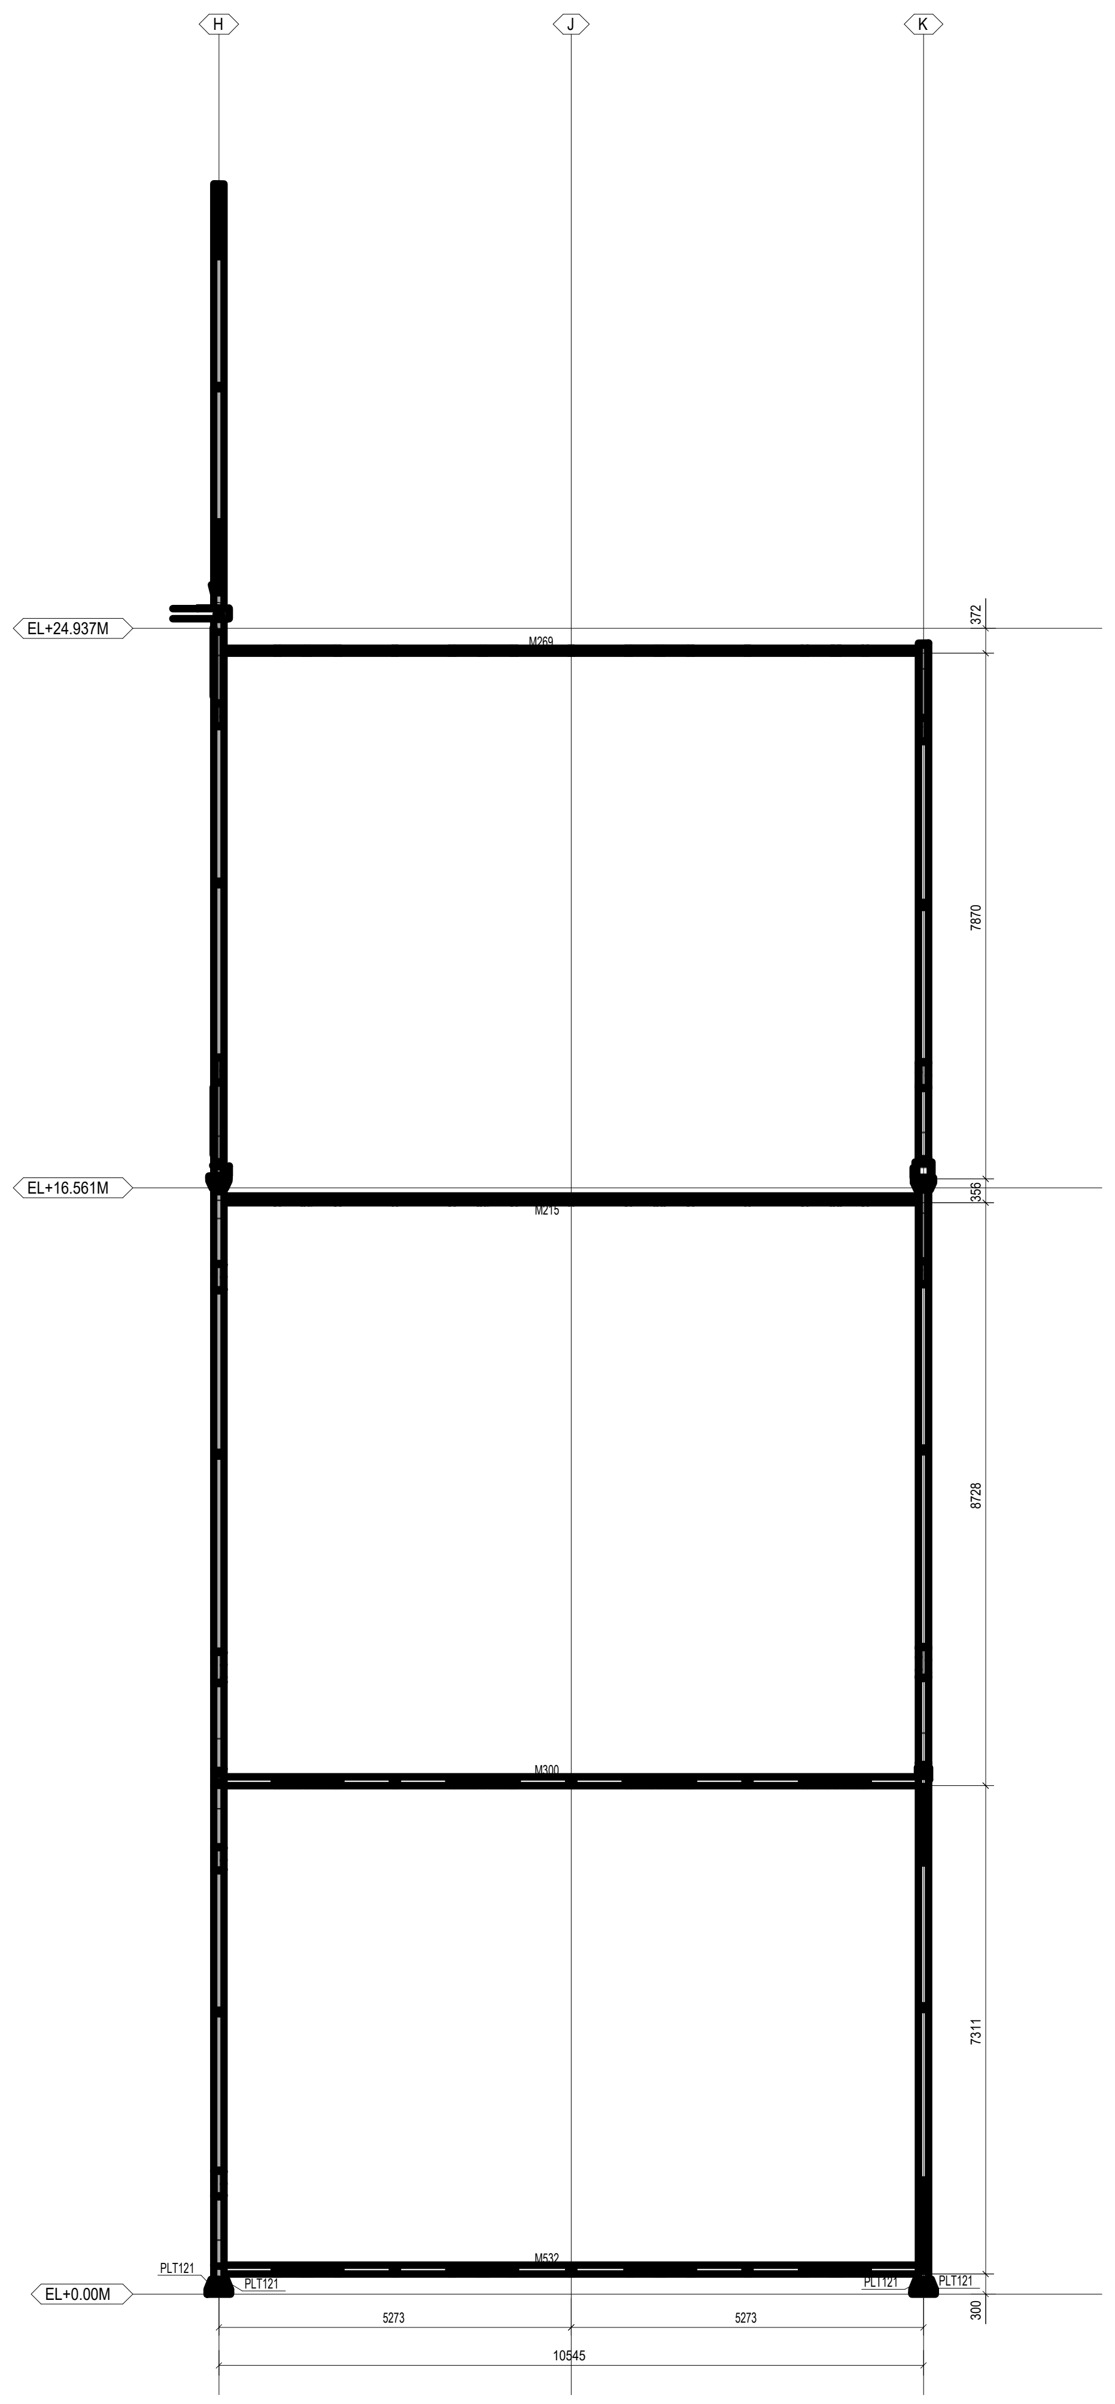

GRID @ 2
1:60

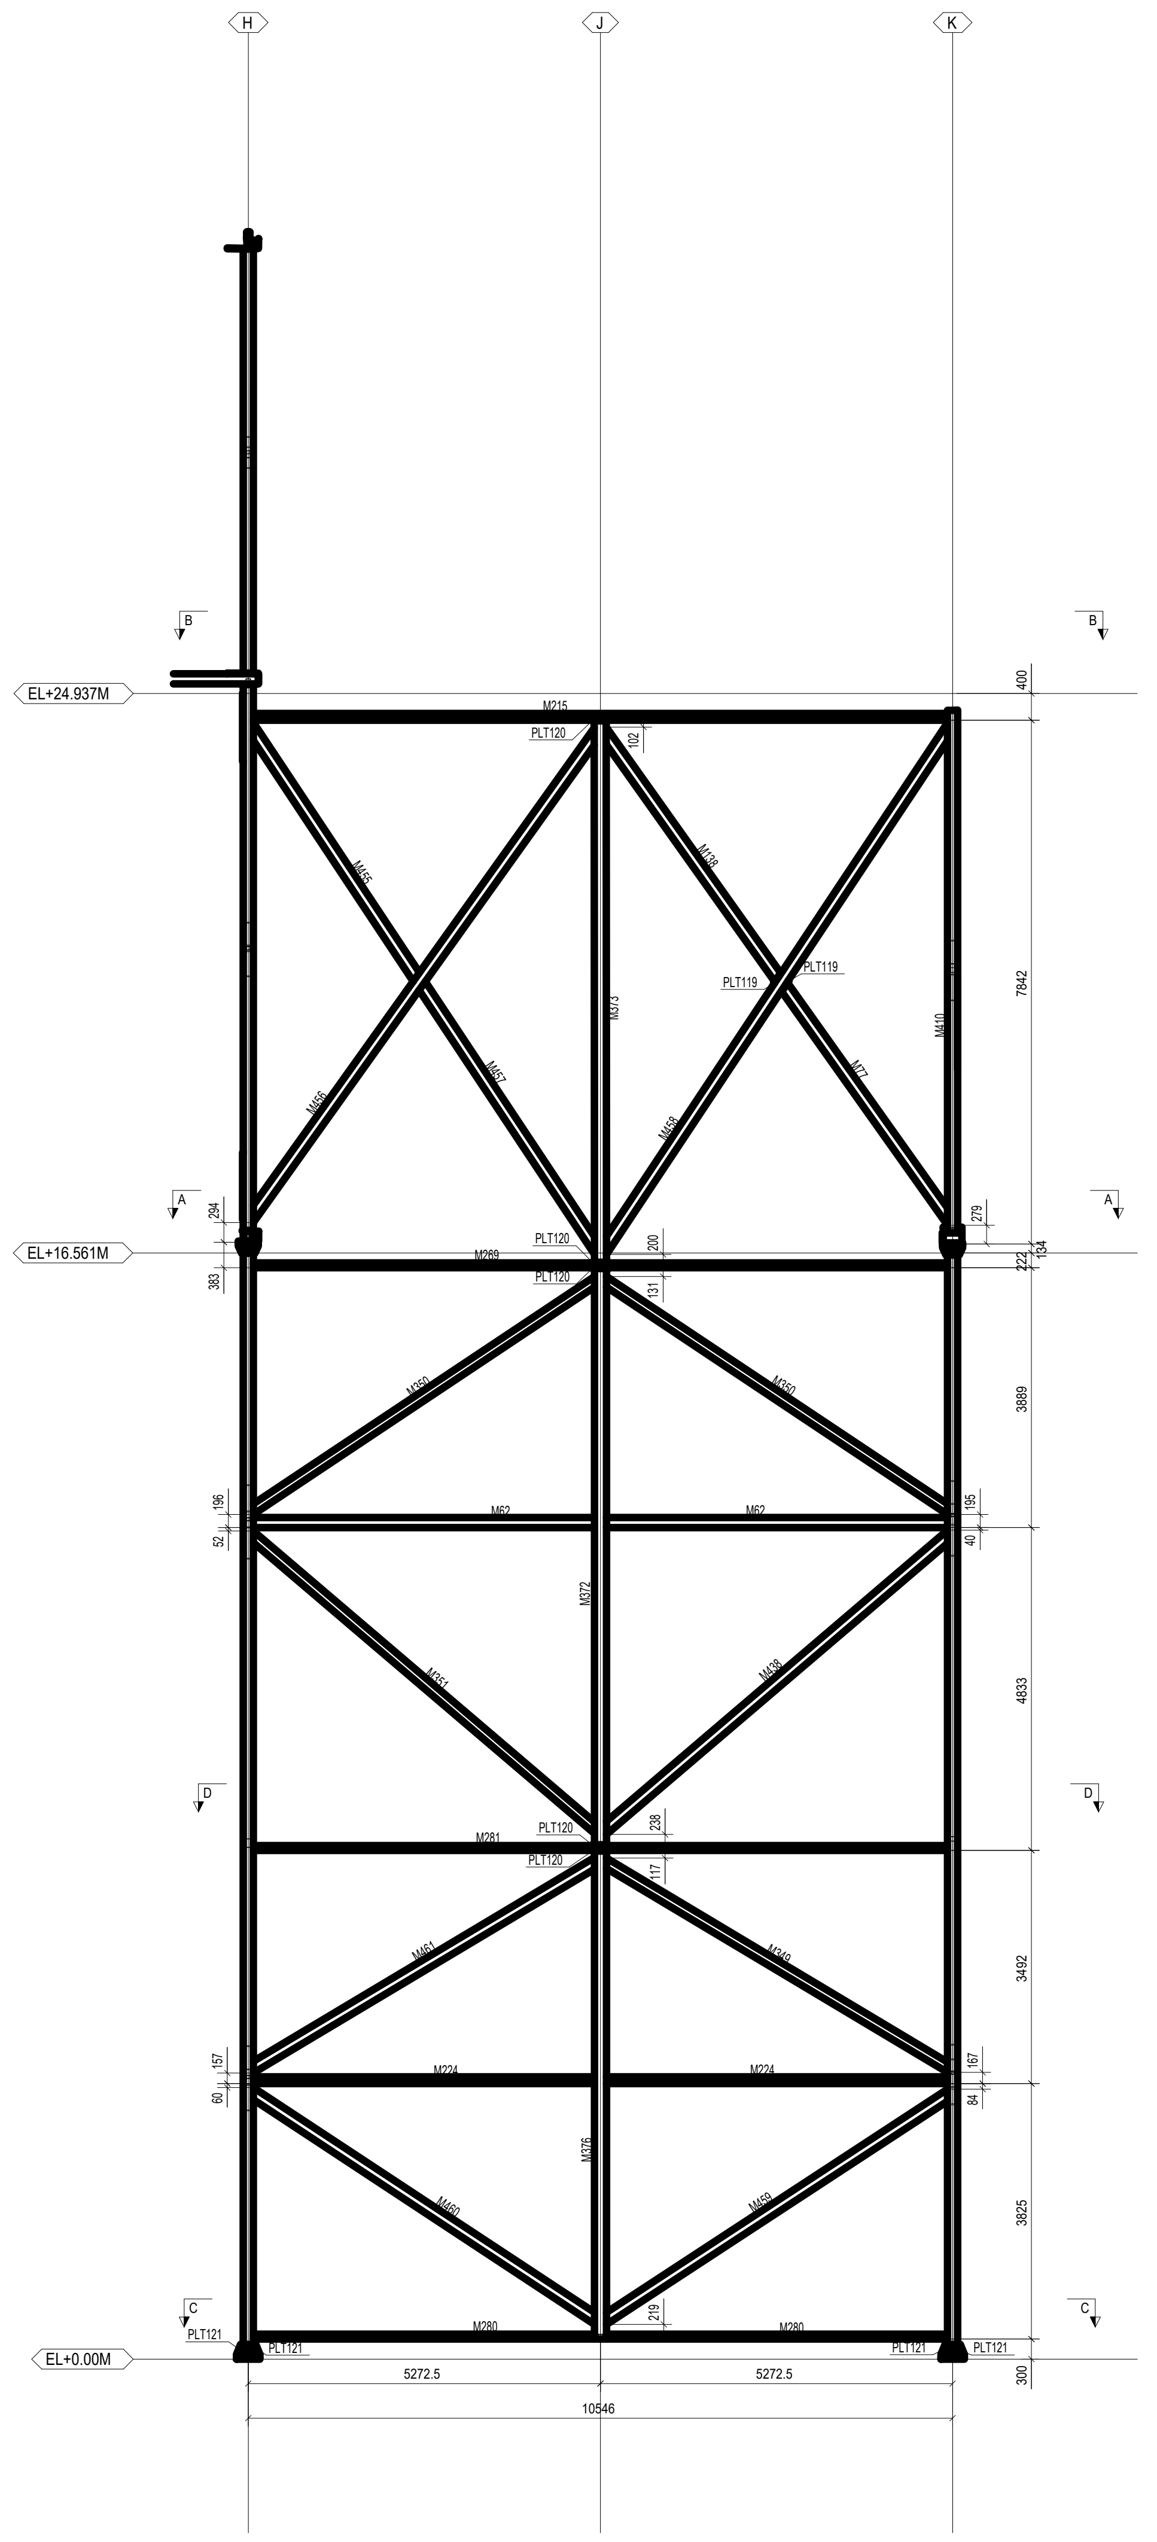

GRID @ 1
1:60

| | | | | | |
|---|---|---|---|---|---|
| | | | | | |
| | | | | | |
| | | | | | |
| 0 | ISSUED FOR APPROVAL | 05.11.22 | IMS | HAB | HAB |
| REV.NO. | DESCRIPTION. | REV.DATE | DRAWN. | CHKD. | APPD. |

DWG.TITLE :- DETAIL DRAWING FOR 84MTR

| | |
|---|---|
| PROJECT | MEGADOOR INSTALLATION AT HYDRABAD AIRPORT |
| CLIENT | GMR |

SALT DESIGN SERVICES

NIHVA TECHNOLOGIES
PVT. LTD. PUNE
Tel : 020 66304033
Email:- info@nihva.com
Website:- www.nihva.com

| | | |
|---|---|---|
| DRAWN :RRK | CHECKED : HAB | SCALE: 1:100 |
| APPROVED : HAB | JOB CODE. : 1729 | DATE: 05.11.2022 |

| | | |
|---|---|---|
| DWG.NO: SALT_1729_FDN_01_R0 | (SH-1OF1) | REV. - R0<br>SIZE. - A1 |

A1 [841 x 594]