Abbrevation's:
WOW-Wall Opening Width
WOH-Wall Opening Height
UC-Under Cut
FFL-Finished Floor Level

ASSESORIES DETALES

(a) HINGES: SS hinges 100x75x3mm

(b) LOCK : Mortise dead Lock with cylinder(One side key & thumb turn on other side)with escutcheon.


(c) DOOR CLOSER : B4W

(d) HANDLE : D Handle (300x22) 2 pair.

(e) VISION PANEL - 5mm THK. GLASS OF SIZE-200X300mm

Shutter thickness : 47 mm
Frame Sheet thick : 1.20mm
Shutter sheet thick : 0.80mm
Fixing : On FRAME OF PEB STRUCTURE


NOTE:- *All Dimensions are in mm.
*Tolerance:-All Linear Dimensions ±3mm,Others ±0.5mm.
*The Drawing Is For Location of Hardware only. Drawing Does Not Represent The Hardware For More Clarity, Please Go Through Hardware Broucher.

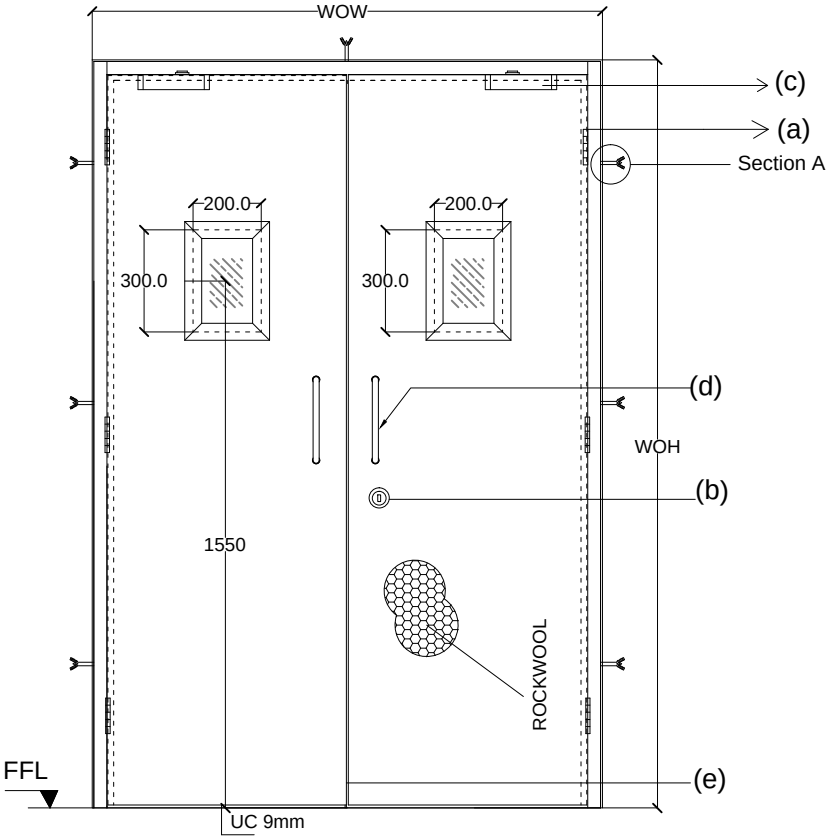

Outside Elevation



Top View

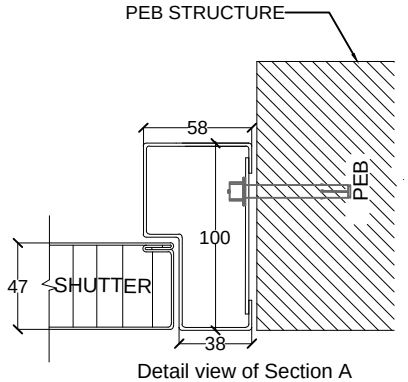

Detail view of Section A

COLOR - GREY WHITE(RAL 9002)

Door Type

WOW	WOH	TYPE 5	TYPE 6	TYPE 7	TYPE 8	QUANTITY
2000	2500			04		04

This drawing & designing is the property of NIHVA TECHNOLOGIES. Not be sold or copy to any other concern.

TITLE: STEEL DOOR (DOUBLE LEAF)

	NAME	DATE	SIGN.
DRAWN	OMKAR	25/09/17	
CHECK	SHEKHAR	25/09/17	
APPRD.	SHEKHAR	25/09/17	
REV.			
MFG			

ALL DIMENSION ARE IN mm

NIHVA TECHNOLOGIES PVT. LTD.
NIHVA TECHNOLOGY PVT. LTD. PUNE
Tel : 020 66304033
Email:- info@nihva.com
Website:-www.nihva.com

CLIENT -
PROJECT -
SITE LOCATION -
DWG. NO. - NIHVA/17-18/VDR/0133
SCALE:NTS | WT: | SHEET: 01 OF 01
If any queries contact : projects@nihva.com