

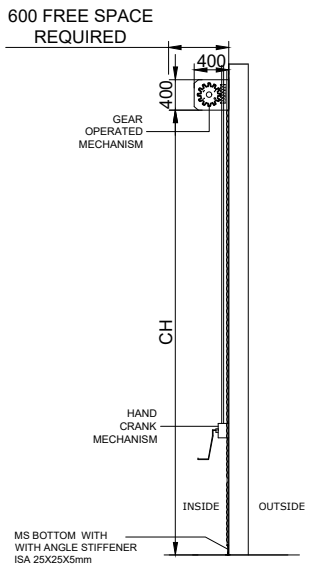



SIDE VIEW

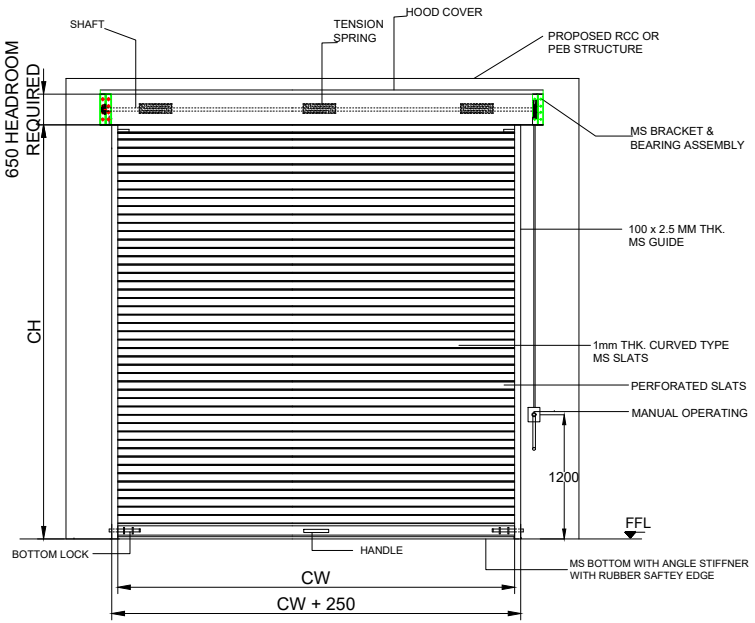

INSIDE ELEVATION

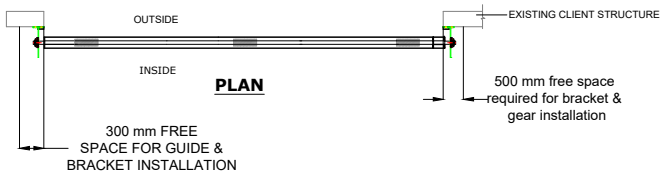


PLAN

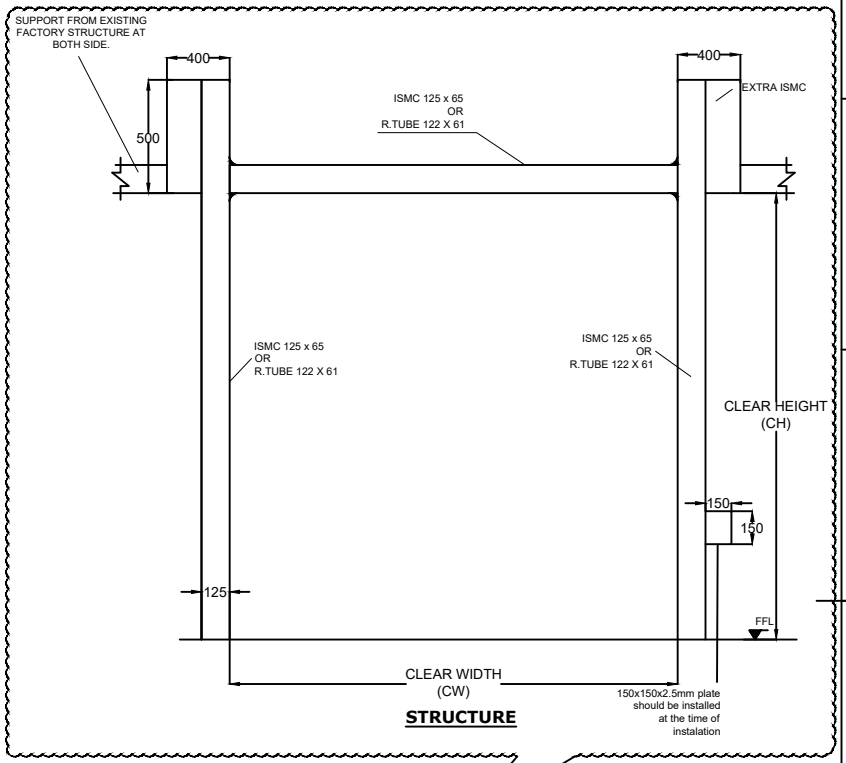

STRUCTURE


IF STRUCTURE REQUIRED FOR SHUTTER IS IN CLIENT'S SCOPE

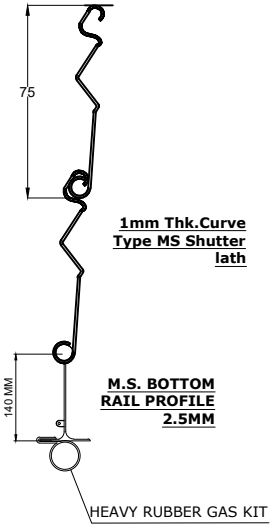

1mm Thk.Curve Type MS Shutter lath

M.S. BOTTOM RAIL PROFILE 2.5MM

M.S. BOTTOM RAIL PROFILE 2.5MM

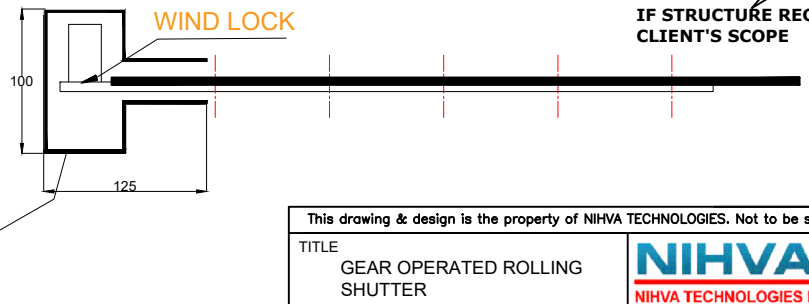

" T " TYPE GUIDE

SR NO	(CW) CLEAR WIDTH	(CH) CLEAR HEIGHT	QUANTITY
1	4500	5000	01 NO

NOTE-
1. ALL CIVIL WORK WILL BE CLIENT'S SCOPE.
2.IF STRUCTURE REQUIRED FOR SHUTTER IS IN CLIENT'S SCOPE.

This drawing & design is the property of NIHVA TECHNOLOGIES. Not to be sold or copied to any other concern.

TITLE: GEAR OPERATED ROLLING SHUTTER

	NAME	SIGN	DATE
DRAWN	B.S.		23.06.2025
CHECK	V.T.		23.06.2025
APPRD.	V.T.		23.06.2025

If any queries contact : design@nihva.com

ALL DIMENSION ARE IN mm

NIHVA TECHNOLOGIES PVT. LTD.
Website:- www.nihva.com
NIHVA TECHNOLOGIES PVT. LTD. PUNE
Tel : 020 66304033
Email:- info@nihva.com

CLIENT - TATA COMMINS

PROJECT -

SITE LOCATION -

DWG. NO. : NIHVA/21-22/VDR/020 | REV- R00

SCALE: NTS | WT: | SHEET: 01 OF 01