

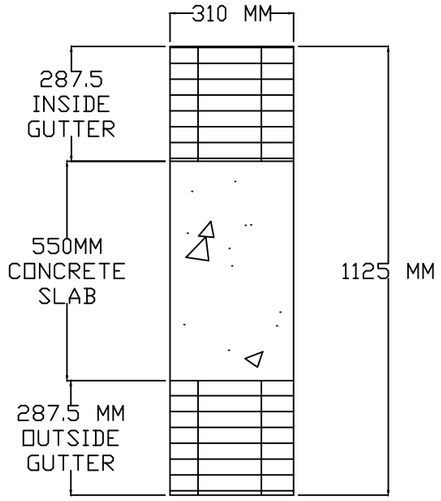



DETAIL
VIEW A
SCALE 8:1

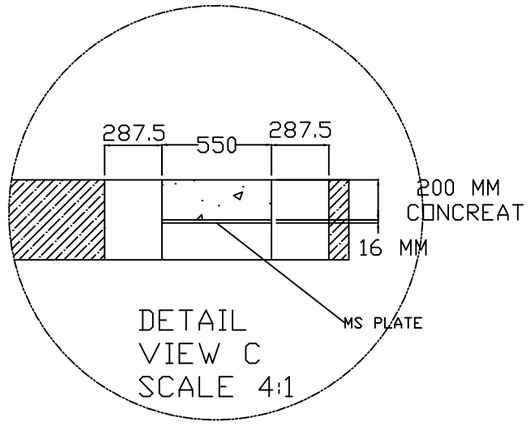

DETAIL
VIEW C
SCALE 4:1

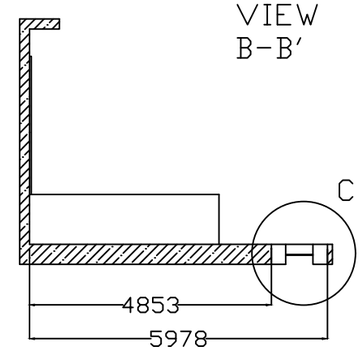

SIDE SCTION
VIEW
B-B'

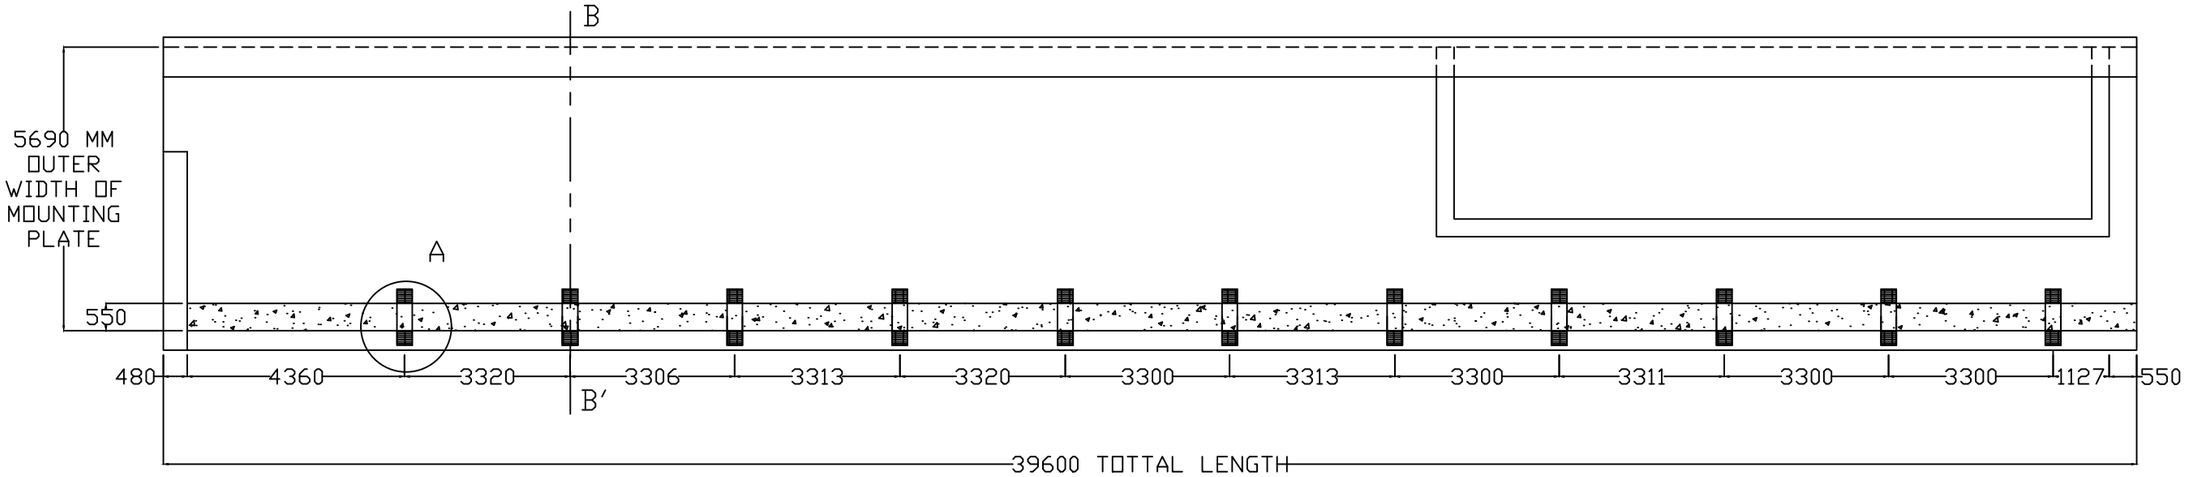

TOP VIEW

EXTENDED GUTTER LAYOUT WITH CONCREAT SLAB

This drawing & design is the property of NIHVA TECHNOLOGIES. Not to be sold or copied to any other concern.

TITLE: EXTENDED GUTTER WITH CONCREAT SLAB				NIHVA TECHNOLOGIES PVT. LTD.
	NAME	SIGN	DATE	
DRAWN	H.B.		28-04-23	CLIENT - RSGL
CHECK	P.M.		28-04-23	
APPRD.	V.T.		28-04-23	SITE LOCATION- LONAVLA
				NIHVA\22-23\00XX — REV- 0
ALL DIMENSION ARE IN mm				SCALE:1:1 — SHEET:01 OF 01