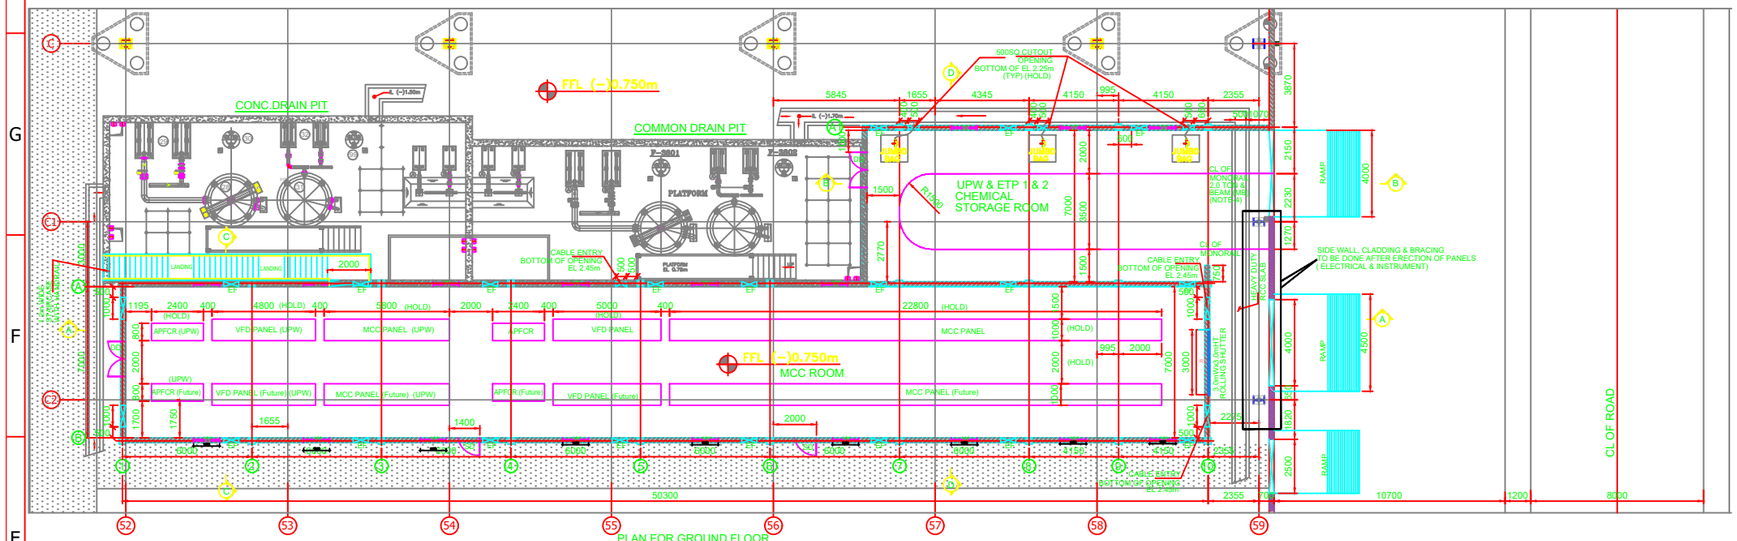
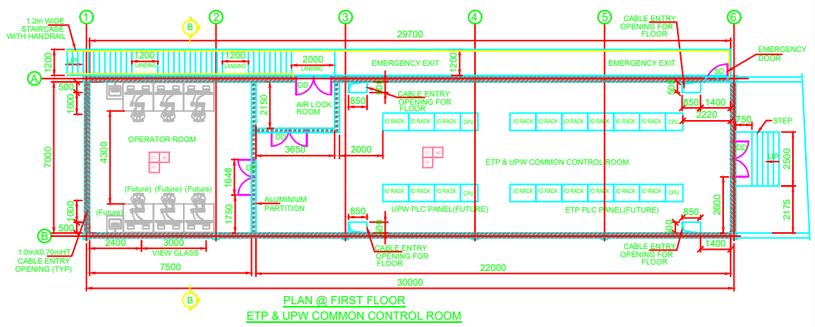
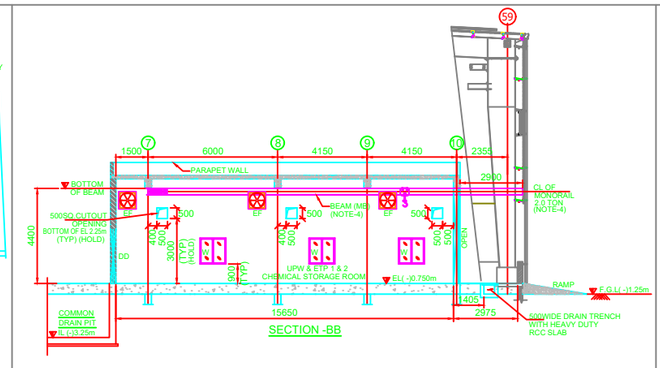
NORTH



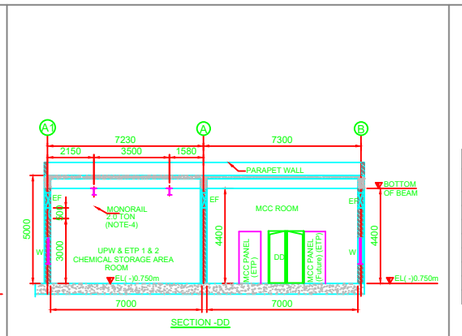

PLAN FOR GROUND FLOOR
UPW & ETP MCC ROOM



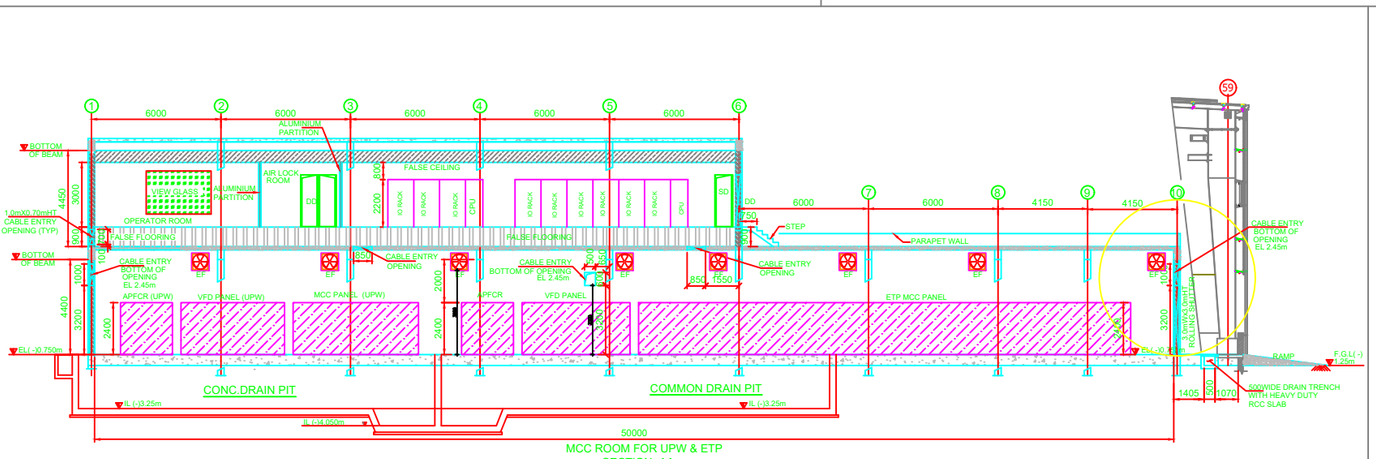

PLAN @ FIRST FLOOR
ETP & UPW COMMON CONTROL ROOM



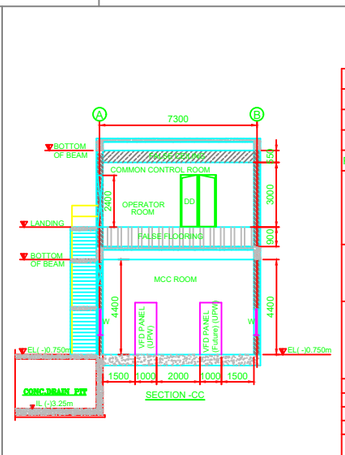

SECTION -BB



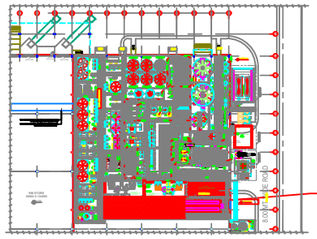

SECTION -DD




MCC ROOM FOR UPW & ETP
SECTION -AA




SECTION -CC




KEY PLAN

## NOTES:–

1. ALL DIMENSIONS ARE IN MM UNLESS OTHERWISE SPECIFIED.
2. FFL CONSIDERED AS (–)0.750m
3. INSERT PLATE FOR PIPE & CABLE TRAY SUPPORT, HANDRAIL, RUNGS, LADDER & PLATFORMS ARE IN CLIENT (RSSPL) SCOPE.
4. MONORAIL & BEAM,EXHAUST FANS & AIR CONDITIONERS ARE IN CLIENT(RSSPL) SCOPE.

## REFERENCE DRAWINGS:

| Sl.No. | GIPL DWG. No. | TITLE |
|---|---|---|
| 1 | RENEW–ETP–BEP–001 | DESIGN BASIS REPORT FOR ETP |
| 2 | RENEW–ETP–BEP–004 | PROCESS AND INSTRUMENTATION DIAGRAM FOR ETP |
| 3 | RENEW–ETP–BEP–006 | OVERALL LAYOUT FOR ETP |

## LEGEND:

FFL – FINISHED FLOOR LEVEL
FGL – FINISHED GROUND LEVEL
EL – ELEVATION
TOP – TOP OF PLATFORM
EF – EXHAUST FAN
RS – ROLLING SHUTTER.
DD – DOUBLE DOOR
SD – SIGNAL DOOR
W – WINDOW

## EQUIPMENT LIST

| SL.NO | PANEL NAME | PANEL WEIGHT (APPROX) |
|---|---|---|
| . | . | . |
| . | . | . |
| . | . | . |
| . | . | . |
| . | . | . |
| . | . | . |
| . | . | . |
| . | . | . |
| . | . | . |

| REV. | DATE | DRAWN | CHECKED | APPROVED | DESCRIPTION |
|---|---|---|---|---|---|
| 0 | 02.03.2023 | SS | JK | UK | ISSUED FOR APPROVAL |

OWNER: ReNew Power Private Limited

CONSULTANT: 中建凯德电子工程设计有限公司
CHINA KIDE ENGINEERING CORPORATION

CONTRACTOR: GRADIANT INDIA PRIVATE LIMITED
Gradiant Towers, New No.9, 100 Feet Road,1st Avenue, Ashok Nagar, Chennai 600 083, India.
Tel. +91 44 48680009, 4859 4959 / www.gradiant.com

| | NAME | DATE |
|---|---|---|
| DRAWN | SS | 02.03.2023 |
| CHECKED | JK | 02.03.2023 |
| APPROVED | UK | 02.03.2023 |

RELEASED FOR: APPROVAL / TENDER / CONSTRUCTION / INFORMATION

TITLE: CIVIL GA FOR MCC , CONTROL & CHEMICAL STORAGE BUILDING

SIZE: A1 | DWG NO: RENEW–ETP–CIVIL–009 | REV: 0

AUTOCAD FILE: | SCALE: 1:125 | JOB NO.: | SHEET: 1 OF 1