

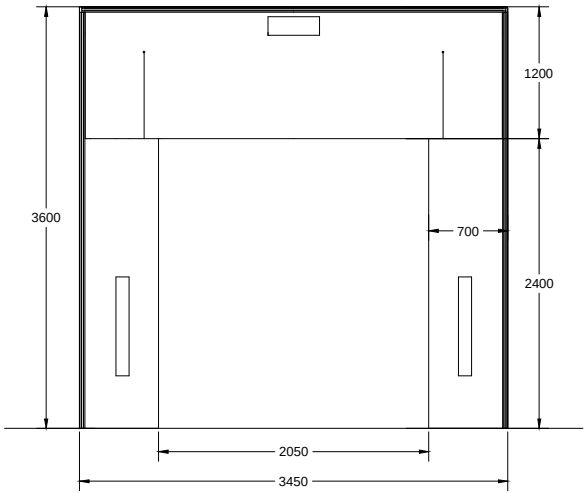



ELEVATION

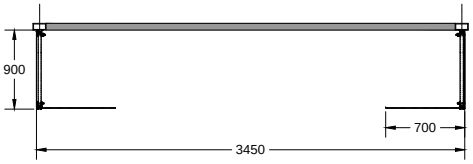

PLAN

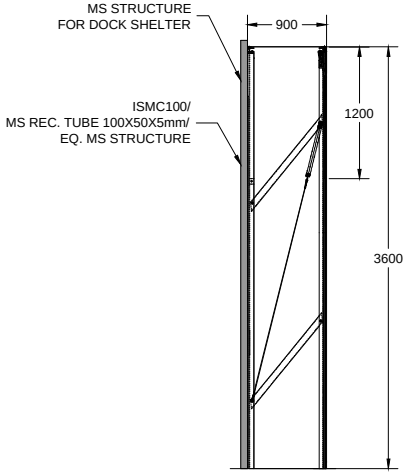

SECTION

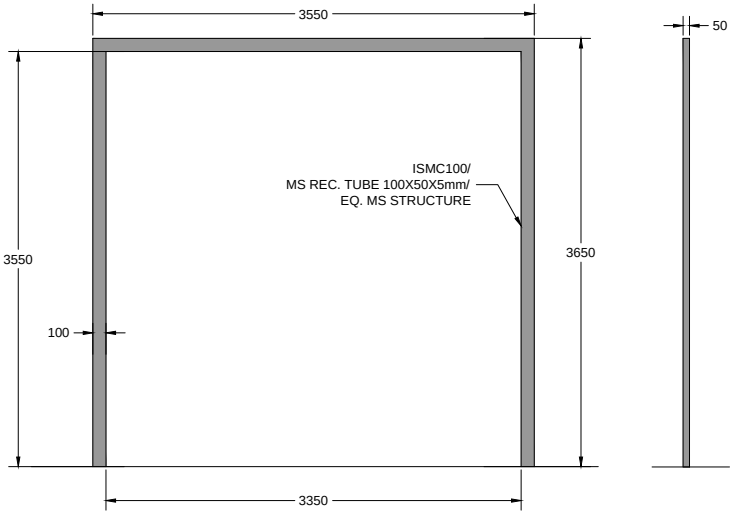

MS STRUCTRE

S.N.	SIZE	QUANTITY
1	3450(W)X3600(H)	1

TOLERANCE - ±10mm

This drawing & design is the property of NIHVA TECHNOLOGIES. Not to be sold or copied to any other concern.

TITLE

DOCK SHELTER & MS STRUCTURE 2

NIHVA TECHNOLOGIES PVT. LTD.
NIHVA TECHNOLOGIES PVT. LTD. PUNE
Tel : 020 66304033
Email:- info@nihva.com
Website:- www.nihva.com

	NAME	SIGN	DATE
DRAWN	OMKAR		27-04-2018
CHECK	PRADEEP		27-04-2018
APPRD.	PRADEEP		27-04-2018

CLIENT - LUPIN LIMITED

PROJECT -

SITE LOCATION - PIRANGUT

If any queries contact : design@nihva.com

DWG. NO. : NIHVA/18-19/0020

REV- 0

ALL DIMENSION ARE IN mm

SCALE: NTS

WT:

SHEET: 01 OF 01