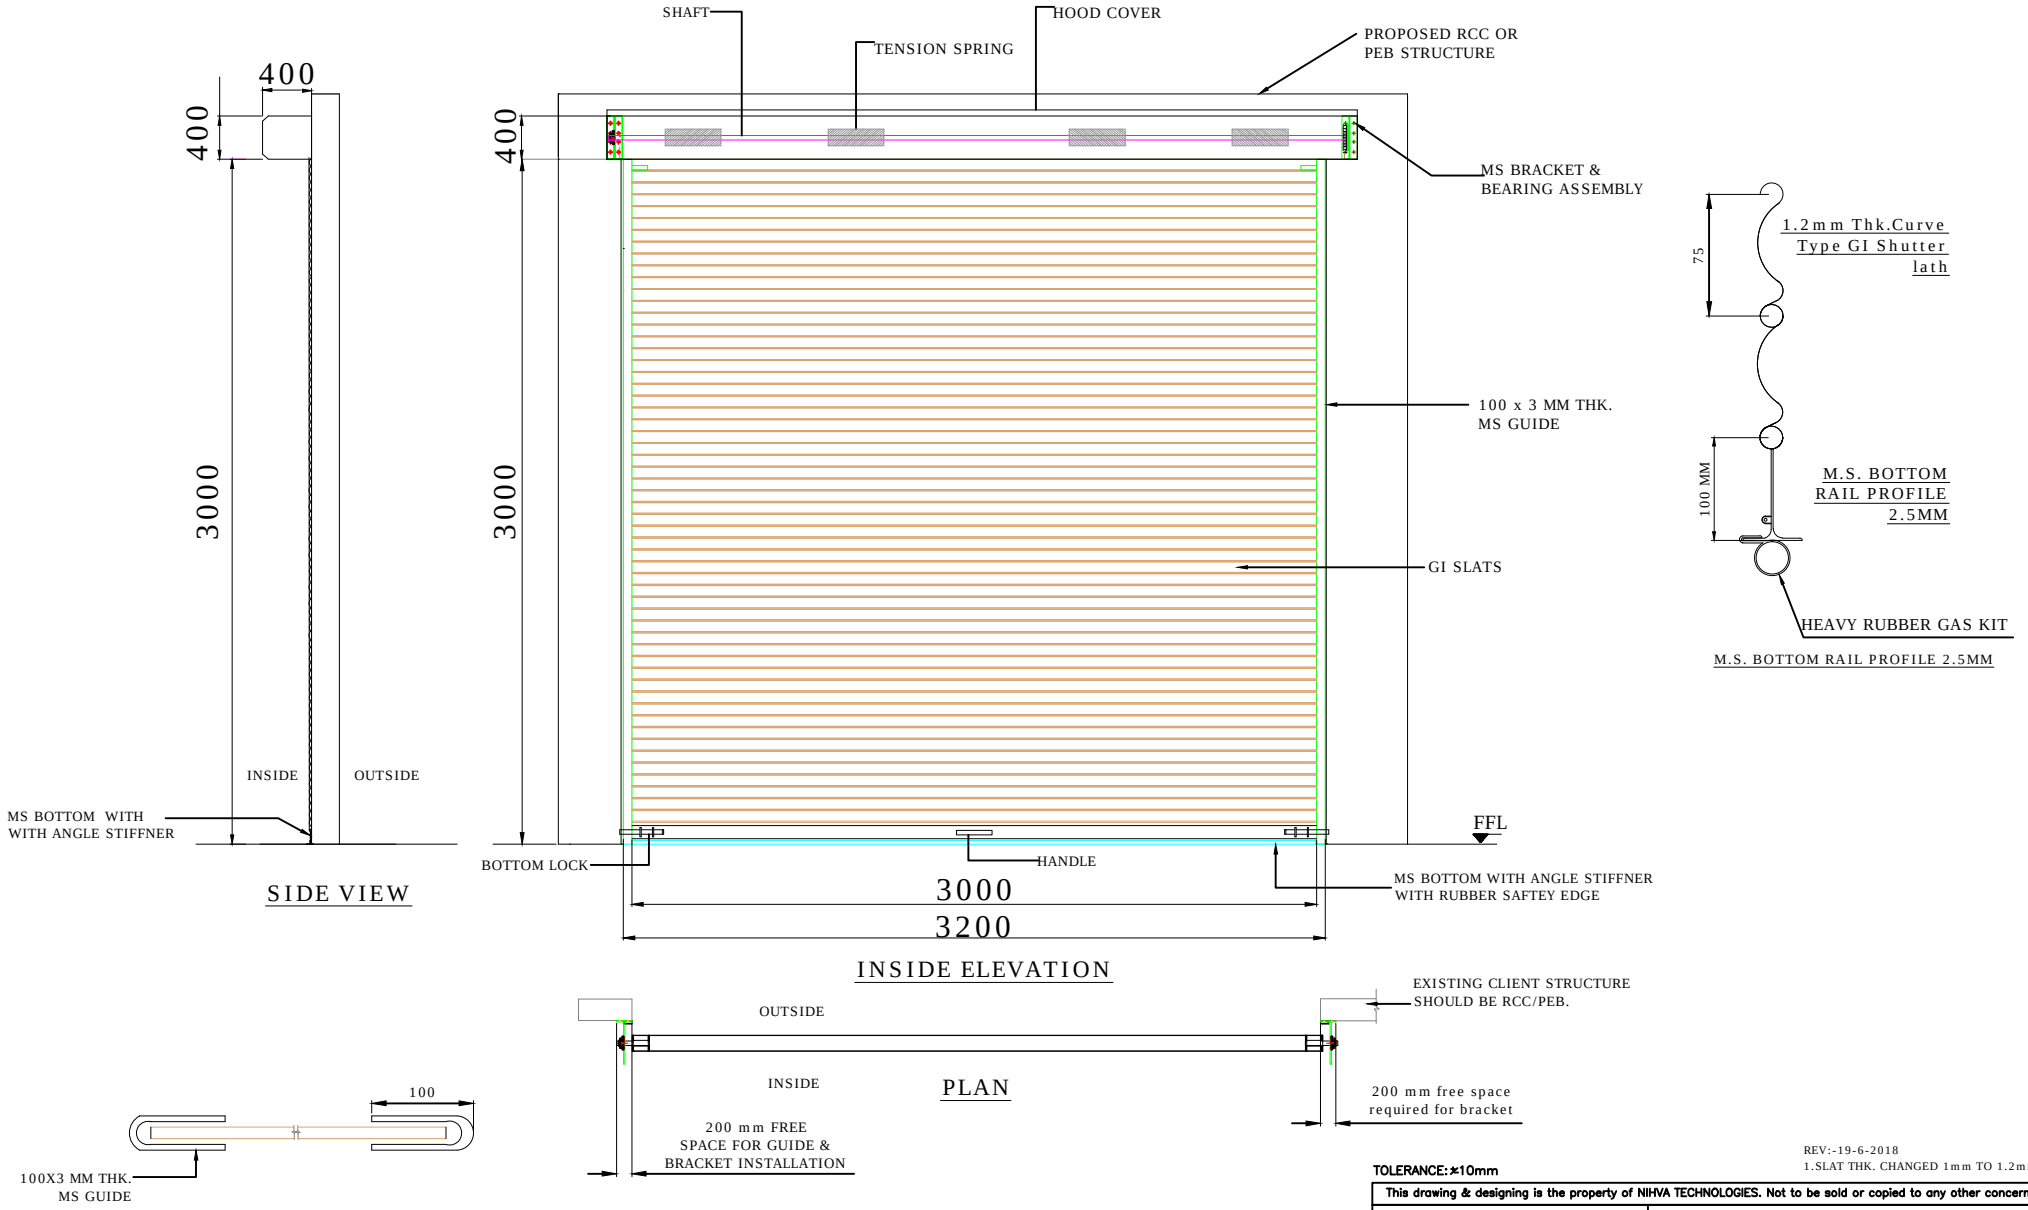

CLEAR WIDTH (CW)	CLEAR HEIGHT (CH)	QUANTITY
3000	3000	01 NO

TOLERANCE: ±10mm

REV:-19-6-2018
1.SLAT THK. CHANGED 1mm TO 1.2mm

This drawing & designing is the property of NIHVA TECHNOLOGIES. Not to be sold or copied to any other concern.

TITLE: MANUAL ROLLING SHUTTER

	SIGN	DATE
DRAWN	SURAJ	02.06.18
CHECK	PRADEEP	02.06.18
APPROVAL	PRADEEP	02.06.18
MFG.		

If any queries contact : design@nihva.com

ALL DIMENSION ARE IN mm

NIHVA TECHNOLOGIES PVT. LTD.
NIHVA TECHNOLOGIES PVT. LTD. PUNE
Tel : 020 66304033
Email:- info@nihva.com
Website:- www.nihva.com

CLIENT - Shapoorji Pallonji and Co.Pvt Ltd

PROJECT -

SITE -

DWG. NO. : NIHVA/18-19/0051/R01 | REV-01

SCALE: NTS | WT: | SHEET: 01 OF 01