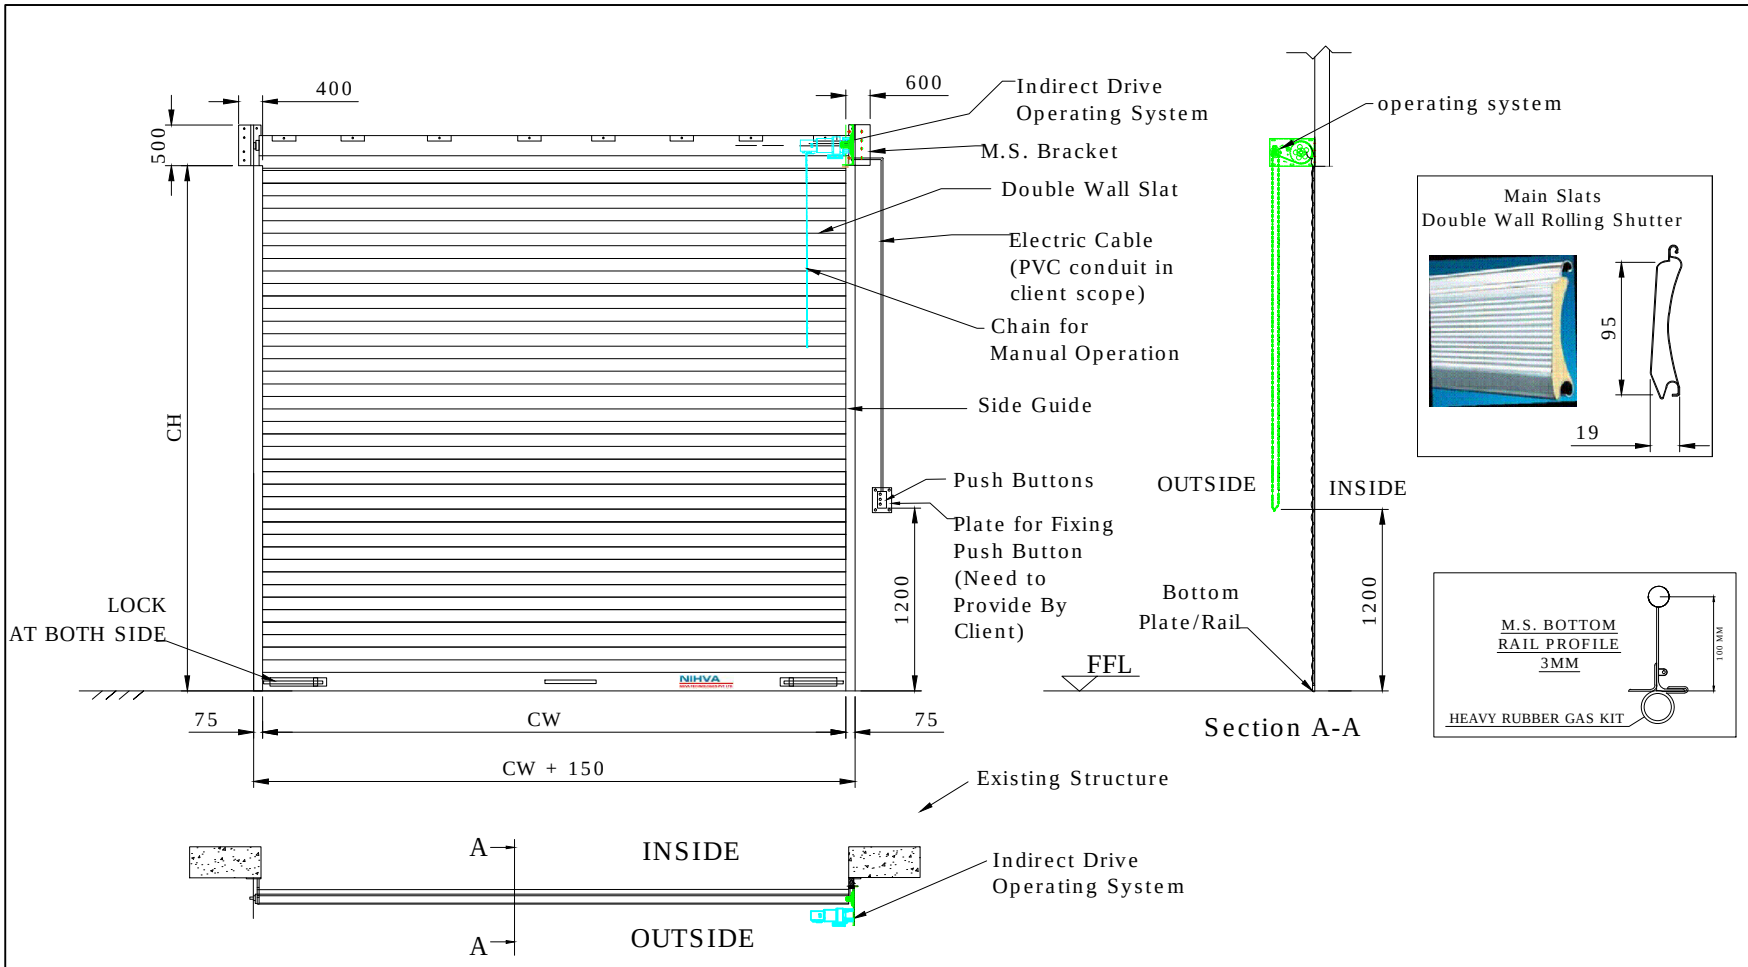


Section A-A

REV 1- CHAIN HEIGHT IS MENTIONED AS 1200mm FROM GROUND.

CLEAR WIDTH (CW)	CLEAR WIDTH (CW)	QUANTITY
2500mm	2500mm	2 NOS
3500mm	3500mm	1 NOS

DIMENSION :

CLEAR WIDTH	CLEAR HEIGHT	QUANTITY
2500mm	2500mm	2 NOS
3500mm	3500mm	1 NOS

MATERIAL :

THICKNESS :

NIHVA TECHNOLOGIES PVT. LTD.

NIHVA TECHNOLOGY
PVT. LTD. PUNE
Email:- info@nihva.com
Website:- www.nihva.com

TITLE:

DOUBLE WALL ROLLING SHUTTER

CLIENT'S APPROVAL :

CLIENT - INGERSOLL-RAND(INDIA)LTD.

PROJECT -

SITE LOCATION -AHMEDABAD

DWG. NO. : NIHVA/16-17/127/R01

SCALE: NTS	WT:	SHEET:1 OF 1

DRAWN BY: SURAJ	DATE: 21-01-2017
CHECK : OMKAR	DATE: 21-01-2017
APPROVED BY : R.K	DATE: 21-01-2017

If any queries contact : projects@nihva.com

NOTE: ALL DIMENSION ARE IN mm

THIS DRAWING & DESIGNING IS THE PROPERTY OF NIHVA TECHNOLOGIES. NOT BE SOLD OR COPY TO ANY OTHER CONCERN.