


Weitergabe sowie Vervielfältigung dieses Dokuments, Verwertung und Mitteilung seines Inhalts sind verboten, soweit nicht ausdrücklich gestattet. Zuwiderhandlungen verpflichten zu Schadenersatz. Alle Rechte für den Fall der Patent-, Gebrauchsmuster- oder Geschmacksmustereintragung vorbehalten.

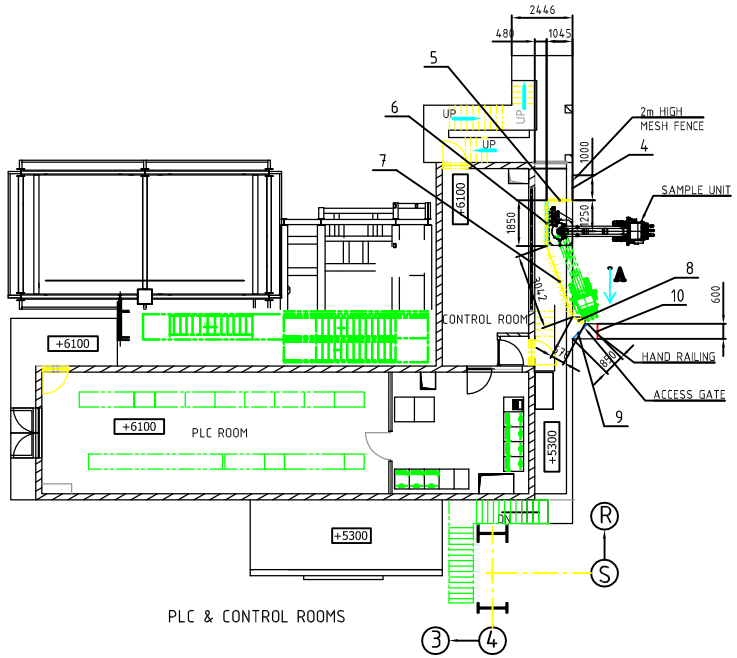


PLC & CONTROL ROOMS

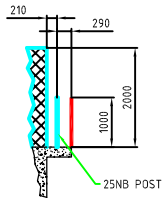

VIEW ON ARROW A
SCALE
1:50

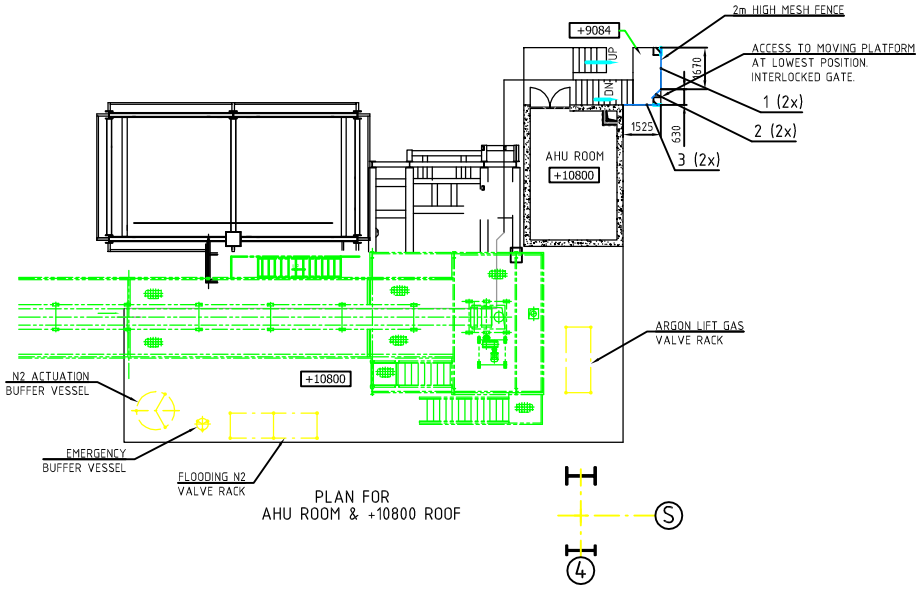

PLAN FOR
AHU ROOM & +10800 ROOF

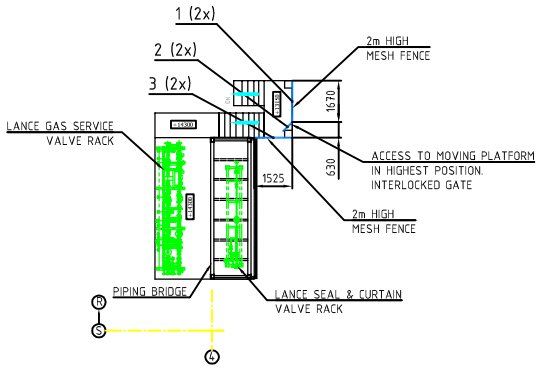

PLAN FOR
AHU ROOM ROOF (+14300)

-STATUS AS ON DATE = 16.01.2015

ITEM NO.	DESCRIPTION	QTY.
1	MESH FENCE - 1670 x 2 Mtr. HEIGHT	2
2	ACCESS GATE - W=630 x 2 Mtr. HEIGHT	2
3	MESH FENCE - 1525 x 2 Mtr. HEIGHT	2
4	MESH FENCE - 1000 x 2 Mtr. HEIGHT	1
5	MESH FENCE - 1045 x 2 Mtr. HEIGHT	1
6	MESH FENCE - 1850 x 2 Mtr. HEIGHT	1
7	MESH FENCE - 3042 x 2 Mtr. HEIGHT	1
8	MESH FENCE - 570 x 2 Mtr. HEIGHT	1
9	ACCESS GATE - W=850 x 2 Mtr. HEIGHT	1
10	HAND RAILING - 600 x 2 Mtr. HEIGHT	1

NOTES
1. EDGES OF ALL PLATFORMS, WALKWAYS ETC. TO BE FITTED WITH STANDARD HANDRAILING UNLESS OTHERWISE NOTED.
2. ALL INTERLOCKED GATES TO BE 2m HIGH.
3. ALL REMOVABLE ACCESS PANELS TO BE REMOVED USING STANDARD TOOLS.
4. FOR LEGEND REFER TO DRAWING NUMBER 1312R-D37-001.
5. 2m HIGH FENCE TO BE ERECTED EITHER SIDE OF ACCESS GATE TO PREVENT BYPASS OF GATE BY CLIMBING OVER HANDRAILING.

REV.NO.	DATE	SCALE	DESCRIPTION	BY	APPROVED
A	16.01.15	-	DRAWING UPDATED	RASI	RAUP

REVISIONS

BASIC ENGINEERING

TATA STEEL LIMITED
JAMSHEDPUR, JHARKHAND

DEPT. CODE
AREA CODE
SUBJECT CODE
TATA DRG. NO.: QTY.

Consulting Engineers: M. N. DASTUR & COMPANY (P) LTD, KOLKATA

Projekt-Nr. / Project-No.: TATA - LD 2 S3H6

Benennung / Designation: 165t DUPLEX RH UNIT
TECHNOLOGICAL STRUCTURES
SAFETY FENCING & ACCESS GATES (ECR BUILDING)

SMS SIEMAG group

	Datum	Name
Drawn	16.12.2014	PKGA
Chkd.	17.12.2014	RAUP
Resp.	17.12.2014	RAUP
Dept.	1131	
Tel.	1752	

Maßst. / Scale: 1:100
Projektionsmethode 1 / ISO 128 - First angle projection method
Fertigungsvorschriften / Manufacturing Instructions: SN 200
Werkstoff, Material
Stückgew., Unit weight: Kg
Ersetzt aus: A 1312R-D37-010
Format Size: 1
Zeichnungs-Nr./Drawing-No.: 1312R-D03-182
Änd. Index: A
CAD
Blatt / Sheet: 3 von 5

SMS Siemag - AutoCAD Version V-4455-1 / 05.09