




DWG.NO: SALT_1729_STR_12_R0

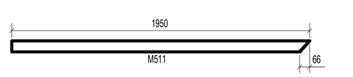


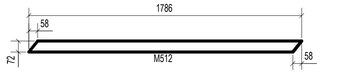

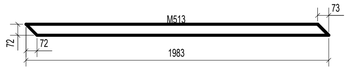


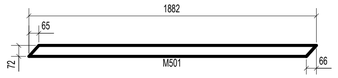


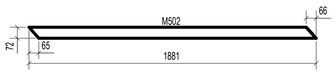


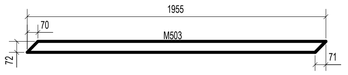





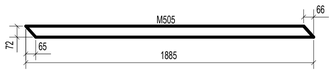

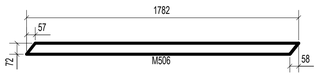


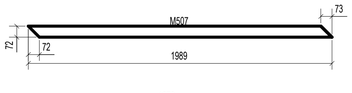


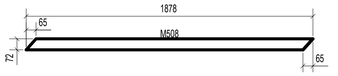


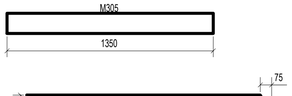





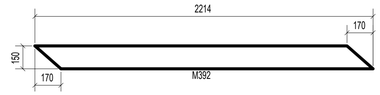


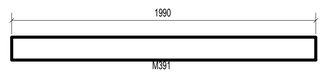


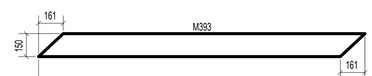


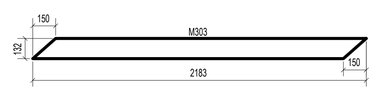

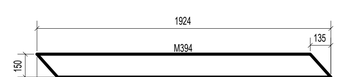


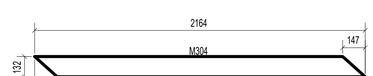


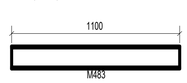


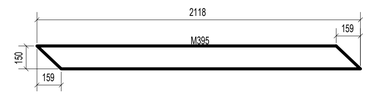





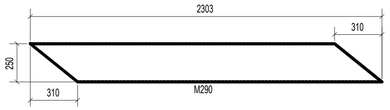


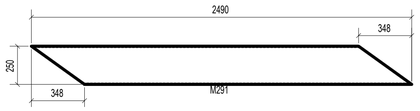


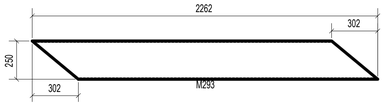


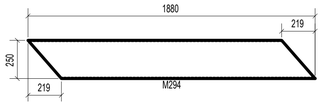


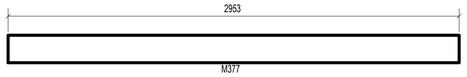

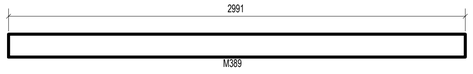


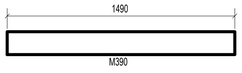


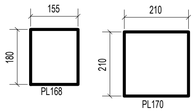


 





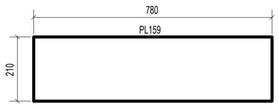


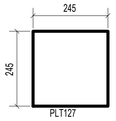

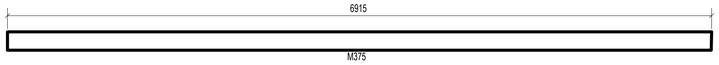


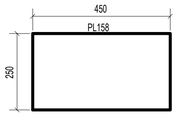


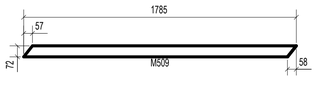


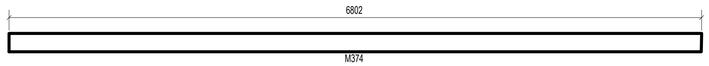





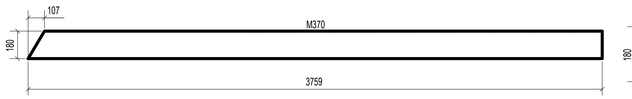


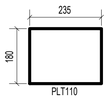


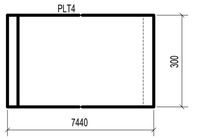


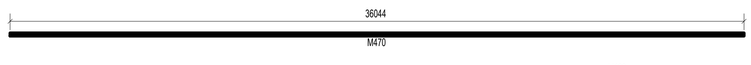


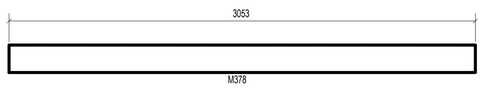


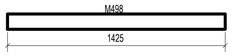


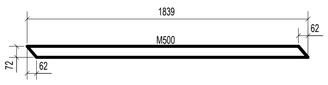


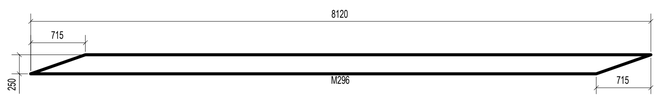


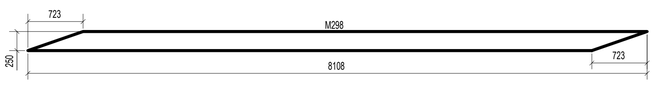


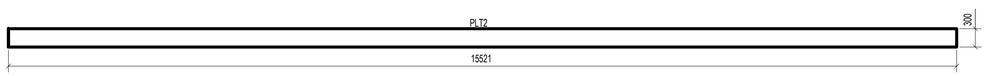


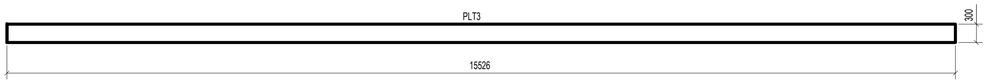


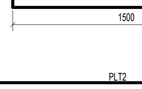


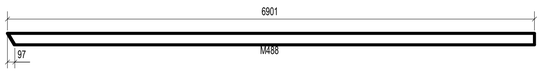


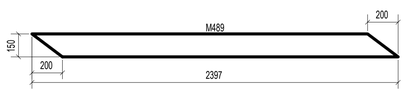


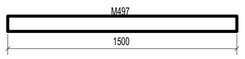


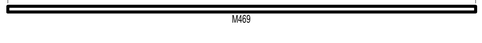


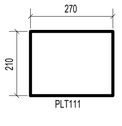


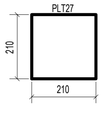


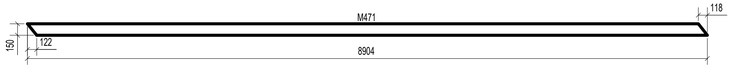


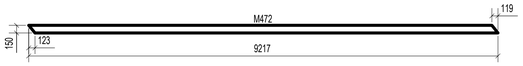


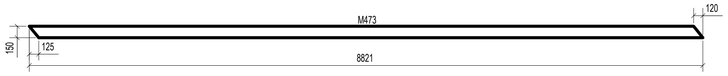


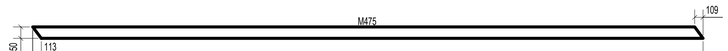

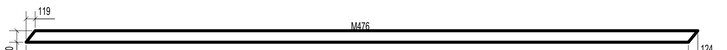


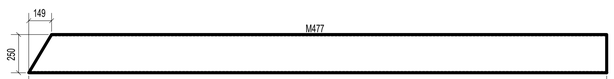


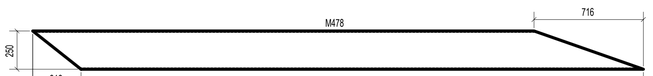


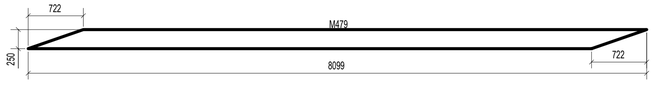





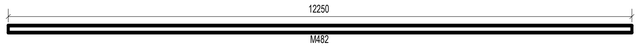


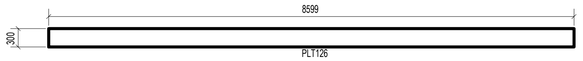


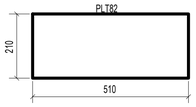


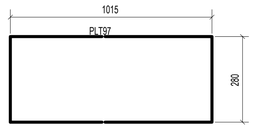


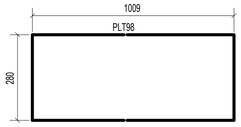


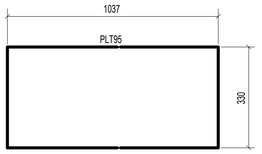


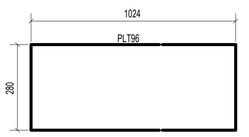


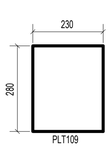


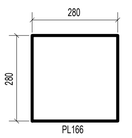


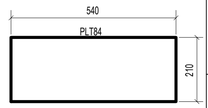


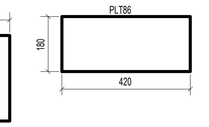


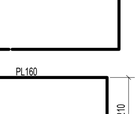

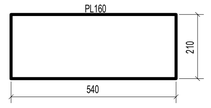


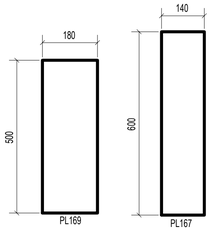


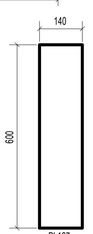


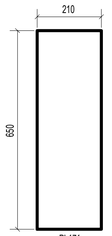





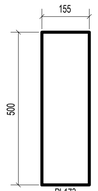


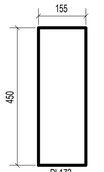


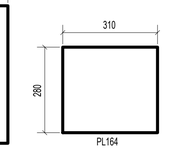


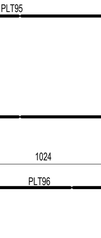


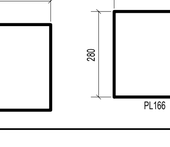

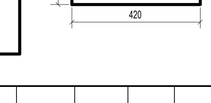


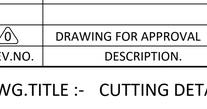


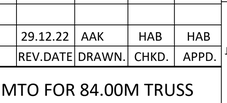

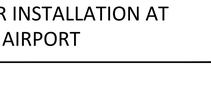



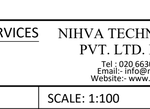

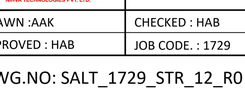



0	DRAWING FOR APPROVAL	29.12.22	AAK	HAB	HAB
REV.NO.	DESCRIPTION.	REV.DATE	DRAWN.	CHKD.	APPD.

DWG.TITLE :- CUTTING DETAILS MTO FOR 84.00M TRUSS

PROJECT	MEGADOOR INSTALLATION AT HYDRABAD AIRPORT
CLIENT	GMR

SALT Design Services
NIHVA TECHNOLOGIES PVT. LTD.

SALT DESIGN SERVICES

NIHVA TECHNOLOGIES PVT. LTD. PUNE
Tel : 020 66304033
Email:- info@nihva.com
Website:- www.nihva.com

DRAWN :AAK	CHECKED : HAB	SCALE: 1:100
APPROVED : HAB	JOB CODE. : 1729	DATE: 29.12.2022
DWG.NO: SALT_1729_STR_12_R0	(SH-1OF1)	REV. - R0
		SIZE. - A0

A1 [841 x 594]