



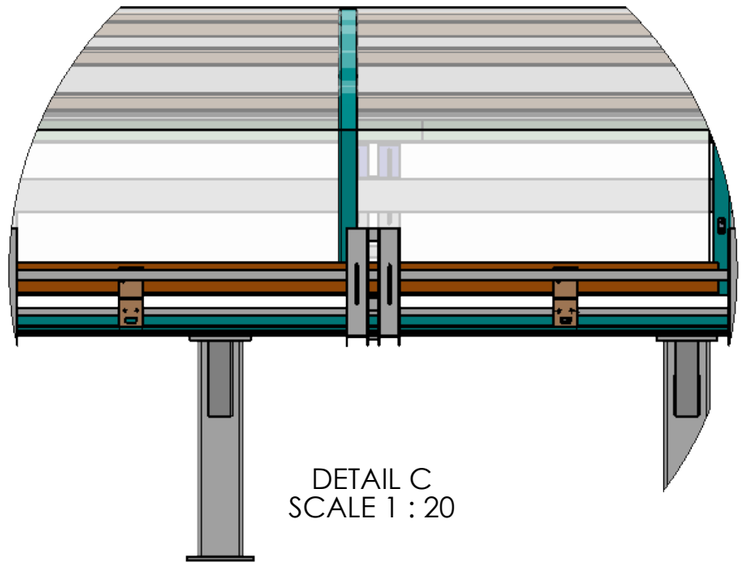

DETAIL C
SCALE 1 : 20

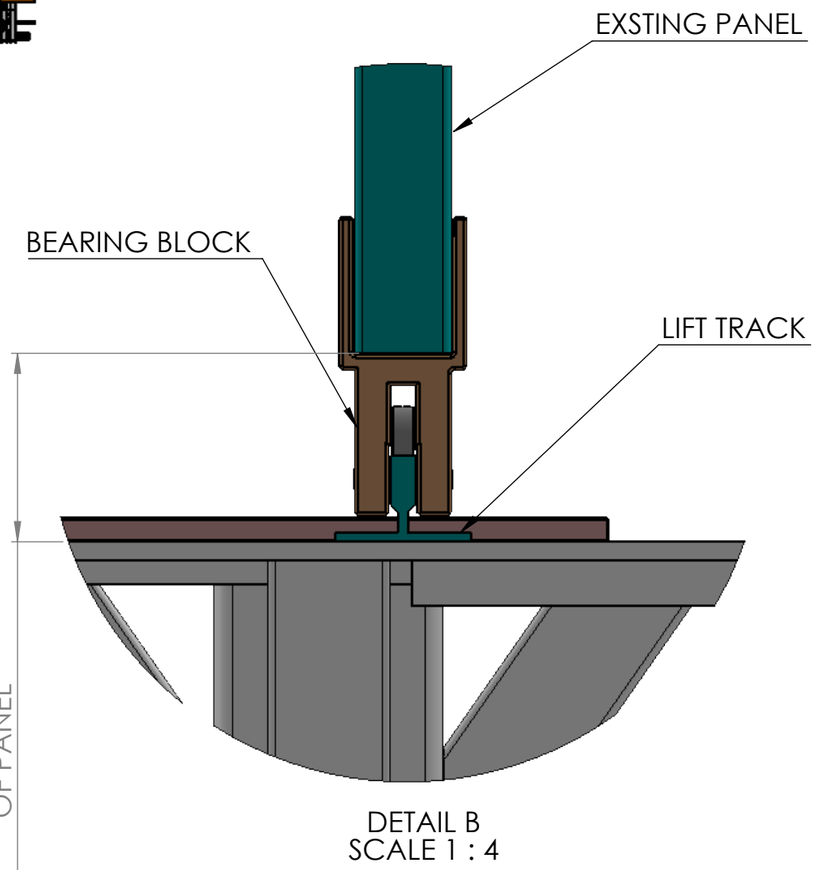


DETAIL B
SCALE 1 : 4

123
PANEL HEIGHT FROM BASE PLATE TO BOTTOM SURFACE OF PANEL




TITLE :	RK ROOF		NIHVA TECHNOLOGIES PVT LTD
	NAME	SIGNATURE	DATE
DRAWN	S.W		27-01-2025
CHK'D	PRANAV M.		27-01-2025
APPV'D	VIJAY T.		27-01-2025
CLIENT NAME :	RAHUL KOL		
PRODUCT NAME :	RR ROOF		
SITE LOCATION :	DAUND		
DWG NO.	NTPL-154		A3
			REVISION : 0
		DIMENSIONS ARE IN MILLIMETERS	SCALE: / SHEET 1 OF 3

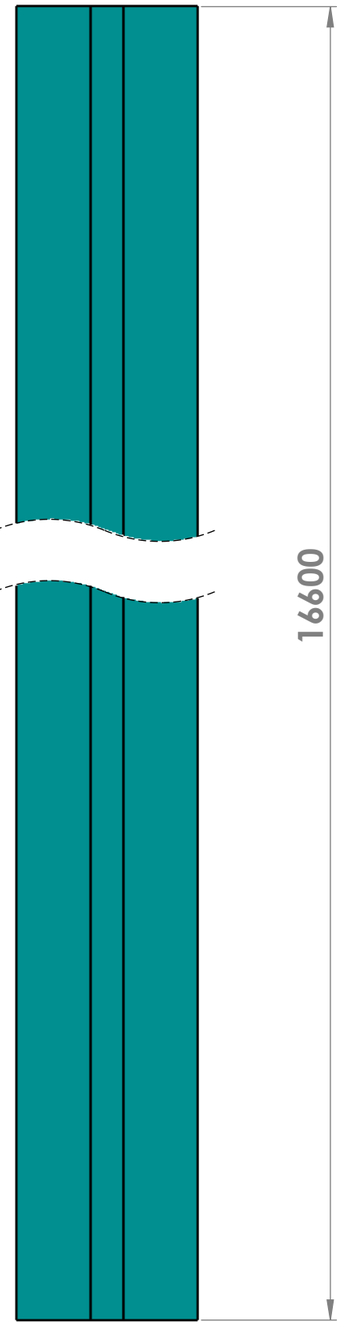





PART NAME - LIFT TRACK
PART NO - T75-1B
QTY - 5 NOS


TITLE - NTPL- 154 - LIFT TRACK				NIHVA TECHNOLOGIES PVT.LTD.PUNE Website - www.nihva.com
DWG NO - NTPL-154				
	NAME	SIGNATURE	DATE	PROJECT NO - NTPL-154
DRAWN	S.W		27-01-2025	PRODUCT - RR ROOF
CHK'D	P.M.		27-01-2025	SITE LOCATION - DAUND
APPV'D	V.T.		27-01-2025	
if any queries contact - supportautomation@nihva.com				REVISION -
ALL DIMENSION ARE IN mm			A3	SCALE - SHEET 2 OF 3

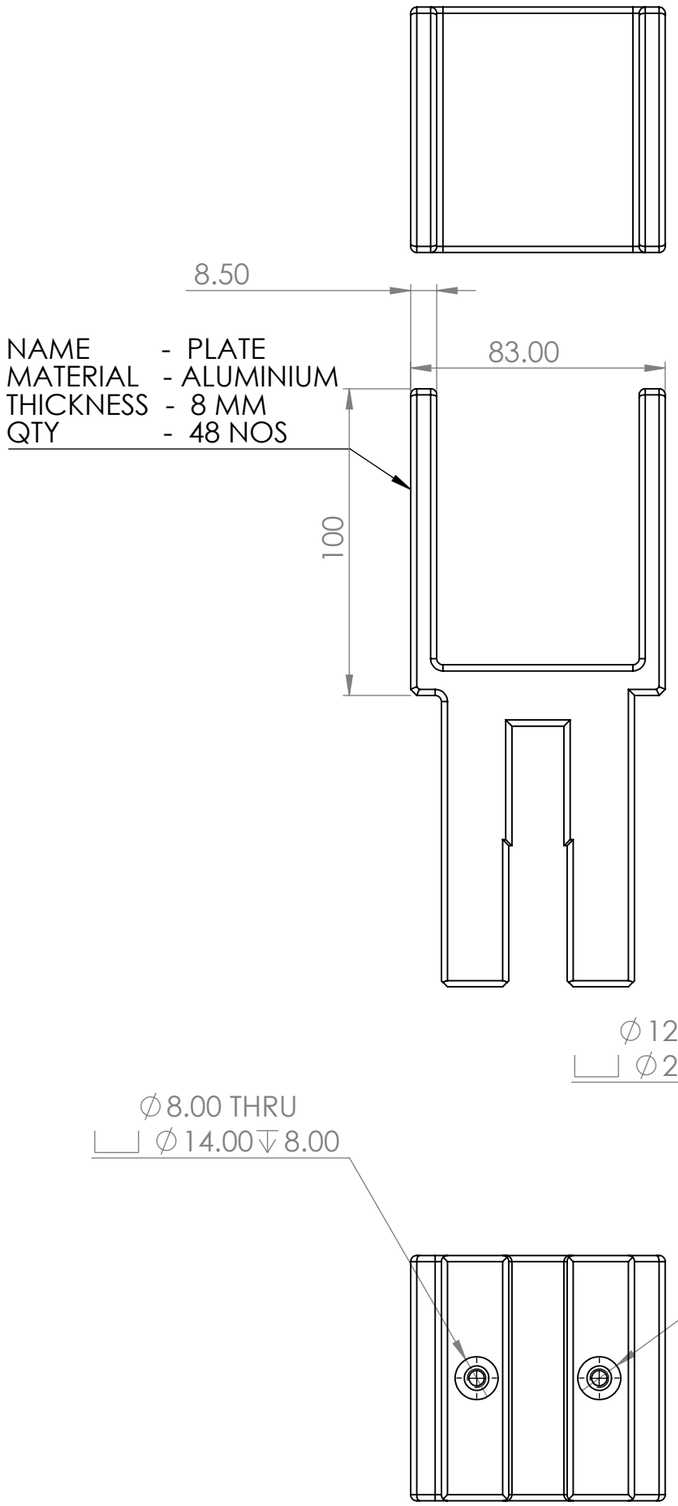


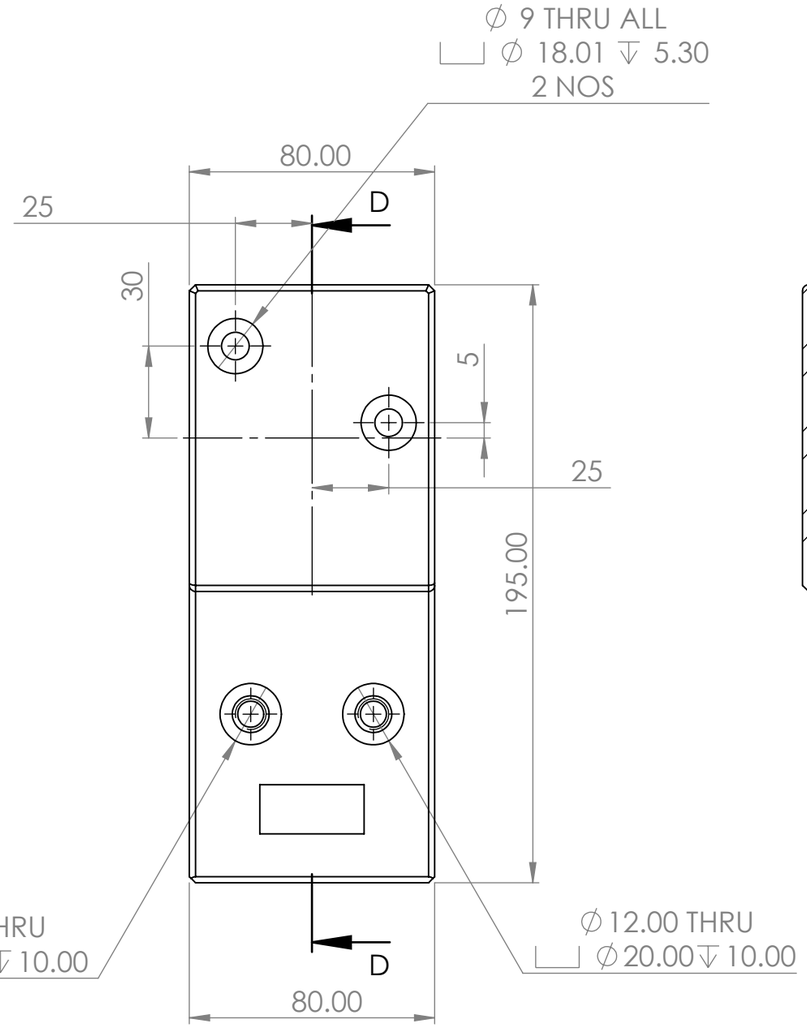

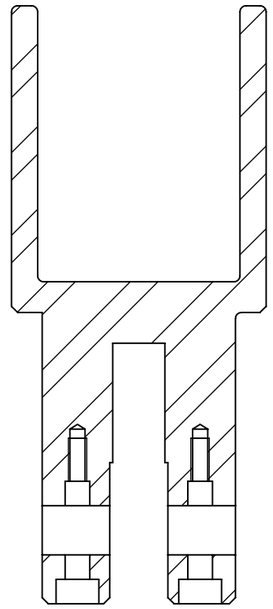

SECTION D-D

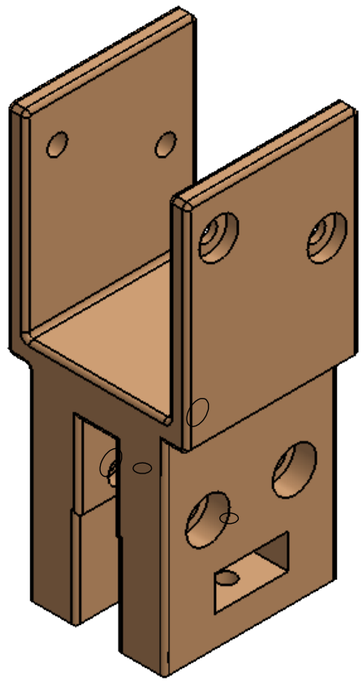

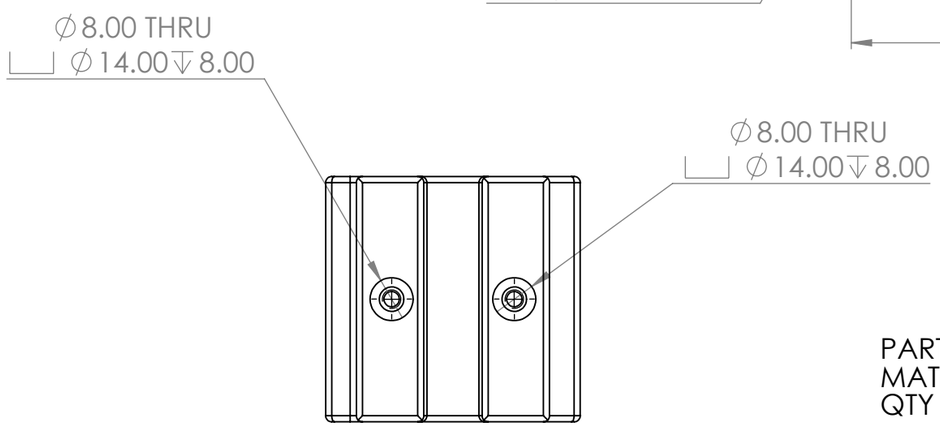

PART NAME - BEARING BLOCK
MATERIAL - ALUMINIUM
QTY - 24 NOS

VMC

TITLE - NTPL-154 - BEARING BLOCK				NIHVA TECHNOLOGIES PVT.LTD.PUNE
DWG NO - NTPL-154				Website - www.nihva.com
	NAME	SIGNATURE	DATE	PROJECT NO - NTPL 154
DRAWN	S.W		27-01-2025	PRODUCT - RR ROOF
CHK'D	P.M.		27-01-2025	SITE LOCATION - DAUND
APPV'D	V.T.		27-01-2025	
if any queries contact - supportautomation@nihva.com				REVISION -
ALL DIMENSION ARE IN mm		A3		SCALE - SHEET 3 OF 3