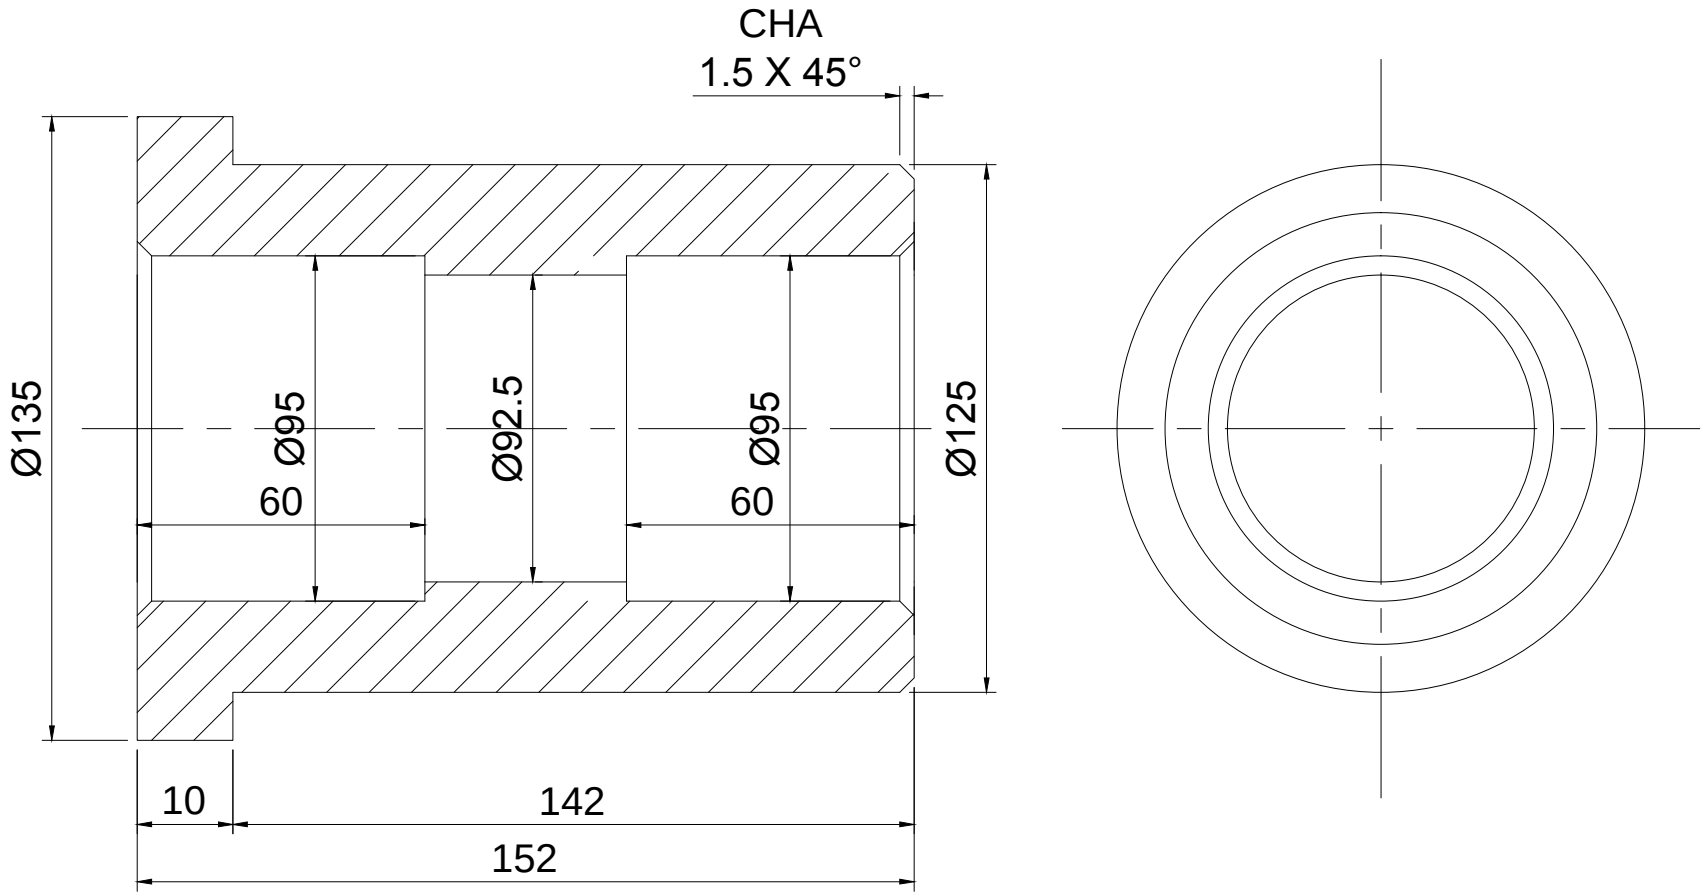


4. MS INNER ARM BUSH
   Ø135 X 155L = 02 NOS
   MU BUSH ID 90 X OD 95 X 40L = 16 NOS

REV NO	DATE	DRAWN	REMARK
REV 01	26.11.18	P.A	1. BORE DEPTH CHANGE

This drawing & design is the property of NIHVA TECHNOLOGIES. Not to be sold or copied to any other concern.

TITLE : -
INNER ARM BUSH

	SIGN	DATE
DRAWN	P.A	19.11.2018
CHECK	R.D	19.11.2018
APPROVAL		

If any queries contact : projects@nihva.com

ALL DIMENSION ARE IN mm

NIHVA TECHNOLOGIES PVT. LTD.
NIHVA TECHNOLOGIES PVT. LTD. PUNE
Tel : 020 66304033
Email:- info@nihva.com
Website:- www.nihva.com

CLIENT -
PROJECT -
SITE -
DWG. NO. : NIHVA/18-19/VDR/216/R01
SCALE: NTS | WT: | SHEET: 01 OF 01