



FRONT ELEVATION

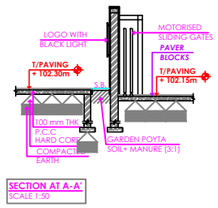

SECTION AT A-A'
SCALE 1:50

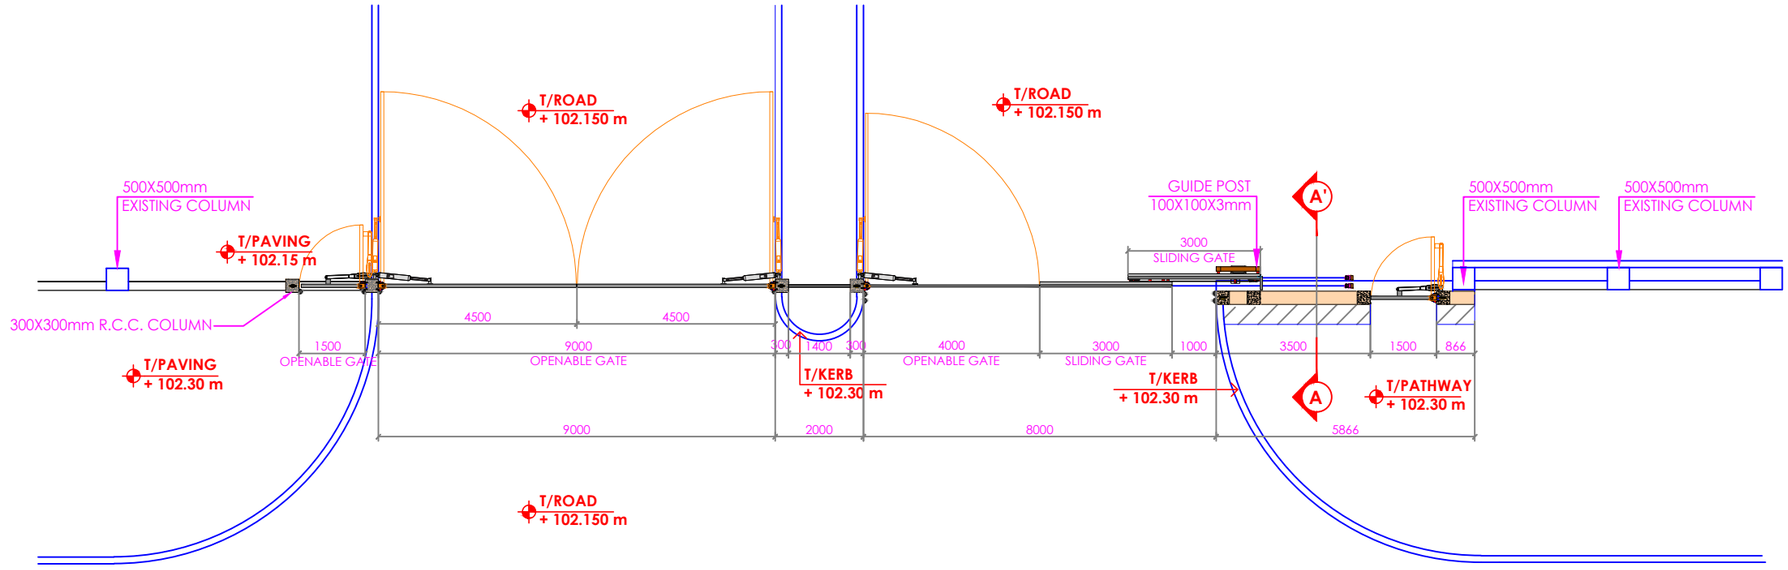

PLAN

BOOM BARRIER
1.BOOM BARRIER CLEAR OPENING= 4500mm= 2 nos.
2.BOOM BARRIER CLEAR OPENING= 3000mm= 2 nos.
3.BOOM BARRIER CLEAR OPENING= 5000mm= 1 nos.
ALL BOOM BARRIERS WITH
-LED LIGHTING SYSTEM WITH VARIABLE FLASHING
-POLYCAB FLEXIBLE CABLE

NOTE:
1.ALL GATES ARE MOTORISED.
2.GATES WITH MILD STEEL WITH TWO COATS OF POLYURETHANE SPRAY PAINT OVER ONE COAT OF EPOXY PRIMER.