
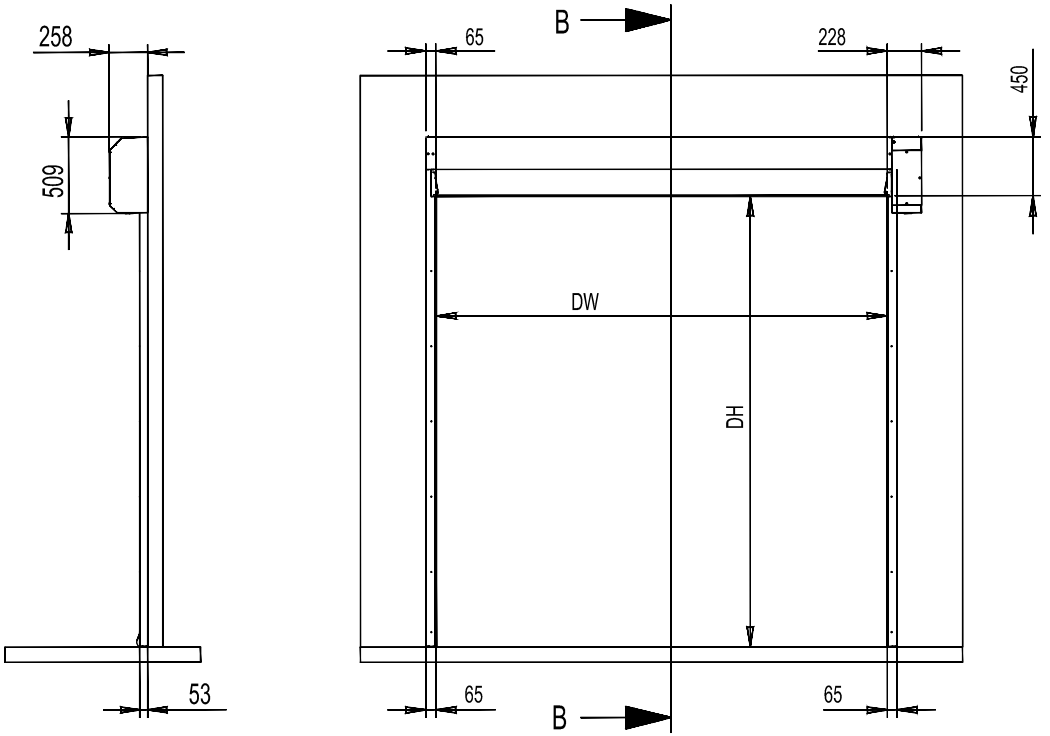


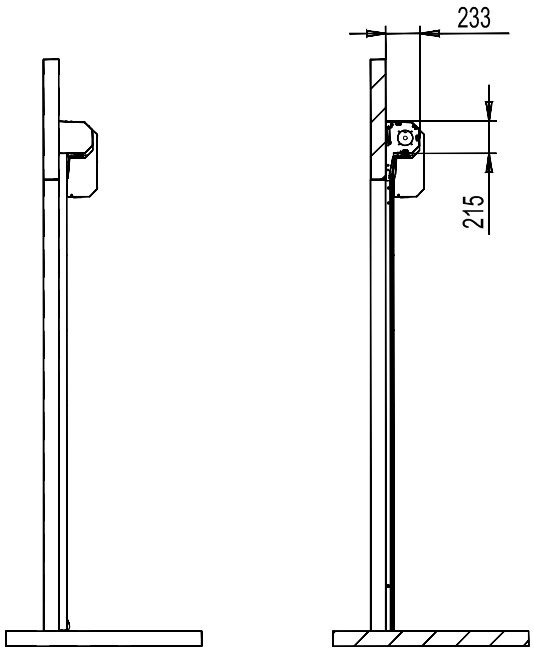

SECTION B-B

DOOR DIMENSION				
SR NO	DW	DH	MOTOR LOCATION	QUANTITY
1	2420	3000	RIGHT HAND SIDE	18
2	2420	3000	LEFT HAND SIDE	01

Accessories/ Features considered-
1. Soft bottom safety edge.
2. Push buttons both side.
3.Magnetic loop detector - Outside
4.Emmergency stop
5.Safety catch
6.Flashing lights both side

Power Supply(Supply & UPS is in client's scope)

1. If motor is single phase then Single phase 230V, 50 Hz supply required.
   UPS Capacity- 2 KVA/ door
2. If motor is three phase then Three phase 430V, 50 Hz supply required.
   UPS Capacity- 3 KVA/ door

Door Curtain color- Grey (RAL 7035)
Note- All required civil work will be client's scope.

This drawing & designing is the property of NIHVA TECHNOLOGIES. Not to be sold or copied to any other concern.

TITLE: HIGH SPEED DOOR HS9020

NIHVA TECHNOLOGIES PVT. LTD. PUNE
Tel : 020 66304033
Email:- info@nihva.com
Website:- www.nihva.com

	NAME	SIGN	DATE
DRAWN	OMKAR		09/02/18
CHECK	SHEKHAR		09/02/18
APPROVAL	SHEKHAR		09/02/18

CLIENT - DEV TECHNOSKILL
PROJECT - AMAR TEA PROJECT
SITE - UMARGAON, GUJARAT

If any queries contact : design@nihva.com
DWG. NO. : NIHVA/17-18/0357 REV- 0
ALL DIMENSION ARE IN mm
SCALE: NTS WT: SHEET: 01 OF 01